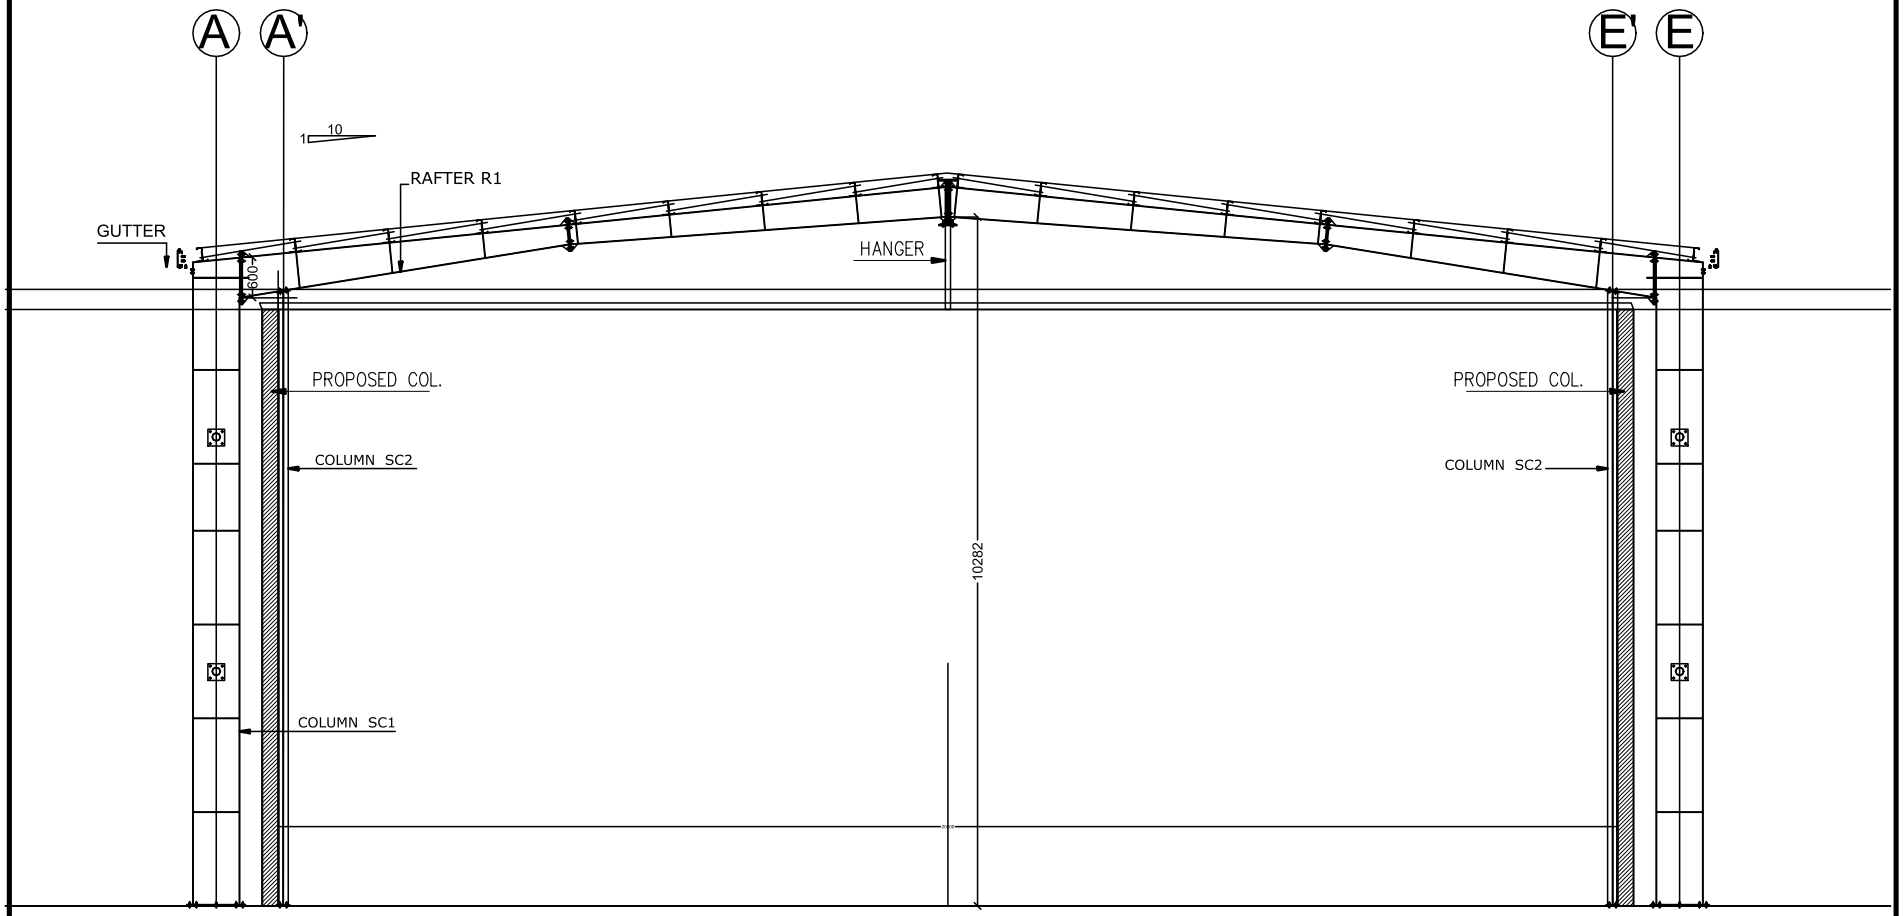


PORTAL FRAME 3 ELEVATION

GENERAL NOTES:-

1) ALL DIMENSIONS ARE IN MILLIMETER AND LEVELS IN METER UNLESS NOTED OTHERWISE.
2) DRAWINGS SHALL NOT BE SCALED. ONLY DIMENSIONS INDICATED ON THE DRAWING ARE TO BE FOLLOWED.
3) ALL STRUCTURAL DRAWINGS TO BE READ IN CONJUNCTION WITH ARCHITECTURAL AND SERVICES DRAWINGS AND SPECIFICATIONS.
4) FOR COLUMN CENTER LINES REFER ARCHITECTS DRAWINGS.
5) REINFORCING BARS SHALL CONFORM TO IS:1786
6) AGGREGATES SHALL CONFORM TO IS:386(1970).
7) PROVIDE LAPS ONLY IF REQUIRED AT LOCATIONS SHOWN. THE LAP LENGTH U.N.O. SHALL BE AS GIVEN BELOW:

GRADE OF CONCRETE	Ld ANCHORAGE & LAP LENGTH	GRADE OF CONCRETE	Ld ANCHORAGE & LAP LENGTH
25	50 X BAR DIA	35	40 X BAR DIA
30	45 X BAR DIA	40 & ABOVE	35 X BAR DIA

PROVIDE COUPLERS FOR 32Ø AND GREATER REINFORCEMENT.

8) BENDING AND BINDING OF REINFORCING BARS SHALL CONFORM TO IS:2502
9) MINIMUM CLEAR COVER TO REINFORCING BARS SHALL BE AS FOLLOWS: FOUNDATIONS, FOUNDATION BEAMS (SIDES/TOP/BOTTOM) = 50MM COLUMNS UP TO PLINTH= 40MM,STEM OF RETAINING WALL= 40 MM FLOOR SLABS =20MM (100 THK. SLAB = 15 mm), FLOOR BEAMS - BOTTOM =40MM FLOOR BEAMS - TOP & SIDES, COLUMNS, LINTELS = 30MM
10) NOT MORE THAN 50% OF THE BARS SHALL BE SPLICED AT ONE SECTION.
11) DISCREPANCY IF ANY SHALL BE BROUGHT TO THE NOTICE OF THE REPRESENTATIVE OF THE CONSULTING ENGINEER BEFORE EXECUTION OF WORK
12) CONCRETE GRADE SHALL BE M:30 U.N.O.
13) CONTRACTOR SHALL BE FULLY RESPONSIBLE FOR ALL TEMPORARY WORKS AND SHORING WORK.

No	Description	By	Chk	Date
RO	FOR STUDY	R.P.	S.K	17.10.2019

DrawingTitle : ELEVATION FOR MEGADOOR

Project Title : MEGADOOR AT SERUM INSTITUTE OF INDIA PVT. LTD.

Drawn by : R.P. | Approved by : R.M.

Checked by : S.K | Date : 17.10.2019

M.E.P. Consultant :

Production Architect :

Architect :

Client : NIHVA technologies Pvt. Ltd.
187, G-Block, Thermax chowk, MIDC Chinchwad, Pune, India

Structural consultant:
Design Werkz Engineering Pvt.LTD
A-1 Liberty Society, 1st Floor, North Main Road, Koregaon Park, Pune-411001. INDIA.
Tel : +91 020 48603422
web: www.designwerkz.in

Job no: -

Dwg. No: ST-101 | Drg. Size: A2

Sheet. No: 1/3 | Rev. No: R0

Scale: AS SHOWN

Drawing status: FOR STUDY

This drawing is the property of *Design* ***Werkz Engineering Pvt.LTD*** and shall not be reproduced or used without written permission.