

PROPOSED PLAN LAYOUT

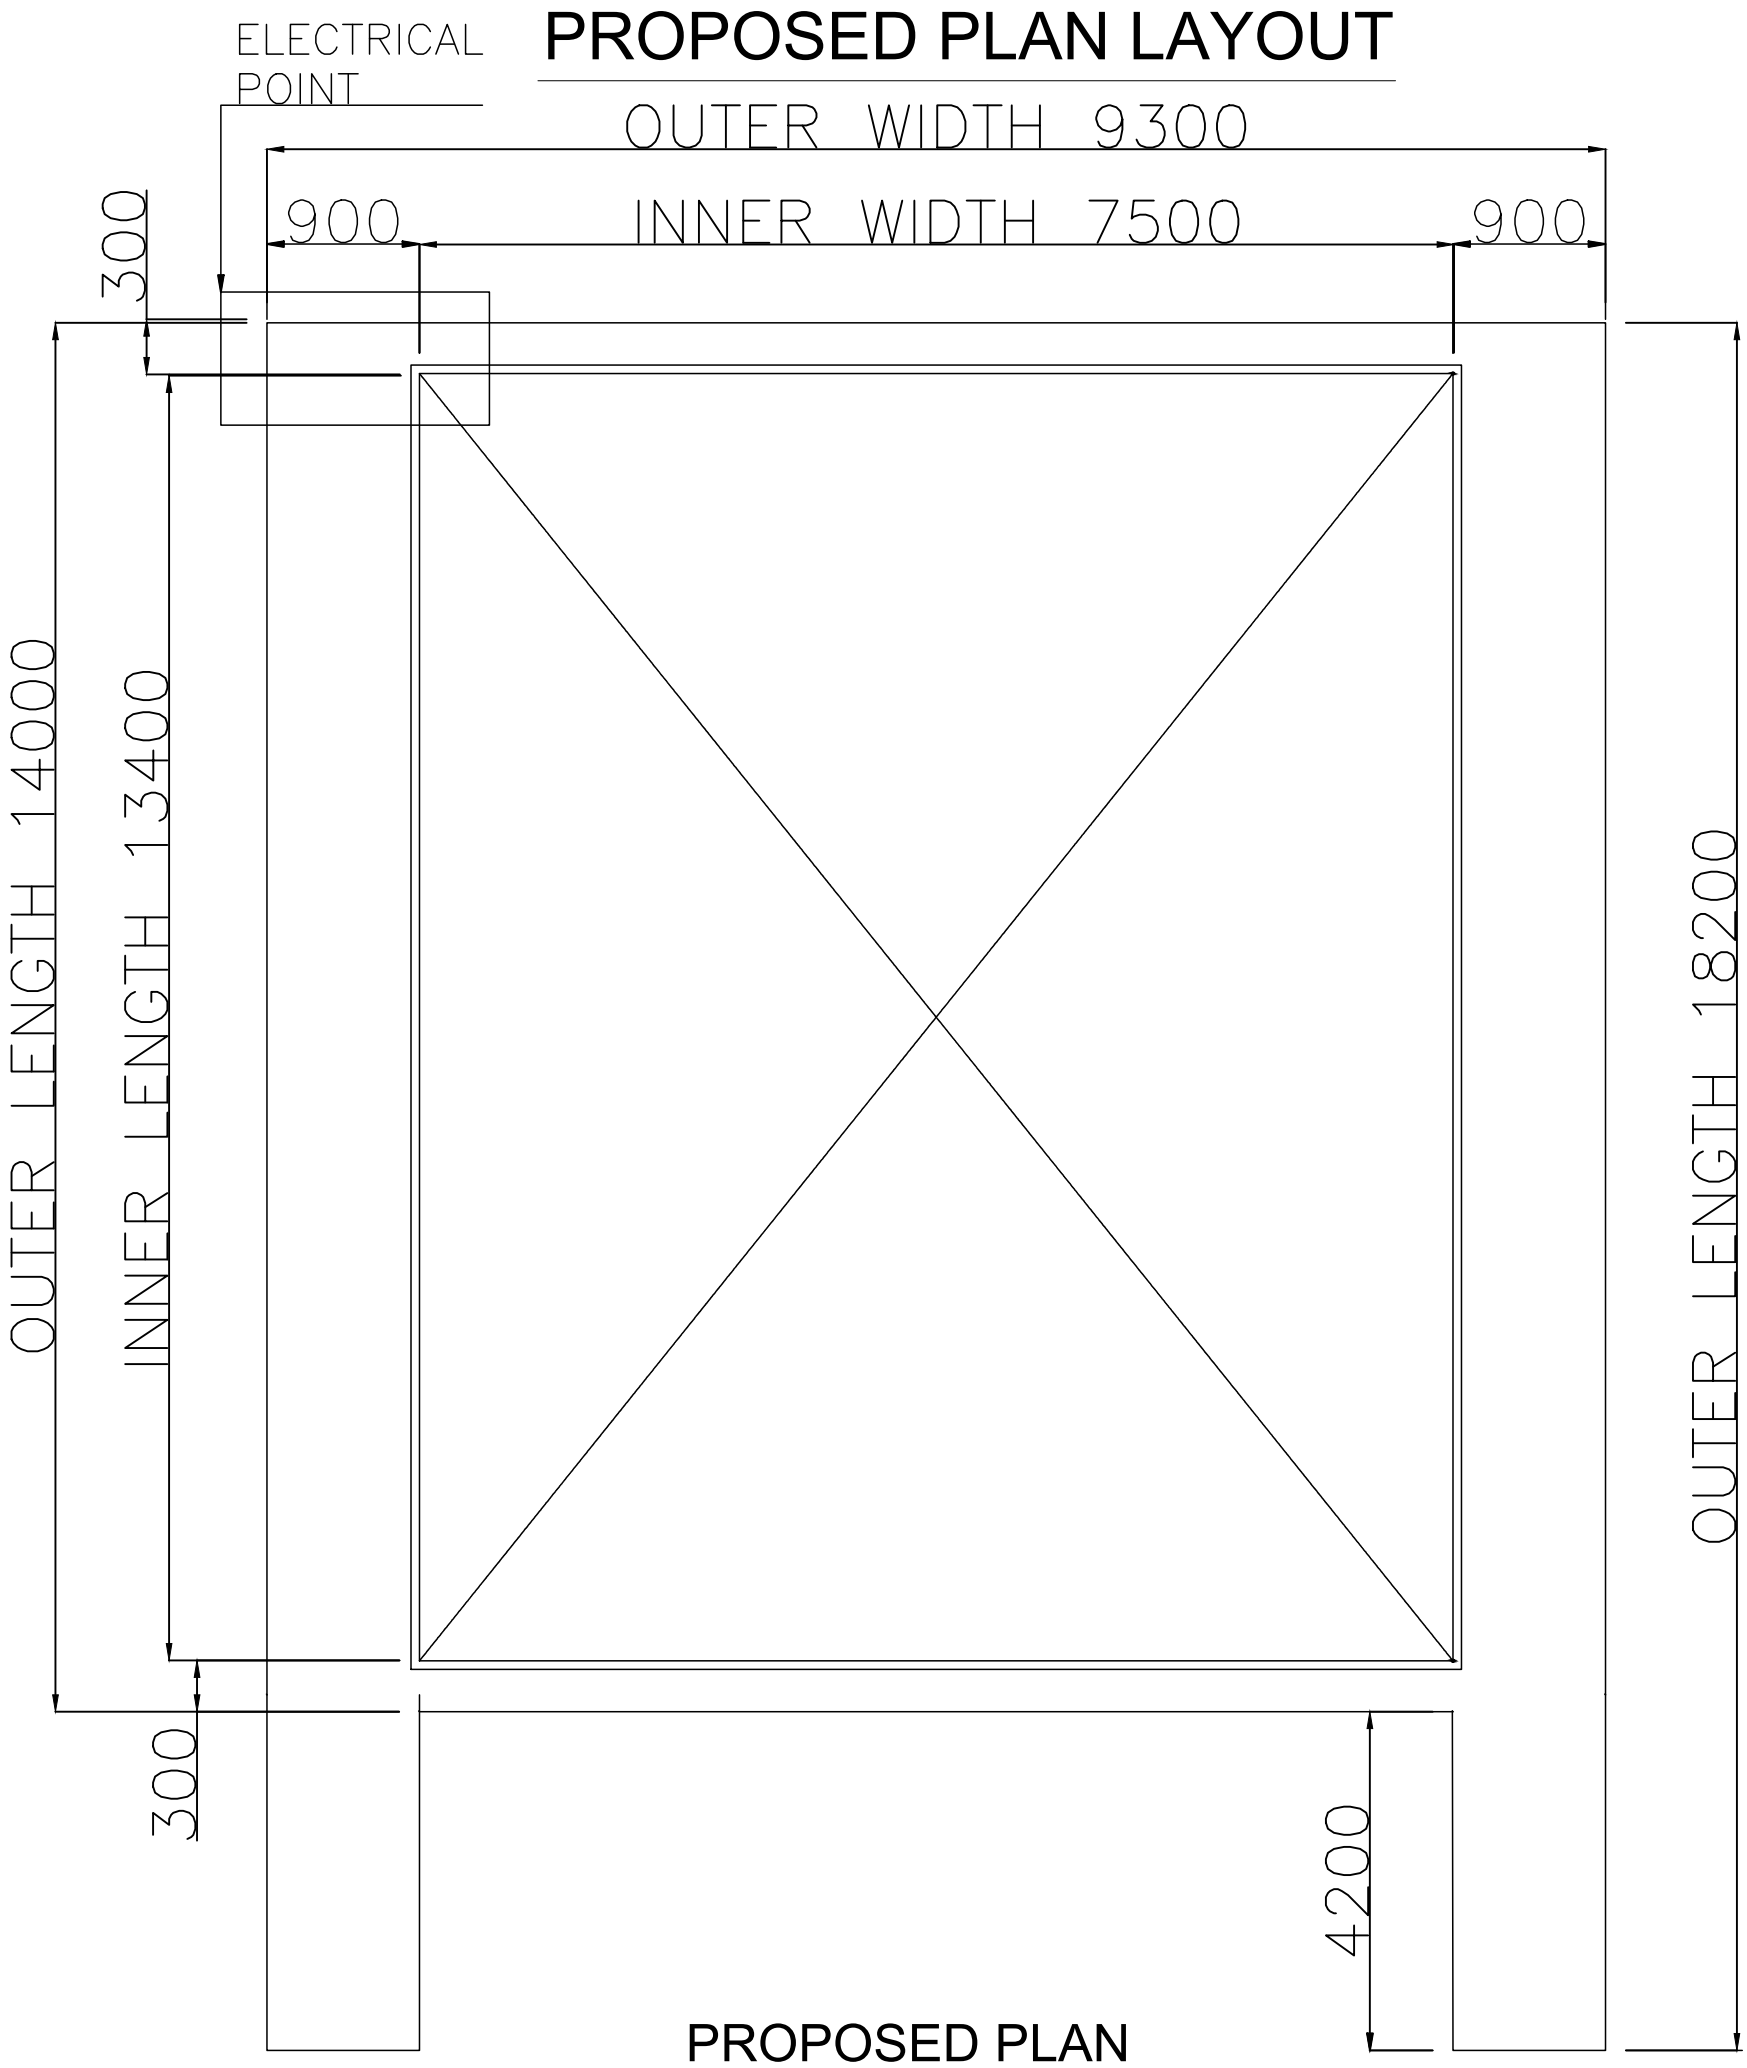

PROPOSED PLAN

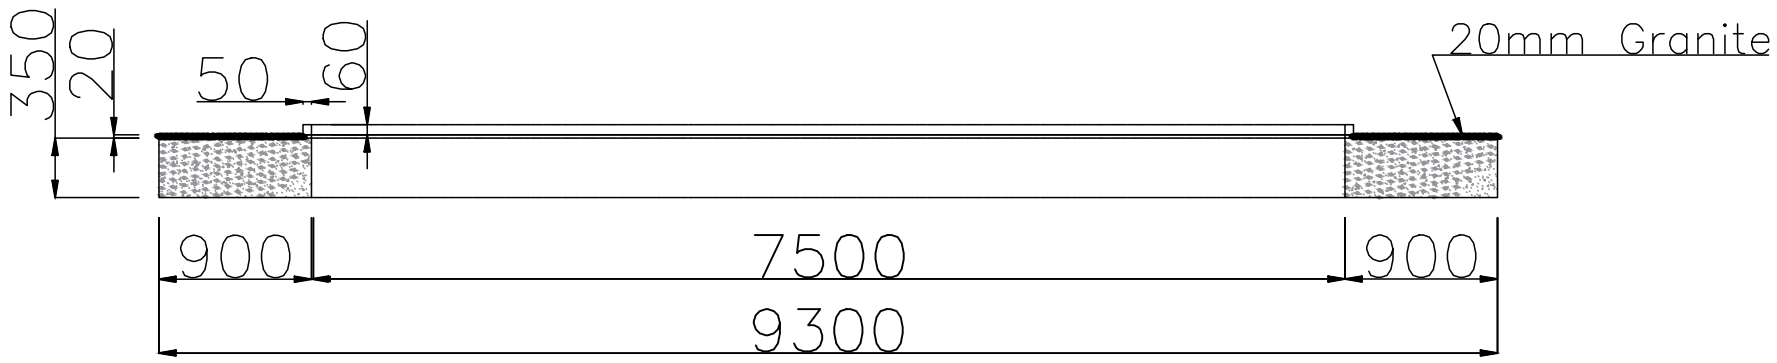

SECTION VIEW

1. THE STRUCTURE AROUND THE CUT OUT SHOULD BE OF CONCRETE FOR FOR PROPER FASTENING OF ROOF.
2. TOP SURFACE SHOULD BE OF GRANITE 20MM FOR SMOOTH FUNCTIONING OF ROOF.
3. ROOF EXTENSION IS SHOWN FOR ONLY REFERENCE. IT CAN BE MODIFIED AS PER THE WORK UNDERTAKEN.
4. GRADIENT OF 50MM NEED TO BE PROVIDED ALONG THE OUTER LENGTH TO AVOID WATER STAGNANCY IN GUIDE RAIL.
5. AL PROFILE - POWDER COATED
6. GASKET - EPDM
7. MOTOR - ITALIAN/GERMAN MAKE
8. ALL DIMENSION IN MM.
9. PROPOSED CIVIL PLAN LAYOUT (IN CLIENT SCOPE)

This drawing & design is the property of NIHVA TECHNOLOGIES. Not to be sold or copied to any other concern.

TITLE: PROPOSED CIVIL PLAN LAYOUT (IN CLIENT SCOPE)	NAME	SIGN	DATE
DRAWN	MAHESH S.		10.10.22
CHECK	MAHESH S.		10.10.22
APPRD.	VIJAY T.		10.10.22

NIHVA TECHNOLOGIES PVT. LTD.

CLIENT - MR. PRANAV	
LOCATION - NOIDA_IN	
PRODUCT - RETRACTABLE ROOF	
If any queries contact : projectsautomation@nihva.com	NIHVA\22-23\02XX REV- 0
ALL DIMENSION ARE IN mm	SCALE: NTS SHEET: 01 OF 01