

230 V & 50 Hz
Single phase supply
Required near left side of Operator.

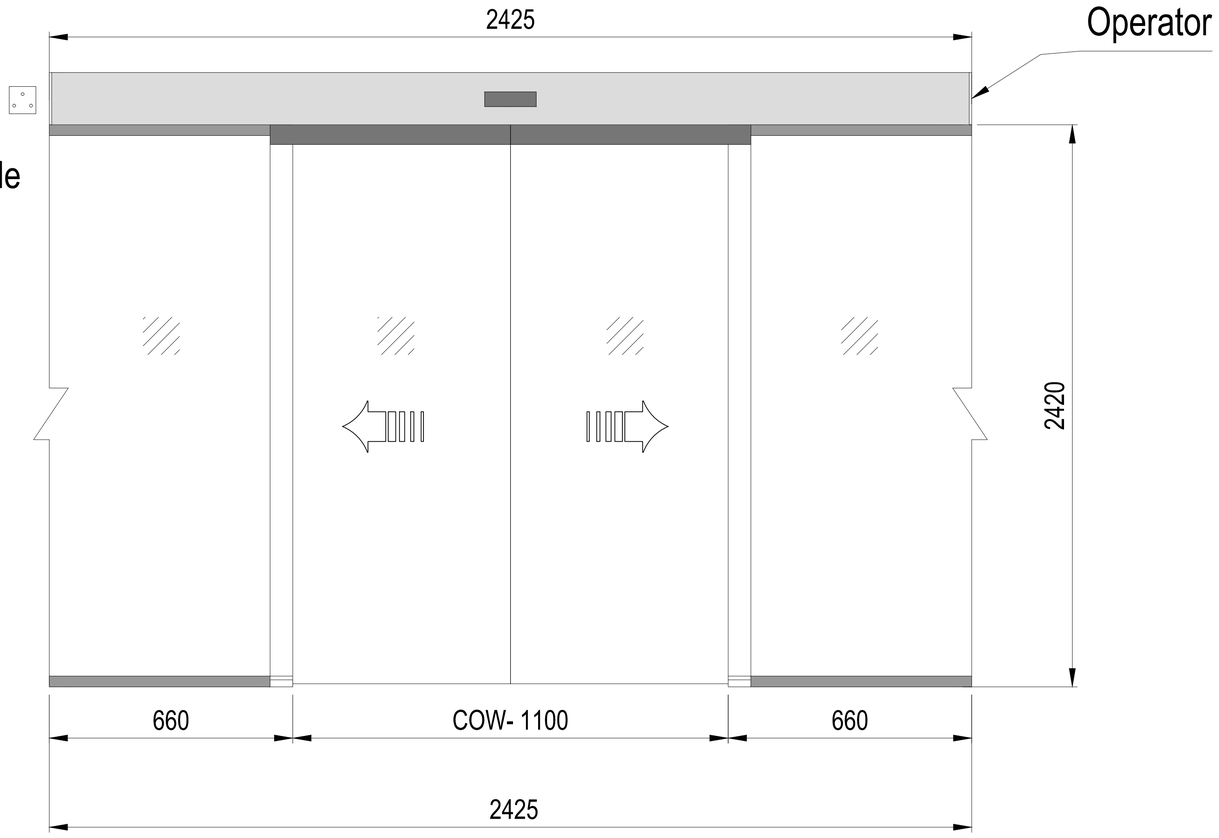

Inside Elevation

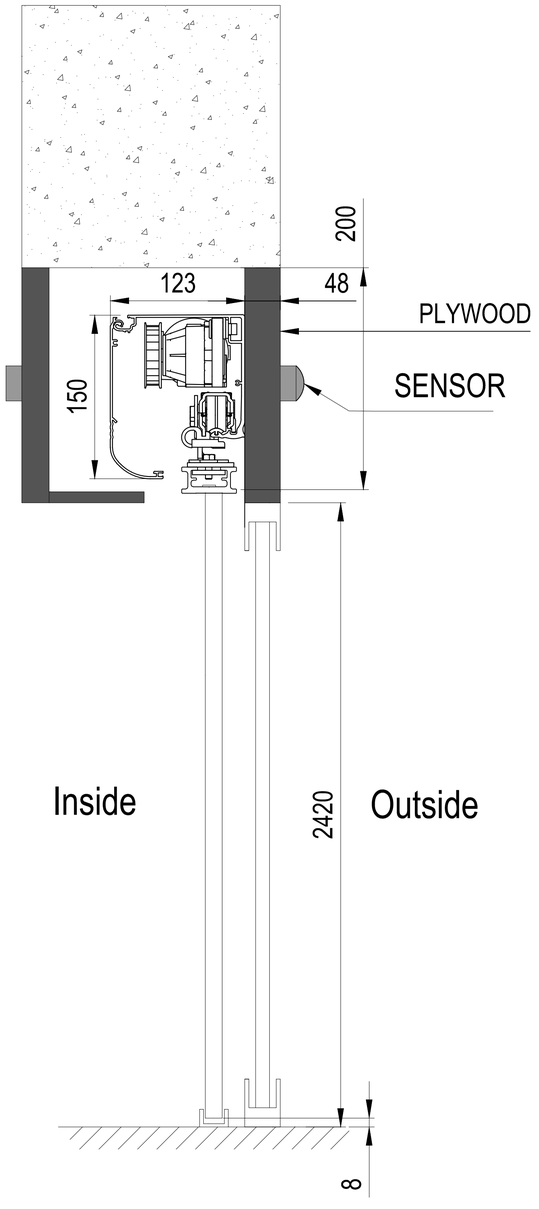

Fixing Plan

Glass Type- 12mm Toughened

Door Size

Sr. No.	Total Width	Clear Width	Clear Height	Quantity
1	2425	1100	2420	1

REV.01-Change in sizes

This drawing & designing is the property of NIHVA TECHNOLOGIES. Not to be sold or copied to any other concern.

TITLE	AUTOMATIC SLIDING GLASS DOOR		NIHVA TECHNOLOGIES PVT. LTD. PUNE Tel : 020 66304033 Email:- info@nihva.com Website:- www.nihva.com
	SIGN	DATE	
DRAWN	SURAJ	07/08/17	CLIENT - VIJAY LOGISTICS
CHECK	SHEKHAR	07/08/17	PROJECT -
REV.	01		SITE - CHAKAN
APPROVAL			DWG. NO. : NIHVA/17-18/0146/R01
If any queries contact : projects@nihva.com			SCALE: NTS | WT: | SHEET: 01 OF 01
ALL DIMENSION ARE IN mm			