

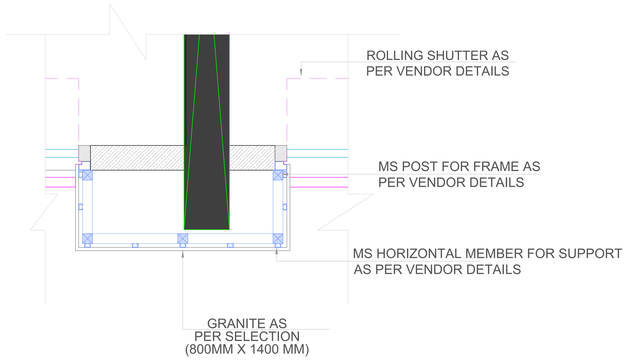


DETAIL AT B

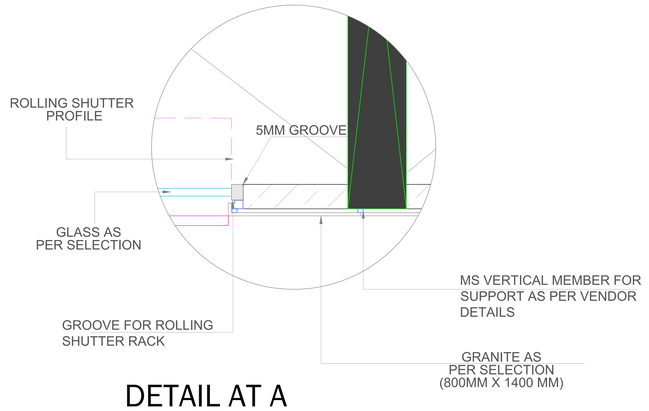

DETAIL AT A


RESIDENTIAL [2B+GR+MEZ+P+21]

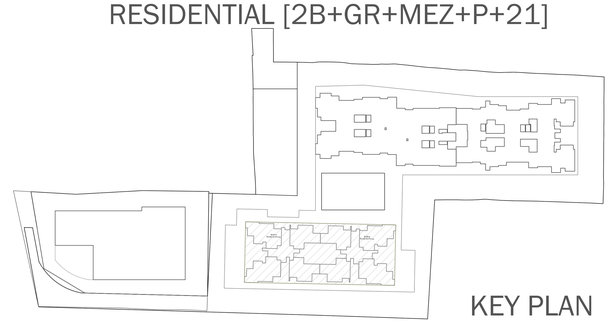


KEY PLAN

SCHEDULE


TYPE	SIZE	SILL	LINTEL	REMARK
RS 1	3000 X 4900	25	4925	
RS 2	2400 X 4900	25	4925	
RS 3	5000 X 4900	25	4925	

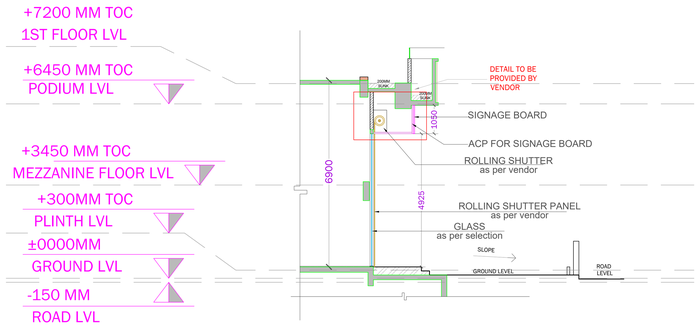


SECTIONAL ELEVATION - AA

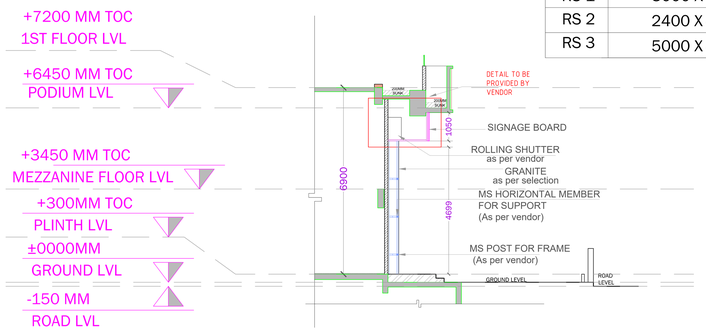

SECTIONAL ELEVATION - BB'

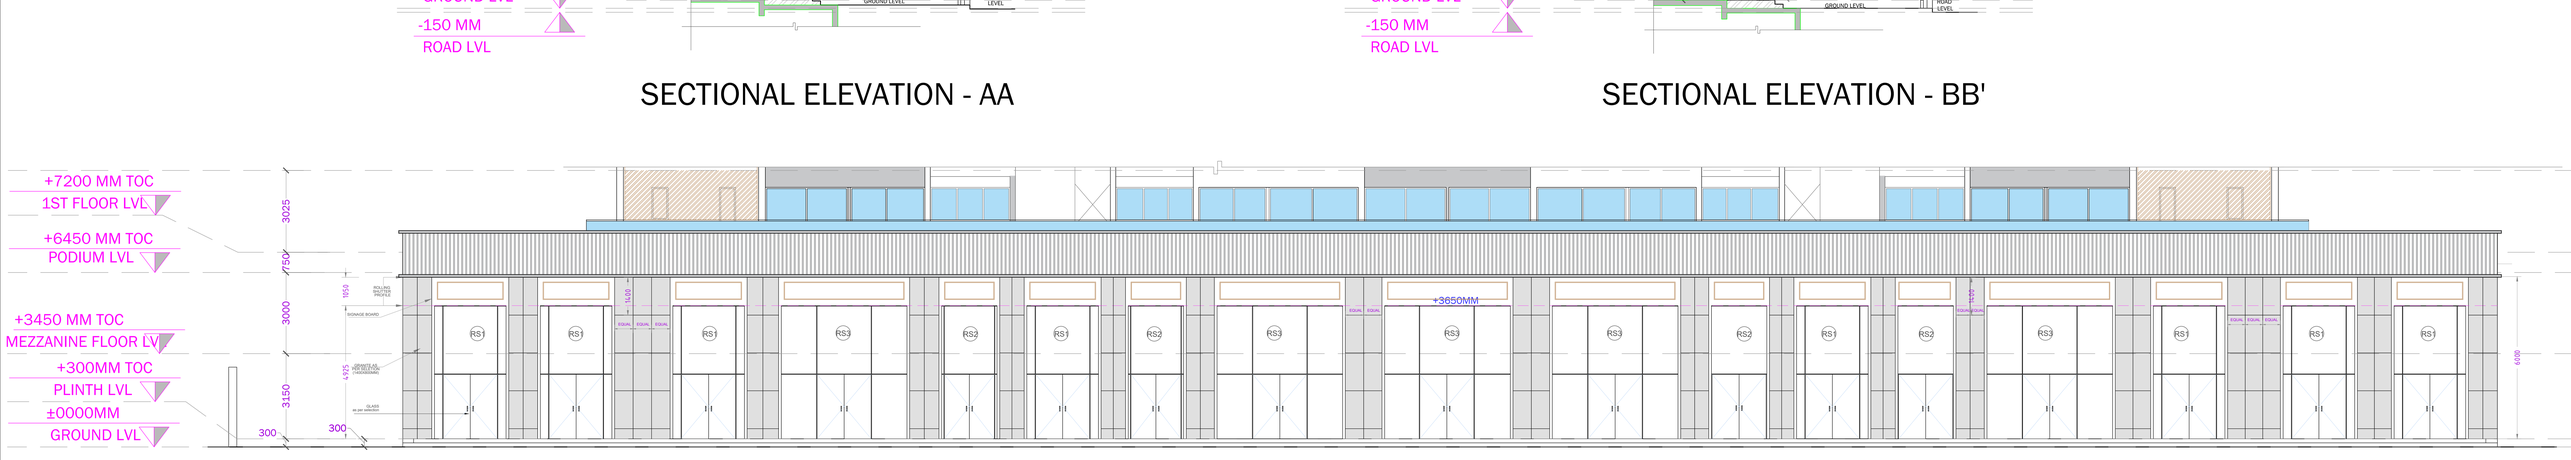

ELEVATION A

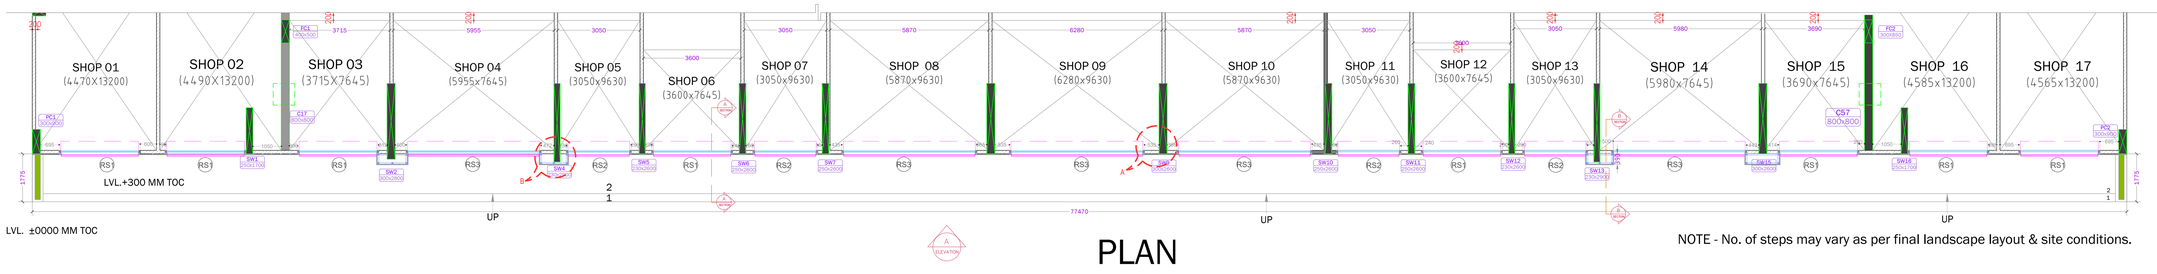

PLAN

NOTE - No. of steps may vary as per final landscape layout & site conditions.

STANDARD DETAILS :

01. WALL DETAIL-REFER LEGEND
02. SUNK DETAIL-REFER LEGEND
03. BEAM DETAIL ALL EXTERNAL & INTERNAL BEAM TO BE READ IN CONJUNCTION WITH STRUCTURAL DRAWING.
04. ALL DIMENSION FROM UNFINISHED TO UNFINISHED SURFACE PROVIDED
05. ALL PARAPET HEIGHTS ARE MIN 1200 MM FROM FINISHED LEVELS.

IMPORTANT DISCLAIMER FOR USE OF THIS DRAWING ON SITE :

01. THIS DRAWING IS A COPYRIGHT OF AMIT BHAT ARCHITECTS AND SHOULD NOT BE RETAINED, COPIED OR USED WITHOUT THEIR AUTHORITY.
02. DO NOT SCALE THE DRAWING.
03. ALL DIMENSIONS ARE IN MILLIMETRES AND LEVELS IN MILLIMETRES. ALL DIMENSIONS TO BE VERIFIED ON SITE AND APPROVED BY THE ENGINEER.
04. THIS DRAWING SHOULD BE READ IN CONJUNCTION WITH OTHER RELEVANT ARCHITECTURAL, STRUCTURAL, MECHANICAL AND ELECTRICAL DRAWINGS AND ALL RELEVANT SECTIONS OF THE SPECIFICATIONS.
05. SITE FORMATION LEVEL TO BE FIXED AS PER FINAL MASTER PLAN
06. PLEASE REFER RCC DRAWING FOR COLUMN SIZE & COLUMN REDUCTION
07. TAKE NOTCH BEAM WHEREVER THERE IS BEAM OFFSET IN THE TOILET
08. ALL AC SLEEVES & SERVICES CUT OUT AS PER MEP CONSULTANTS
09. SITE TEAM SHOULD CHECK THE DIAGONAL DISTANCE FOR EACH SLAB.
10. REFER ELECTRICAL & MEP DRAWINGS FOR CUTOUTS.

R5	18.09.2024	UPDATED AS PER CLIENT'S COMMENTS RECEIVED ON 17.09.2024
R4	------	----------
R3	------	----------
R2	------	----------
R1	------	----------
R0	------	----------

DATE	DRAWN BY	CHECKD BY	APPROVED BY	SCALE
27.08.2024	TANISHKA	----	AMIT BHAT	NTS

JOB NO. 183/ 149/ 08 DWG.NO. AB-D-RS-01

DWG TYPE : SHOPFRONT DETAIL

DWG TITLE : A&B RESIDENTIAL BUILDING

PROJECT NAME :MANTRA INFINITY

OWNER NAME : MANTRA PROPERTIES

PROJECT PROPOSED COMMERCIAL BUILDING ON S. NO. 93/16, CTS NO. 129/16 AT MUNDHWA,PUNE

ARCHITECTS . LANDSCAPE . INTERIORS . M.E.P SERVICES
OFFICE: #601, 6th floor, AnP One, Opp. My world society, Above Kapil's salon, Balewadi high street, Balewadi, Pune - 411045, Email:- info@abarchitects.in, Website:- www.abarchitects.in, Ph. : +91 8657609512 ; + 91 9607087979