

NOTE : ~ PLEASE MAINTAIN 7 MM GAP BETWEEN TWO LIP BUSHES.

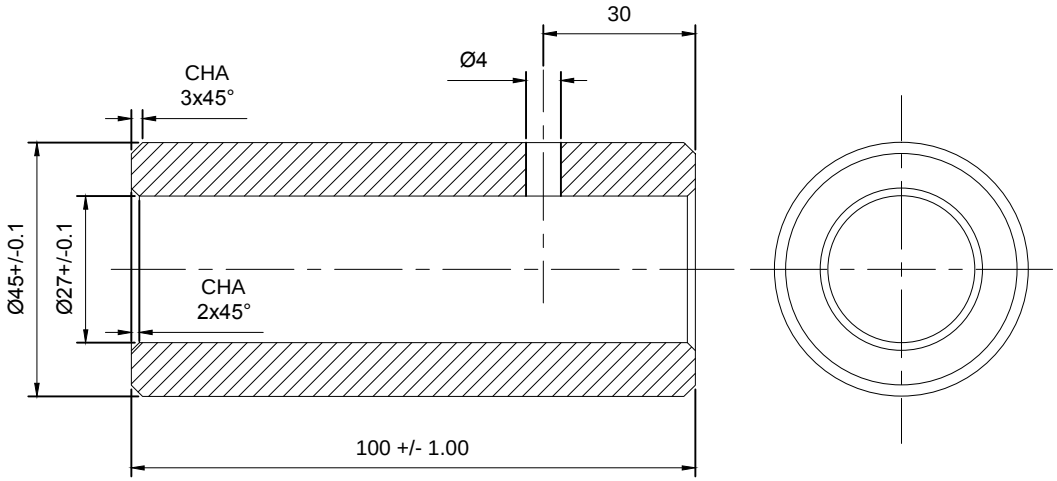

NOTE:~ MTL : MS

BUSH Ø45 X 103L = 100 NOS

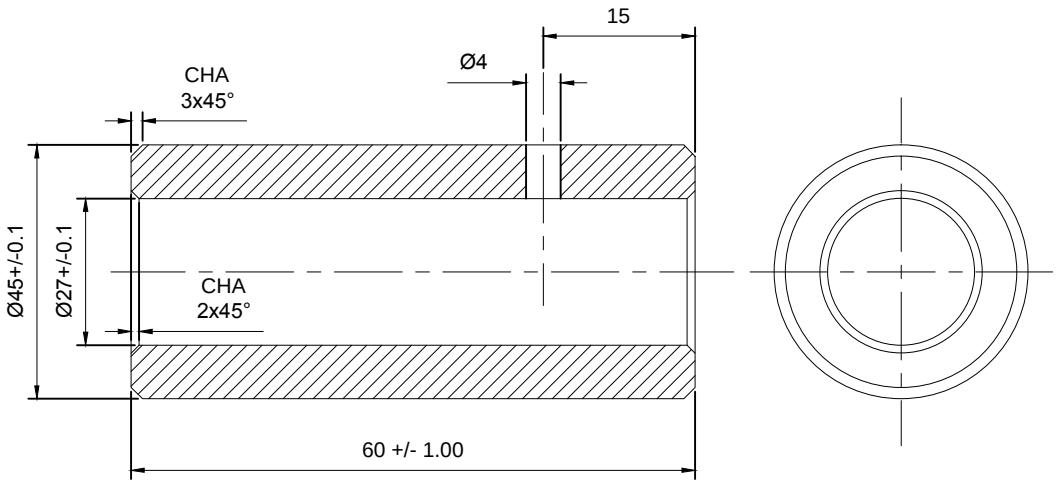

NOTE:~ MTL : MS

BUSH Ø45 X 63L = 120 NOS

REV NO	DATE	DRAWN	REMARK
R01	02.01.19	P.A	1. BUSH QTY & SIZE CHANGE

This drawing & design is the property of NIHVA TECHNOLOGIES. Not to be sold or copied to any other concern.

TITLE

LIP MOUNTING BUSH

NIHVA TECHNOLOGIES PVT. LTD.

NIHVA TECHNOLOGIES PVT. LTD. PUNE
Tel : 020 66304033
Email:- info@nihva.com
Website:- www.nihva.com

	NAME	SIGN	DATE
DRAWN	P.V.A		17.10.2019
CHECK	V.M.T		17.10.2019
APPRD.			

CLIENT -

PROJECT - NDL451

SITE LOCATION -

If any queries contact : design@nihva.com

DWG. NO. : NIHVA/19-20/VDR/183/R01

ALL DIMENSION ARE IN mm

SCALE: NTS | WT: | REV- 0