

Abbrevation's:
WOW-Wall Opening Width
WOH-Wall Opening Height
UC-Under Cut
FFL-Finished Floor Level

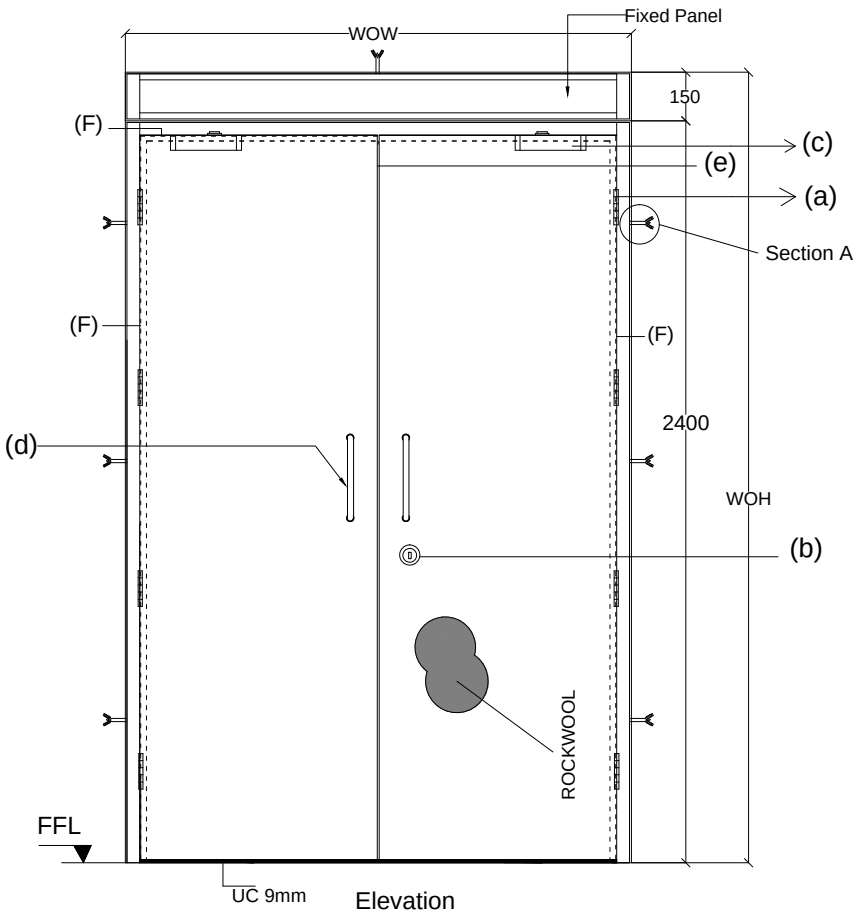

Elevation

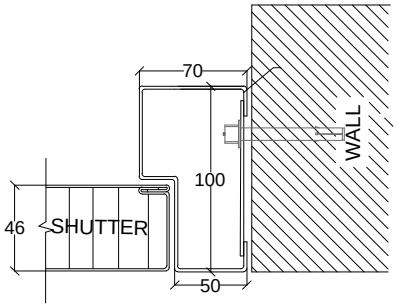

Section A


Top View

ASSESORIES DETALES

(a) HINGES: SS Ball bearing butt hinges 100x75x3mm
3S2BB403030-MS-ASSA ABLOY.

(b) LOCK : Mortise Dead lock-18 P4.50-S-ASSA ABLOY,
Cylinder with one side key & other side turn bolt on Rose
(80MM)SS-80mmTTSN-S-ASSA ABLOY.

(c) DOOR CLOSER: C7722-ASSA ABLOY

(d) HANDLE : 'D' HANDLE (BOTH SIDE) dia 200mmX22mm
YEH-11-200-ASSA ABLOY.

(e) CONCEALED FLUSH BOLT-YFB-011-ASSA ABLOY.

(f) SEAL : RP weather strip closed sponge self adhesive
EPDM bulb seal.

Shutter thickness : 46 mm
Frame Sheet thick : 1.5mm
Shutter sheet thick : 1.2mm
Fixing : On Solid Brick plastered wall with Anchors

NOTE:- *All Dimensions are in mm.
*Tolerance:-All Linear Dimensions ±3mm,Others ±0.5mm.
*The Drawing Is For Location of Hardware only. Drawing Does Not Represent The Hardware For More Clarity, Please Go Through Hardware Broucher.

COLOR
1.TRAFFIC WHITE (RAL 9016)

Steel door size

WOW	WOH	TYPE 5	TYPE 6	TYPE 7	TYPE 8	QUANTITY
2040mm	2550mm				1	01NOS

This drawing & designing is the property of NIHVA TECHNOLOGIES. Not be sold or copy to any other concern.

TITLE: FIRE DOOR (DOUBLE LEAF)

	NAME	SIGN.	DATE
DRAWN	SURAJ		22/02/18
CHECK	OMKAR		22/02/18
APPRD.	SHEKHAR		22/02/18

NIHVA TECHNOLOGIES PVT. LTD.
NIHVA TECHNOLOGY PVT. LTD. PUNE
Tel : 020 66304033
Email:- info@nihva.com
Website:-www.nihva.com

CLIENT -
PROJECT -
SITE -
If any queries contact: design@nihva.com
DWG. NO. - NIHVA/17-18/VDR/0237
REV. :-0
ALL DIMENSION ARE IN mm
SCALE: NTS
WT:
SHEET: 01 OF 01