

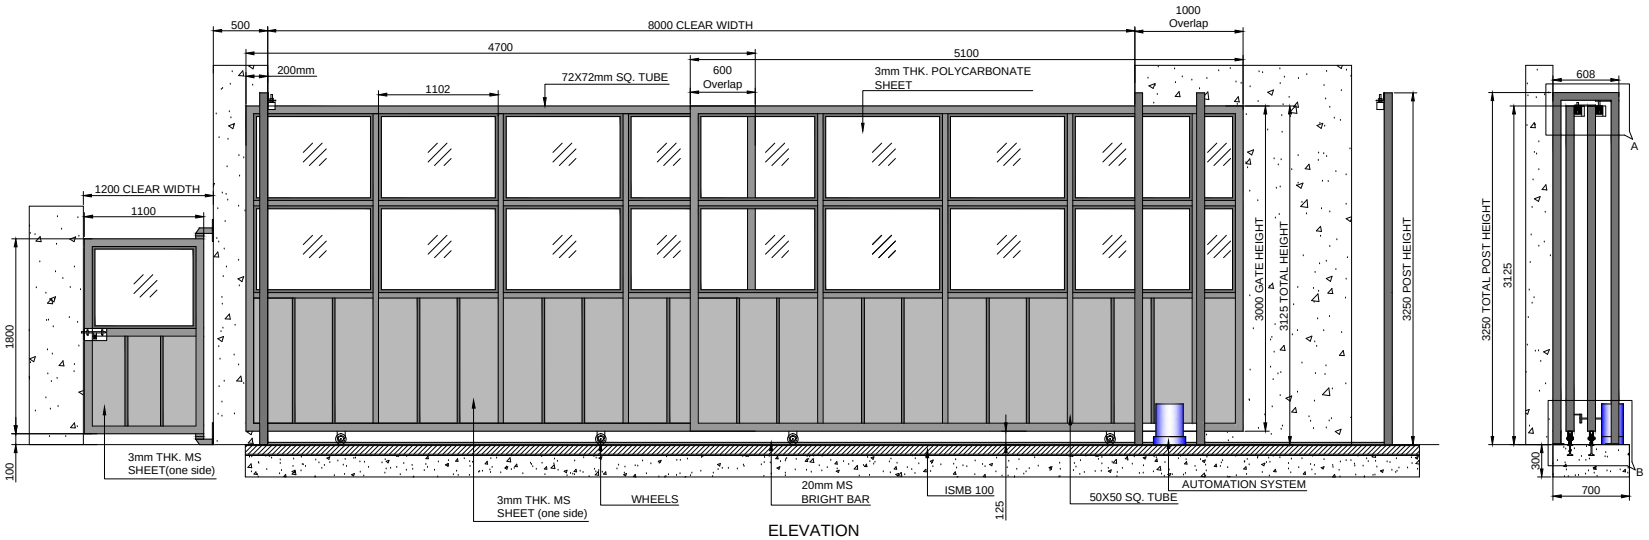



ELEVATION

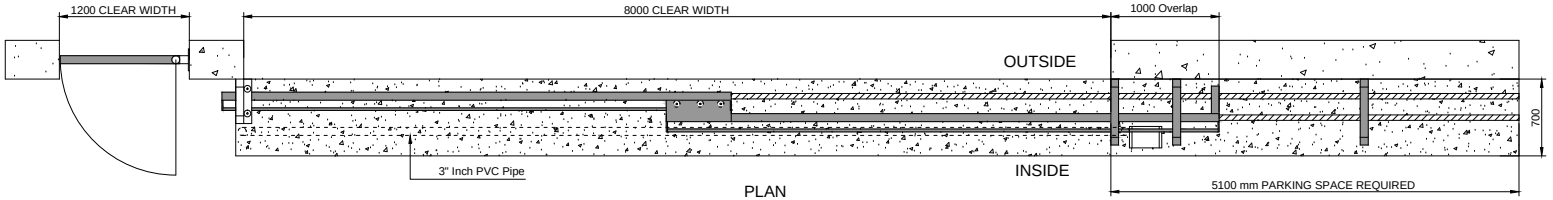


PLAN

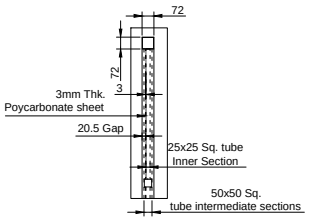

Gate leaf section details

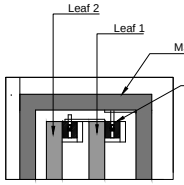

Detailed View of A

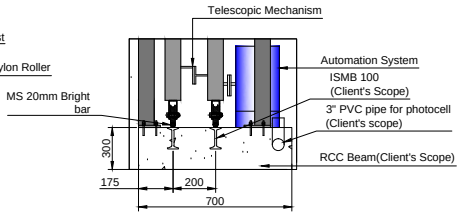

Detailed View of B

DIMENSION :

CLEAR WIDTH	CLEAR HEIGHT	QUANTITY
8000 mm	3000 mm	1 NOS.

MATERIAL : MS

THICKNESS :

MATERIAL SPECIFICATION

SR NO	TUBE SIZE	
1	MS TUBE 72X72X3.2mm	OUTER TUBE
2	MS TUBE 50X50X2.6mm	INTERMEDIATE TUBE
3	MS TUBE 25X25X2mm	INNER TUBE
4	3mm MS SHEET	AT LOWER SIDE
5	3mm THK. POLYCARBONATE SHEET (TRANSPARENT)	AT UPPER SIDE

NOTE: ALL REQUIRED CIVIL WORK WILL BE IN CLIENT'S SCOPE.
ONE COAT RED OXIDE PRIMER WILL BE GIVEN TO THE STRUCTURE OF GATE.
TWO COATS OF FINAL APPROVED RAL SHADE WILL BE GIVEN TO THE CLIENT.
ISMB 100 WILL BE CLIENTS SCOPE.

NIHVA
NIHVA TECHNOLOGIES PVT. LTD.
NIHVA TECHNOLOGY PVT. LTD. PUNE
Email:- info@nihva.com
Website:- www.nihva.com

TITLE:

TWO LEAF TELESCOPIC SLIDING GATE 8X3m

CLIENT'S APPROVAL :

CLIENT - WILO MATHER & PLATT PUMPS PVT. LTD.

PROJECT -

SITE LOCATION - AKURDI

DWG. NO. : NIHVA/17-18/0360		REV- 0
SCALE: NTS	WT:	SHEET:1 OF 1

DRAWN BY: OMKAR	DATE: 12-02-2018
CHECK : SHEKHAR	DATE: 12-02-2018
APPROVED : SHEKHAR	DATE: 12-02-2018

If any queries contact : design@nihva.com

NOTE: ALL DIMENSION ARE IN mm

THIS DRAWING & DESIGNING IS THE PROPERTY OF NIHVA TECHNOLOGIES. NOT BE SOLD OR COPY TO ANY OTHER CONCERN.