

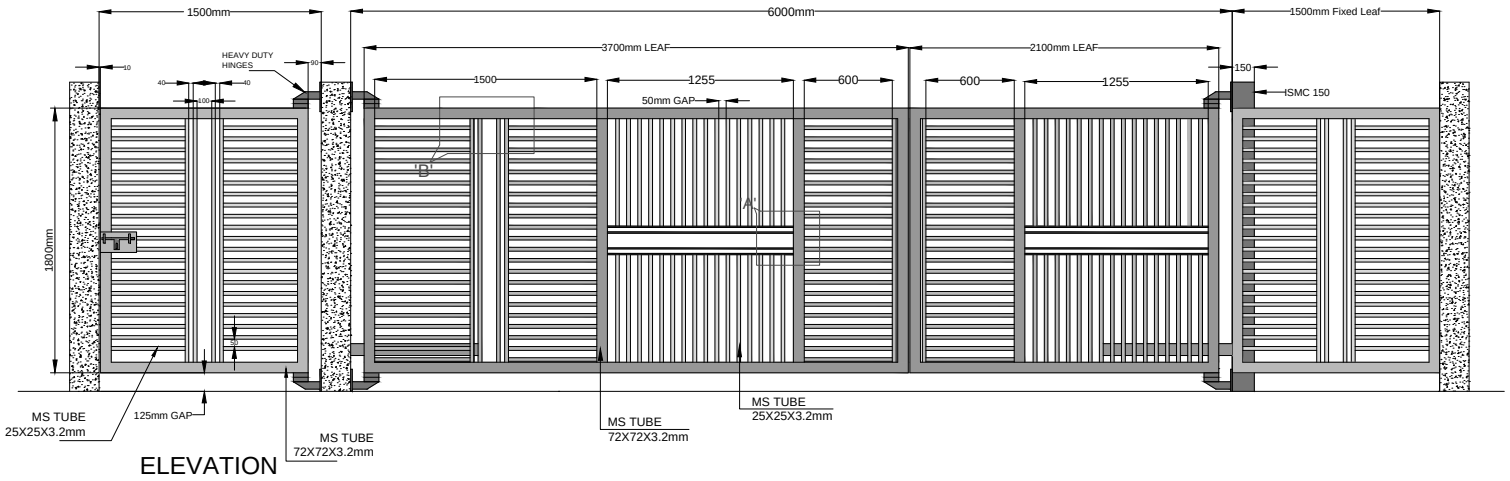



ELEVATION

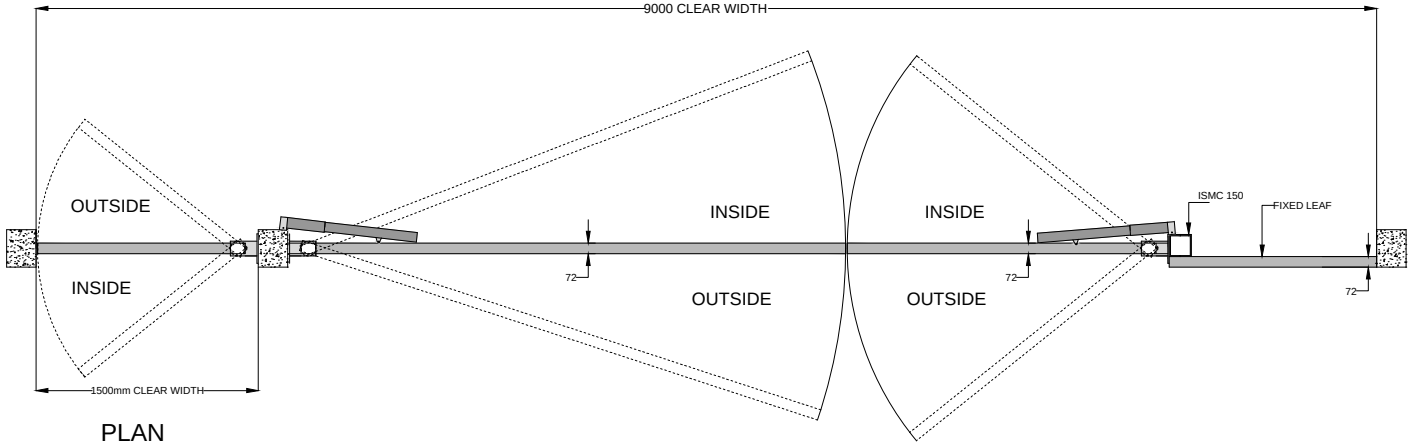

PLAN

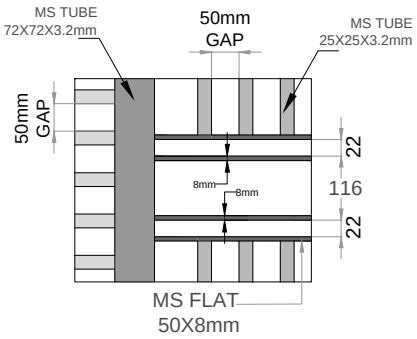

DETAIL VIEW OF 'A'.

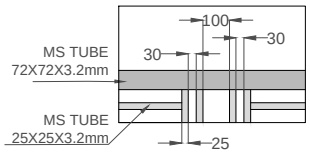

DETAIL VIEW 'B'

SR NO	CLEAR WIDTH	CLEAR HEIGHT	QTY.
1	9000mm	1800mm	01 NOS

REV:– FIXED LEAF POSITION HAS BEEN CHANGED AS PER SITE CONDITION.

This drawing & design is the property of NIHVA TECHNOLOGIES. Not to be sold or copied to any other concern.

TITLE

AUTOMATIC SWING GATE

NIHVA TECHNOLOGIES PVT. LTD.

NIHVA TECHNOLOGIES PVT. LTD. PUNE
Tel : 020 66304033
Email:- info@nihva.com
Website:- www.nihva.com

	NAME	SIGN	DATE
DRAWN	SURAJ		12-05-2018
CHECK	OMKAR		12-05-2018
APPRD.	PRADEEP		12-05-2018

CLIENT - JLL

PROJECT -STANDLEE

SITE LOCATION - CHAKAN.

If any queries contact : design@nihva.com

DWG. NO. : NIHVA/18-19/0035/01 REV- 01

ALL DIMENSION ARE IN mm

SCALE: NTS WT: SHEET: 01 OF 01