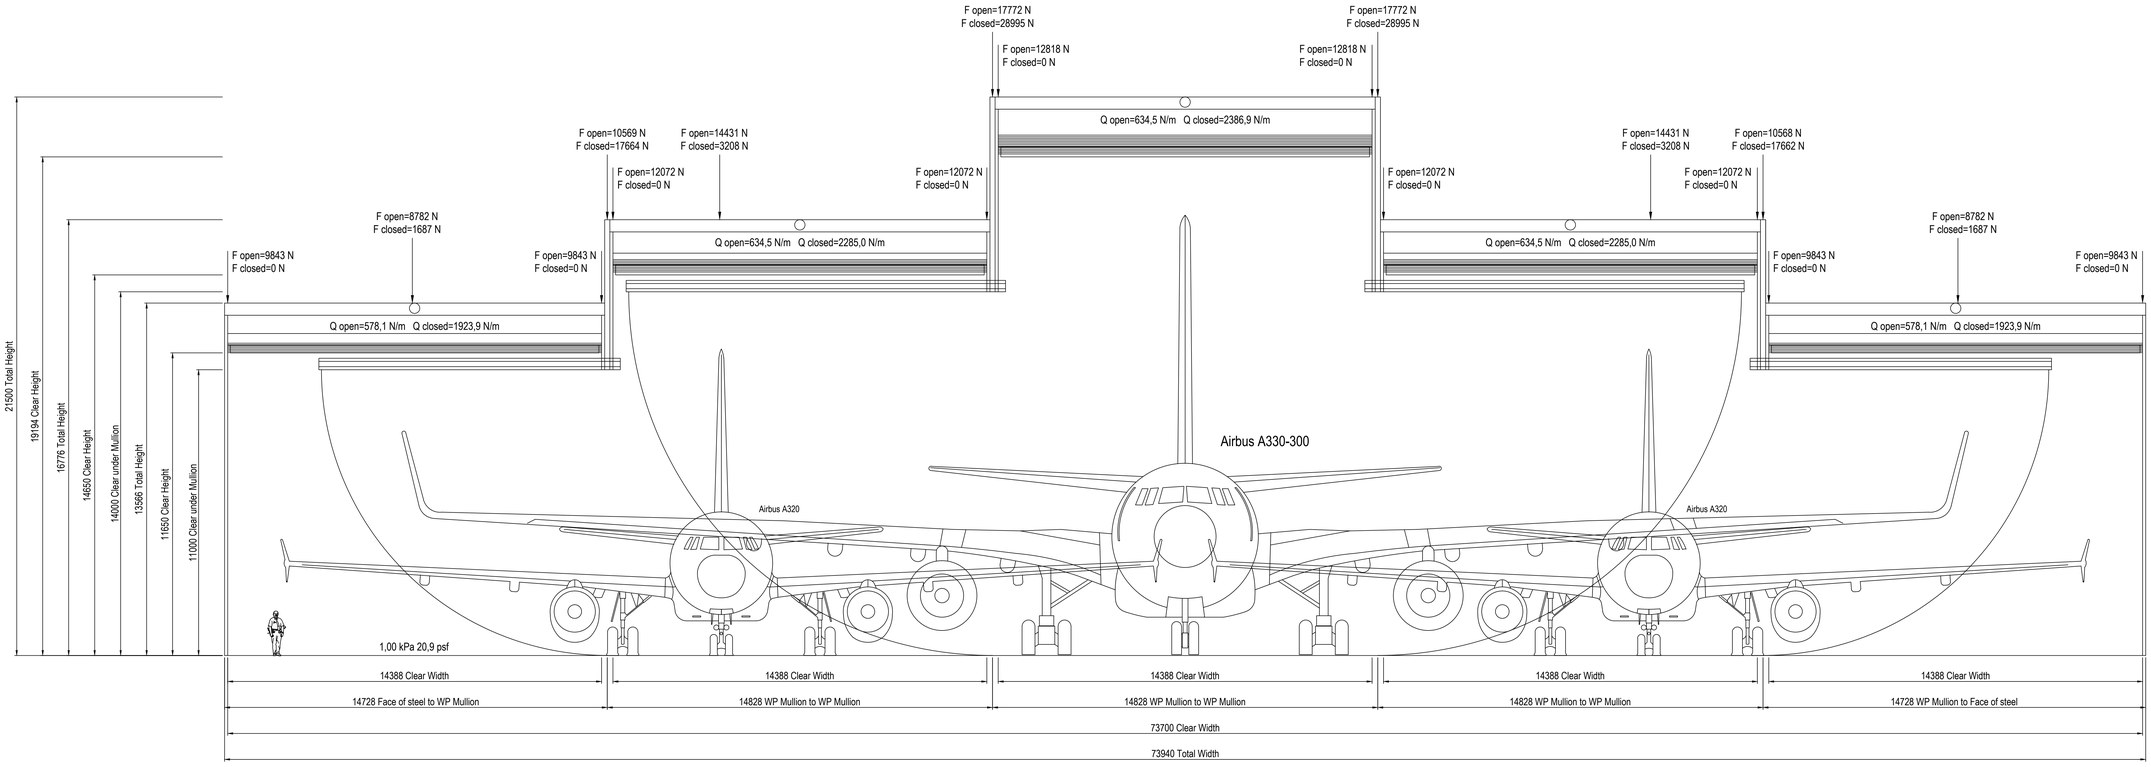


Quotation only. Do not use for design.
Nominal static vertical loads are indicated.
A dynamic surload factor of 1.25 should be added to door leaf loads in open position.
Includes items provided by ASSA ABLOY Entrance Systems only.
Total weight: 26257 kg
Total static weight: 26003 kg
Total motor power: 35,7 kW
Total rated current: 74,7 A
Total peak current: 79,6 A
Power supply: 400V/50Hz/3ph
(max. allowed voltage drop at start: 5%)
Control system: 24V
Mains power to control panel supplied by others than ASSA ABLOY Entrance Systems.

Contact Information

Henk v.d. Heijden
Project Manager
MEGADOOR/
ASSA ABLOY Entrance Systems
Servicegatan 6
P.O. Box 383
SE-931 24 Skellefteå
SWEDEN
Direct: +31 (0)65 323 61 77
Switchboard: +46 (0)10 47 47 190
E-mail: henk.van.der.heijden@assaabloy.com
www.megadoor.com

ASSA ABLOY

SALES REP. Ashish Nair	DATE ISSUED 27-6-2019
SALES No. 219-251	DATE DRAWN 27-6-2019
SCALE N.T.S.	
DRAWING No. 219-251	REVISION

Air India Retrofit
Kolkata
India

Load diagram