


HIGH SPEED DOOR STRUCTURE = 2 NOS

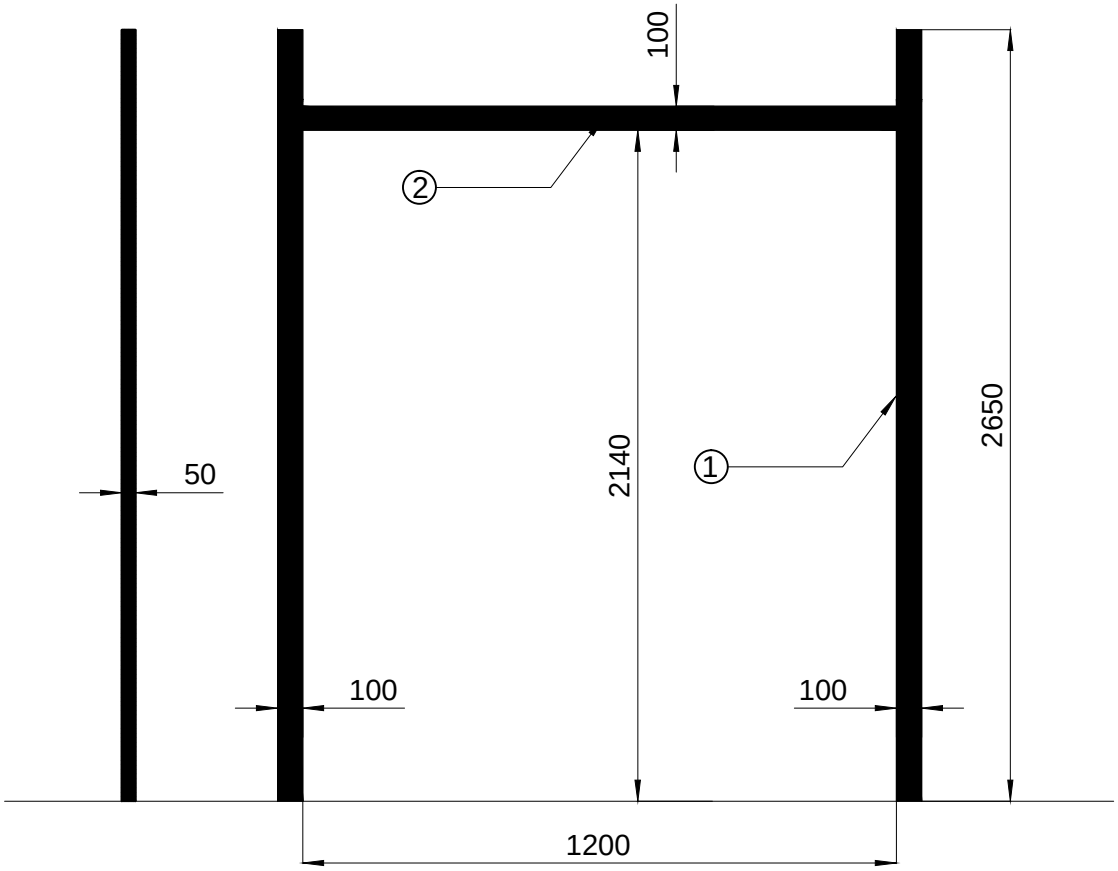

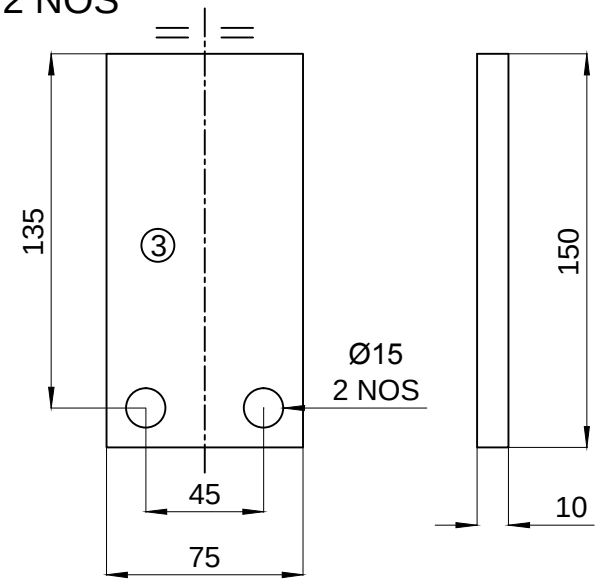

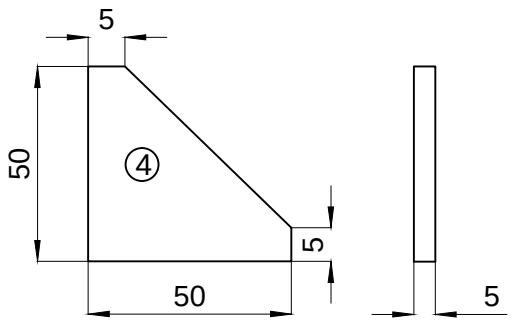

Tolerance ±3 mm (for all dimensions)

SR NO	DESCRIPTION	SPECIFICATION	QTY
4	RIB	50 X 5 X 50L	4 NOS
3	FLAT	75 X 10 X 150L	4 NOS
2	R.TUBE	96 X 48 X 4.8 THK X 1200L	1 NO
1	R.TUBE	96 X 48 X 4.8 THK X 2650L	2 NOS

This drawing & design is the property of NIHVA TECHNOLOGIES. Not to be sold or copied to any other concern.

TITLE	HIGH SPEED DOOR STRUCTURE		
	NAME	SIGN	DATE
DRAWN	P.A		21.11.19
CHECK	G.J		21.11.19
APPV'ED			

NIHVA TECHNOLOGIES PVT. LTD.
NIHVA TECHNOLOGIES PVT. LTD. PUNE
Tel : 020 66304033
Email:- info@nihva.com
Website:- www.nihva.com

CLIENT :-
PROJECT :-
LOCATION :-
If any queries contact : design@nihva.com
DWG. NO. :- NIHVA/19-20/VDR/228
REV.:- R00
ALL DIMENSION ARE IN mm
SCALE: NTS
WT:
SHEET: 01 OF 01