

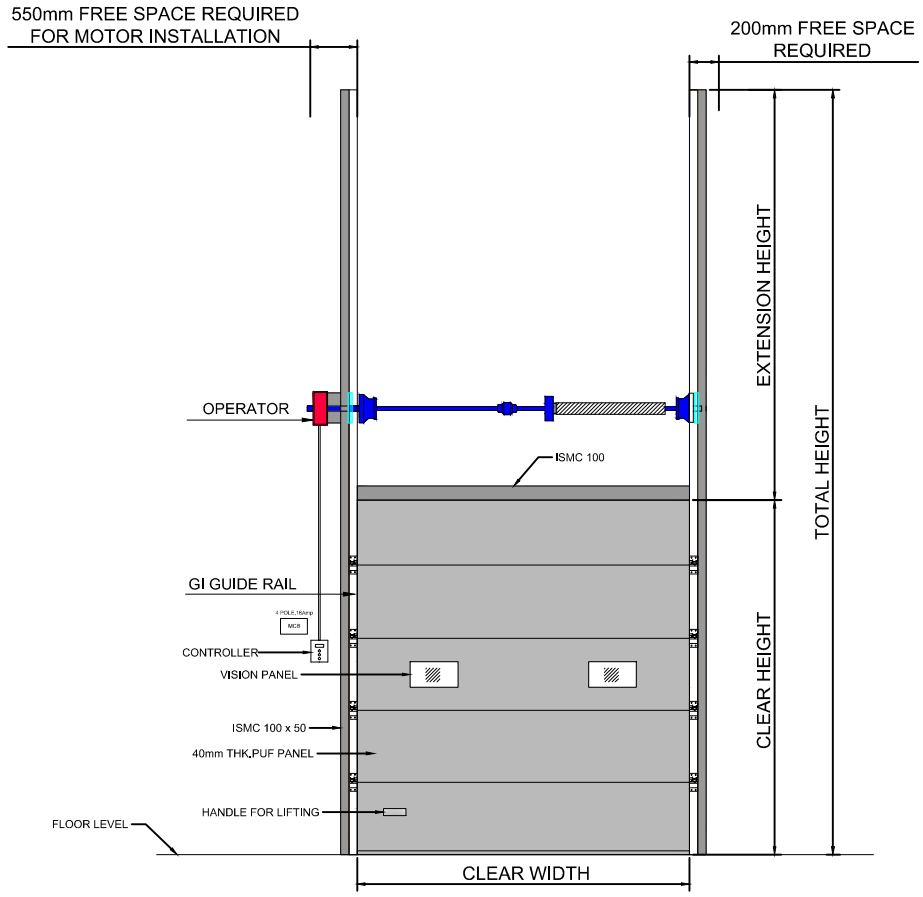


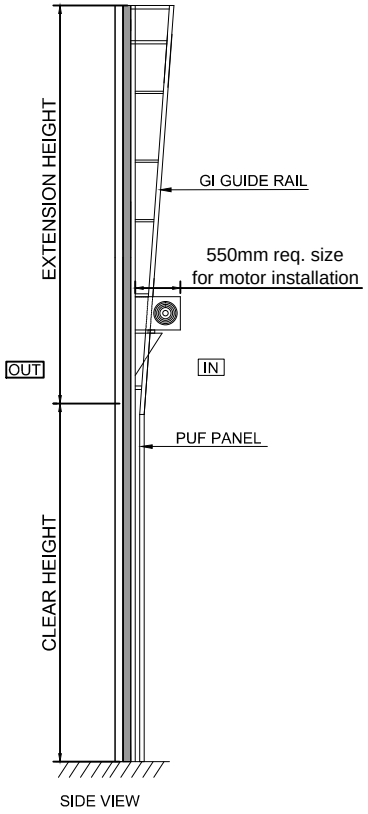

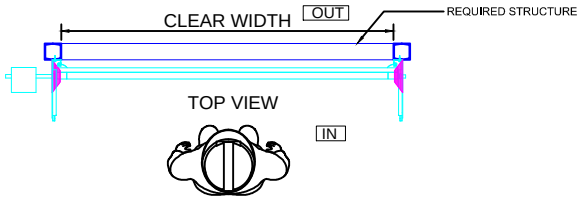

SR NO	CLEAR WIDTH	CLEAR HEIGHT	QTY	TOTAL HEIGHT	EXTENSION HEIGHT
01	2400mm	3000mm	3	6300	3300

NOTE : REQ. M.S STRUCTURE FOR DOOR INSTALLATION WILL BE IN CLIENT SCOPE.

TOLERANCE: 10mm

This drawing & design is the property of NIHVA TECHNOLOGIES. Not to be sold or copied to any other concern.

TITLE: SECTIONAL DOOR (VL)

NIHVA TECHNOLOGIES PVT. LTD. PUNE
Tel : 020 66304033
Email:- info@nihva.com
Website:- www.nihva.com

	NAME	SIGN	DATE
DRAWN	P.A		25.06.20
CHECK	G.J		25.06.20
APPROVAL			

CLIENT - RMK INFRASTRUCTURE
PROJECT -
SITE -
If any queries contact : design@nihva.com
DWG. NO. : NIHVA/20-21/0026
REV: 0
ALL DIMENSION ARE IN mm
SCALE: NTS
WT:
SHEET: 01 OF 01