🟩 marked green hatch required
cantiliver slab

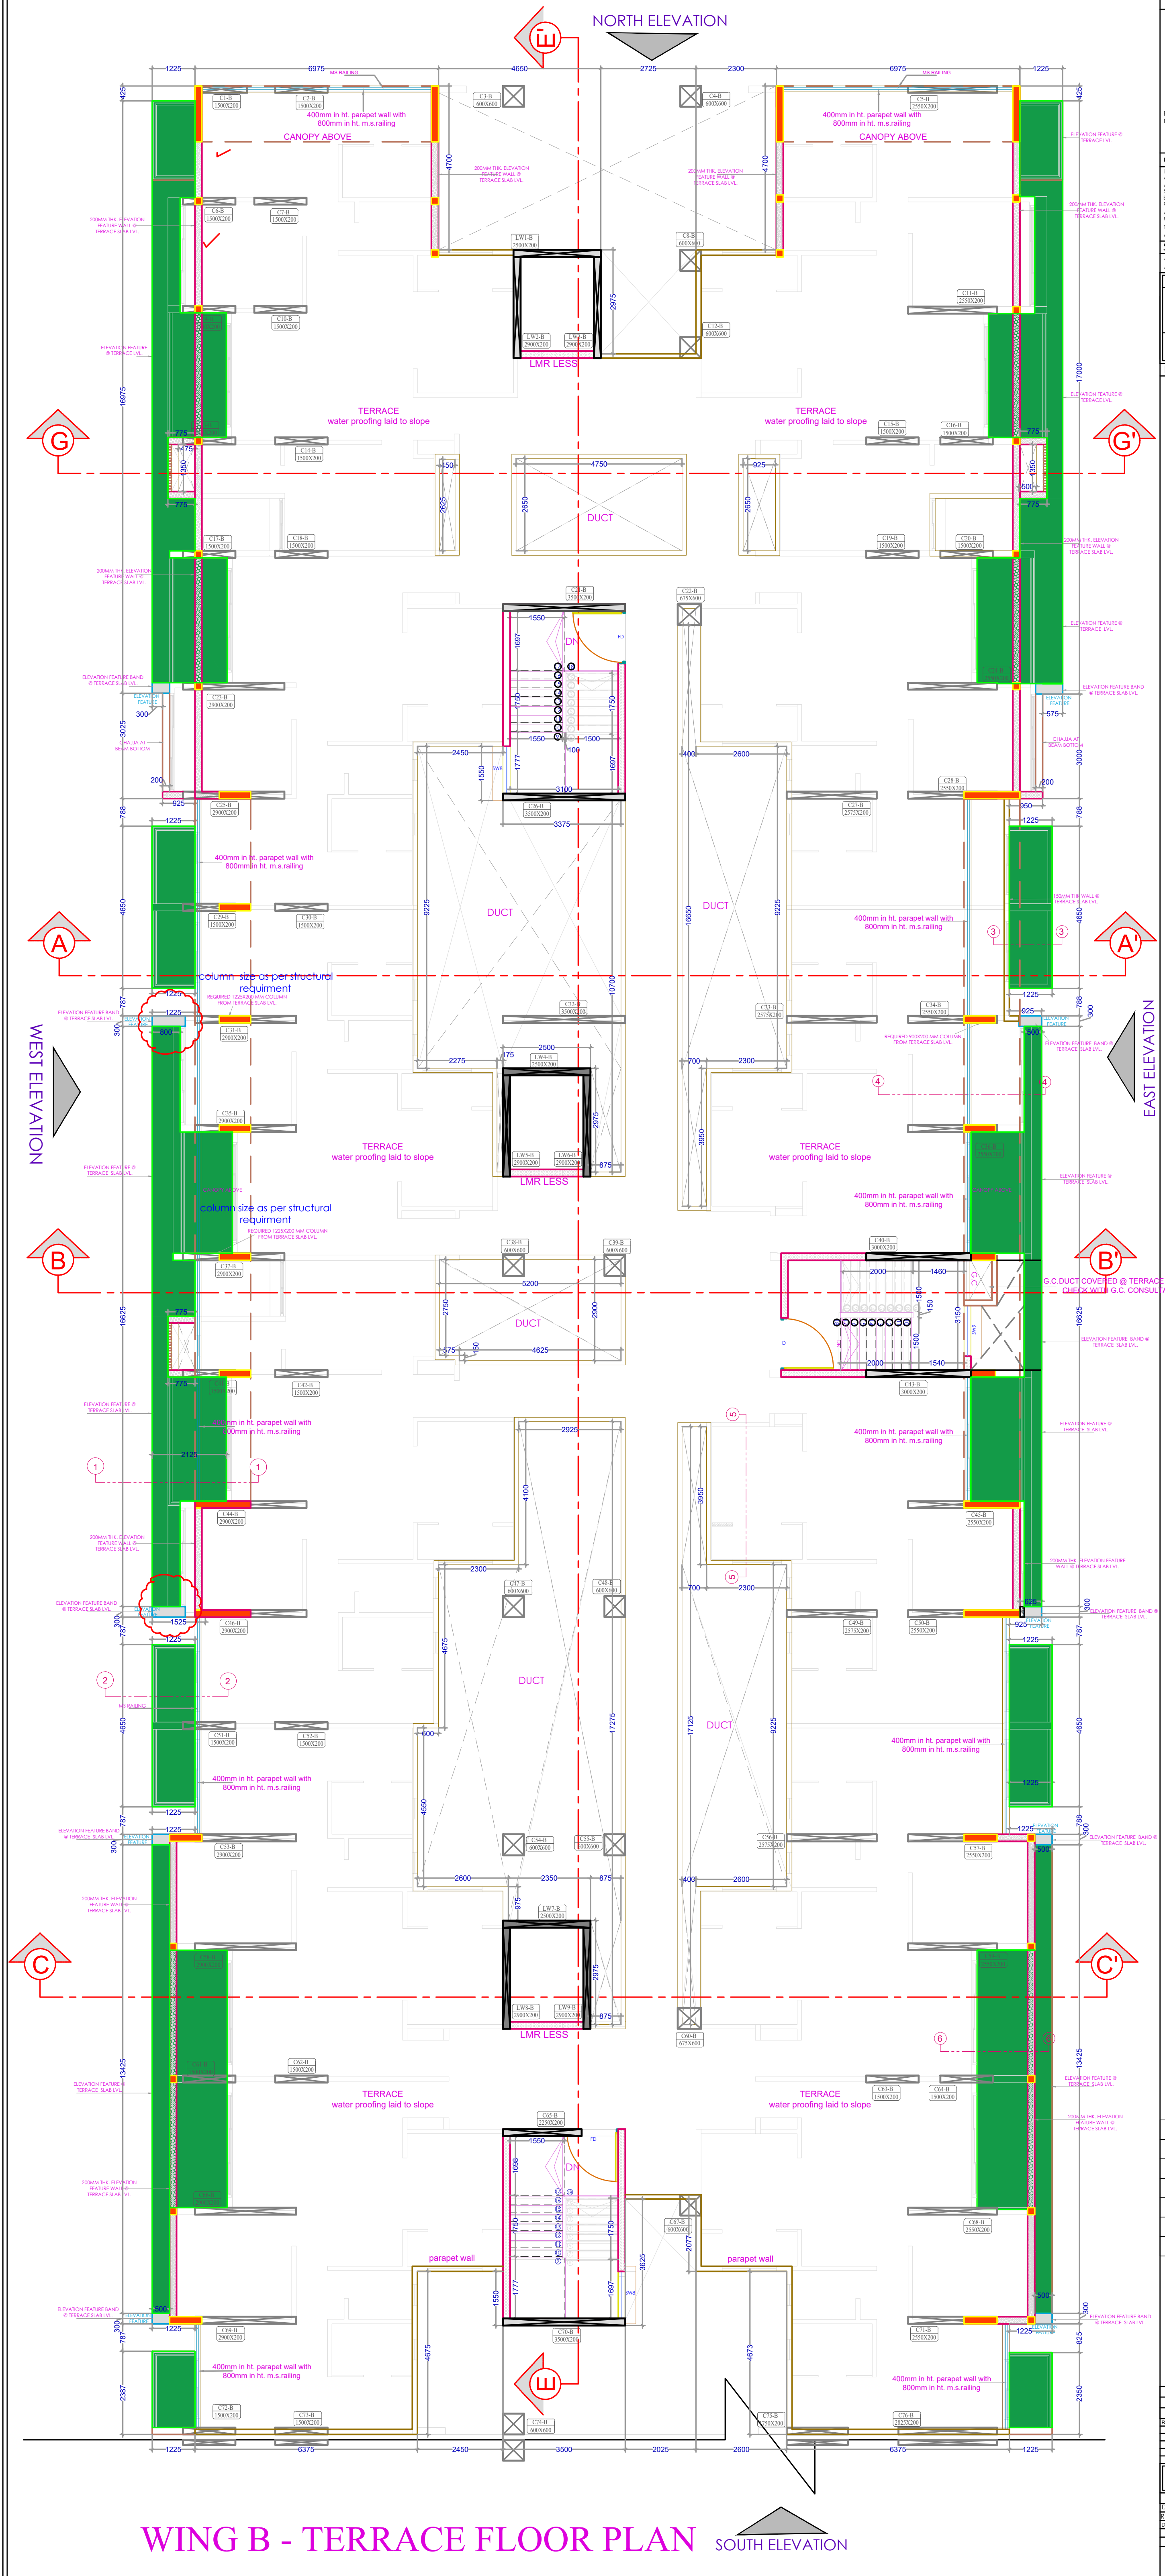
NORTH ELEVATION
SOUTH ELEVATION
WEST ELEVATION
EAST ELEVATION
G
G'
A
A'
B
B'
C
C'
E
MS RAILING
400mm in ht. parapet wall with 800mm in ht. m.s.railing
CANOPY ABOVE
200MM THK. ELEVATION FEATURE WALL @ TERRACE SLAB LVL.
ELEVATION FEATURE @ TERRACE LVL.
ELEVATION FEATURE BAND @ TERRACE SLAB LVL.
LMR LESS
TERRACE
water proofing laid to slope
DUCT
column size as per structural requirement
G.C.DUCT COVERED @ TERRACE LVL. CHECK WITH G.C. CONSULTANT
parapet wall
C1-B 1500X200
C2-B 1500X200
C3-B 600X600
1225
6975
4650
2725
16975

WING B - TERRACE FLOOR PLAN

ARCHITECT

LANDMARK DESIGN GROUP

PLOT NO 32, SECTOR NO 29, ISKCON TEMPLE ROAD
NEAR PCMC WATER TANK, RAVET, PRADHIKARAN, PUNE
E-MAIL-landmarkdg@gmail.com PH NO 9763033222
www.landmarkdesigngroup.in

GENERAL NOTES:

THIS DRAWING IS SOLE PROPERTY OF LANDMARK DESIGN GROUP AND IS NOT TO BE COPIED OR USED WITHOUT PRIOR PERMISSION.

ALL DIMENSIONS SHALL BE CO-RELATED WITH STRUCTURAL AND SERVICE DRAWINGS AND ANY AMBIGUITY SHALL BE IMMEDIATELLY BROUGHT TO THE NOTICE OF THE ARCHITECTS BEFORE THE COMMENCEMENT OF WORK

ALL DIMENSIONS IN THE DRAWING ARE TO BE READ AND NOT TO BE MEASURED.

THIS DRAWING SHALL SUPERSEDE ITS PREVIOUS REVISIONS.

ALL DIMENSIONS ARE IN MILLIMETERS UNLESS SPECIFIED OTHERWISE.

SPECIFIC NOTES

ALL LEVELS IN THIS DRAWING ARE UNFINISHED FLOOR LEVELS.

ALL DIMENSIONS IN THIS DRAWING ARE FROM UNFINISHED SURFACES.

PROJECT :

PROPOSED RESIDENTIAL BUILDING
YASHADA VIVANTA REALITY
AT- RAVET, PUNE

OWNER :

NOTES

100 MM THK WALL	▨
125 MM THK WALL	▨
150 MM THK WALL	▨
200 MM THK WALL	▨
300 MM THK WALL (ELEVATION)	▨
200 MM SUNK	▨
150 MM SUNK	▨

DRAWING RELEASED

☐ FOR DISCUSSION ☐ FOR PRELIMINARY
☐ FOR TENDER ☑ FOR EXECUTION

REVISION	REVISION DATE	DISCRIPTION
R1	21.12.2023	CHANGES SA PER ELEVATION FEATURE WALL AT TERRACE SLAB LVL.

DRAWING NAME: TERRACE FLOOR PLAN

DATE :	27.11.2023	JOB. NO.	_
REV DATE:	21.12.2023	REV NO:	R1
DRAWN BY :	AKSHAY	CHECKED :	TUSHAR
		SCALE :	N.T.S.

N

SEAL & SIGN

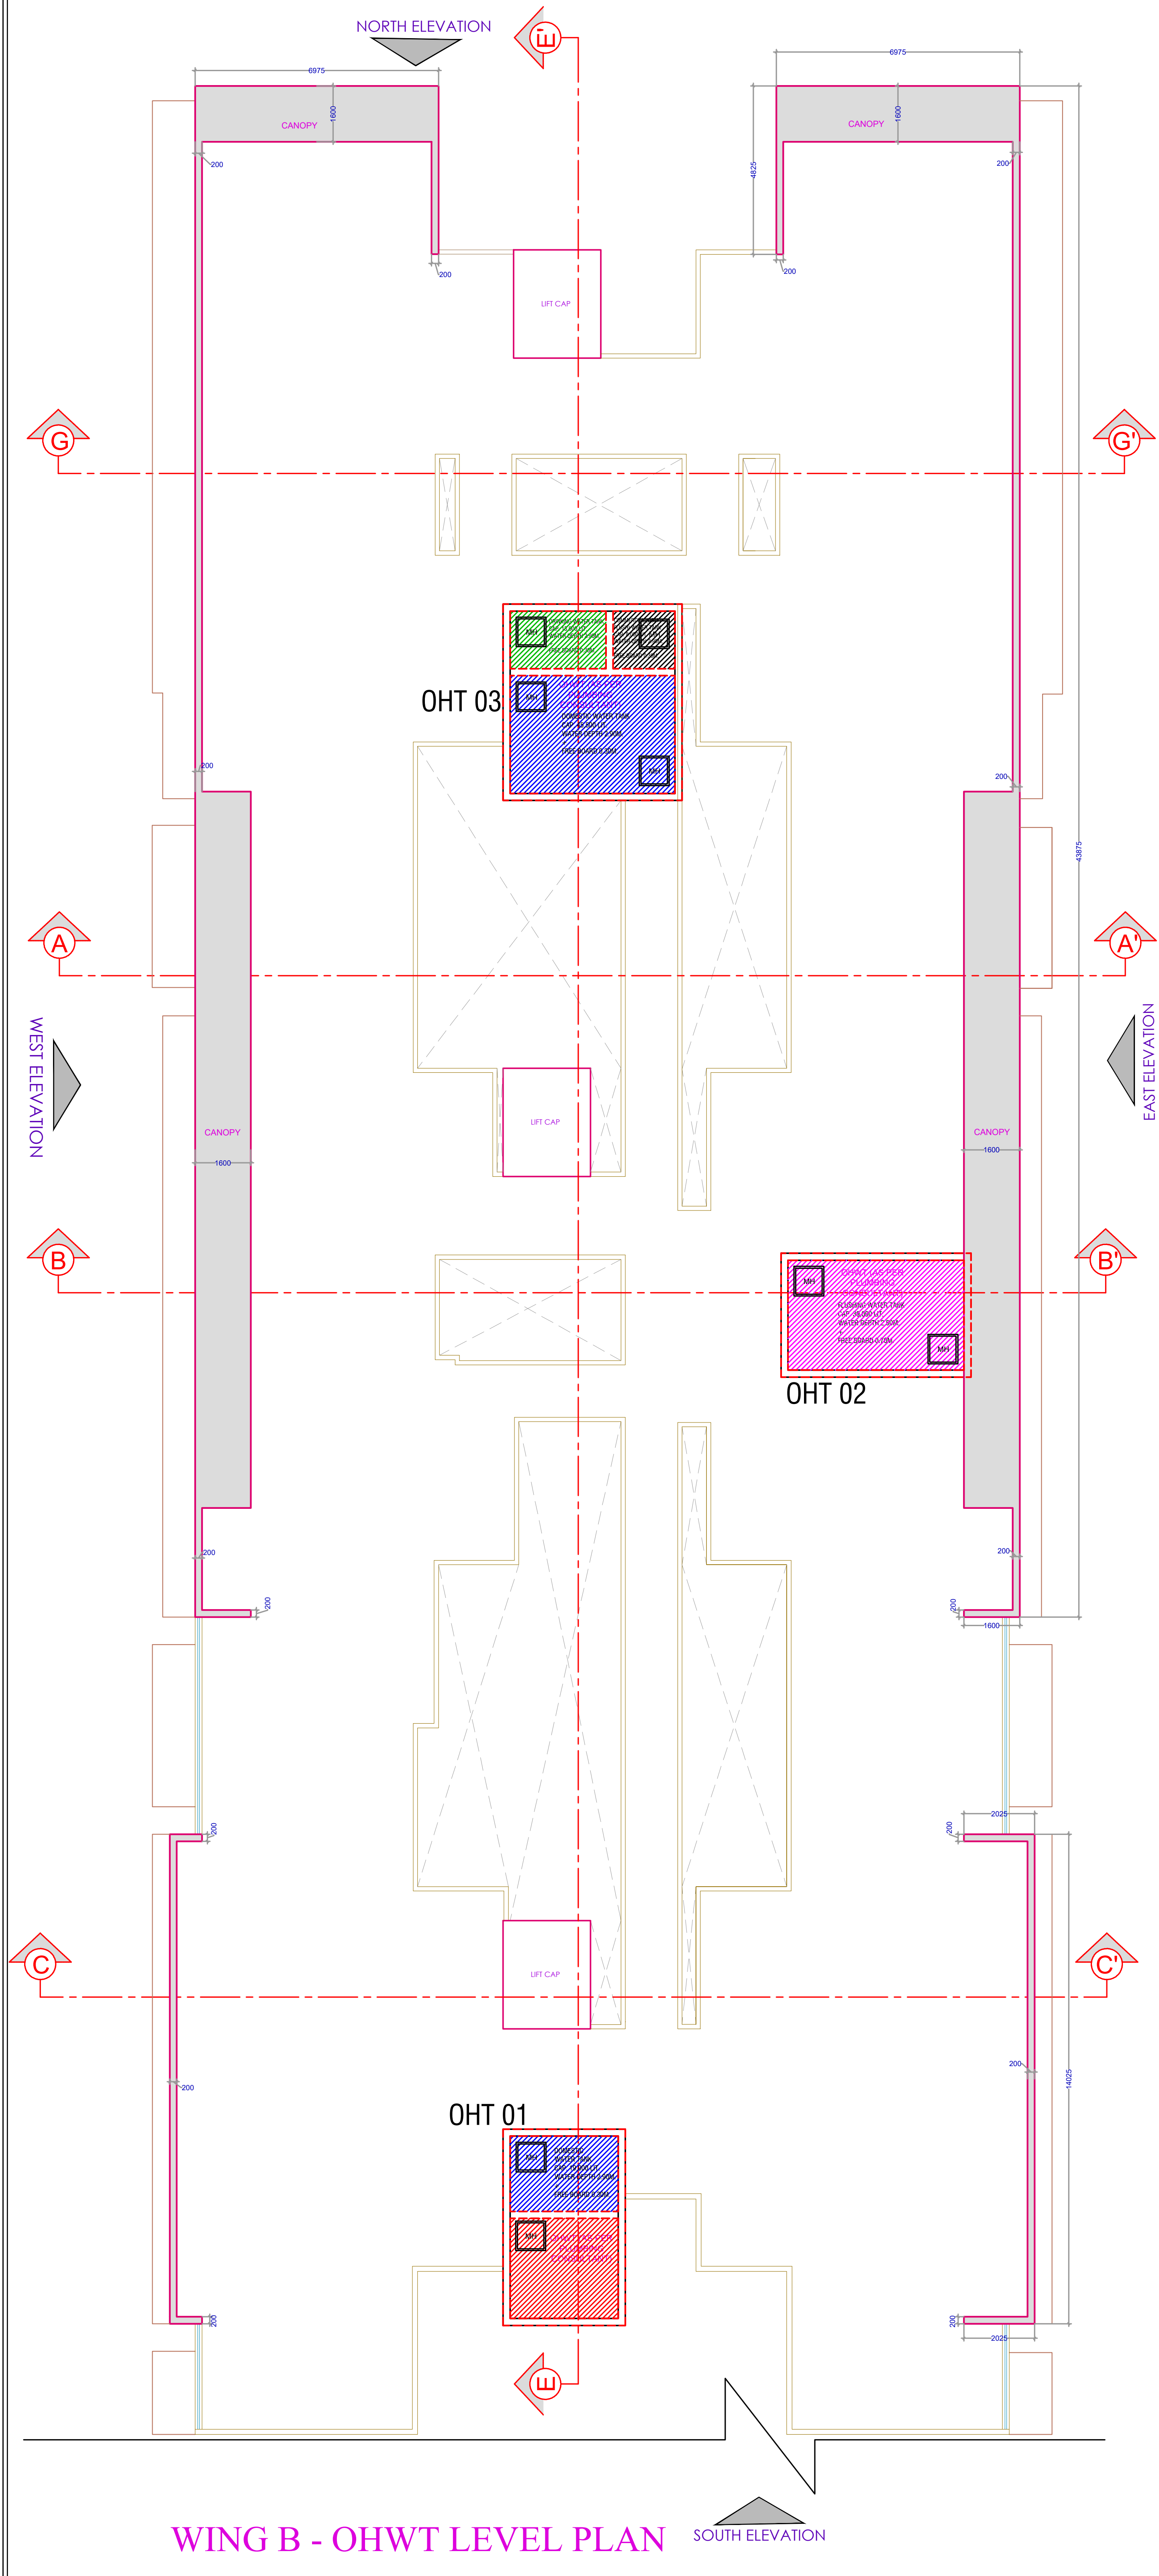

WING B - OHWT LEVEL PLAN

ARCHITECT

LANDMARK DESIGN GROUP

PLOT NO 32, SECTOR NO 29, ISKCON TEMPLE ROAD
NEAR PCMC WATER TANK, RAVET, PRADHIKARAN, PUNE
E-MAIL-landmarkdg@gmail.com PH NO 9763033222
www.landmarkdesigngroup.in

GENERAL NOTES:

THIS DRAWING IS SOLE PROPERTY OF LANDMARK DESIGN GROUP AND IS NOT TO BE COPIED OR USED WITHOUT PRIOR PERMISSION.

ALL DIMENSIONS SHALL BE CO-RELATED WITH STRUCTURAL AND SERVICE DRAWINGS AND ANY AMBIGUITY SHALL BE IMMEDIATELLY BROUGHT TO THE NOTICE OF THE ARCHITECTS BEFORE THE COMMENCEMENT OF WORK

ALL DIMENSIONS IN THE DRAWING ARE TO BE READ AND NOT TO BE MEASURED.

THIS DRAWING SHALL SUPERSEDE ITS PREVIOUS REVISIONS.

ALL DIMENSIONS ARE IN MILLIMETERS UNLESS SPECIFIED OTHERWISE.

SPECIFIC NOTES

ALL LEVELS IN THIS DRAWING ARE UNFINISHED FLOOR LEVELS.

ALL DIMENSIONS IN THIS DRAWING ARE FROM UNFINISHED SURFACES.

PROJECT :

PROPOSED RESIDENTIAL BUILDING
YASHADA VIVANTA REALITY
AT- RAVET, PUNE

OWNER :

NOTES

100 MM THK WALL	▨
125 MM THK WALL	▨
150 MM THK WALL	▨
200 MM THK WALL	▨
300 MM THK WALL (ELEVATION)	▨
200 MM SUNK	▨
150 MM SUNK	▨

DRAWING RELEASED

☐ FOR DISCUSSION ☐ FOR PRELIMINARY
☑ FOR TENDER ☐ FOR EXECUTION

REVISION	REVISION DATE	DISCRIPTION
R1	21.12.2023	CHANGES SA PER ELEVATION FEATURE WALL AT TERRACE SLAB LVL.

DRAWING NAME: OHWT FLOOR PLAN

DATE :	27.11.2023	JOB. NO.	_
REV DATE:	21.12.2023	REV NO:	R1
DRAWN BY :	AKSHAY	CHECKED :	TUSHAR
		SCALE :	N.T.S.

N

SEAL & SIGN