

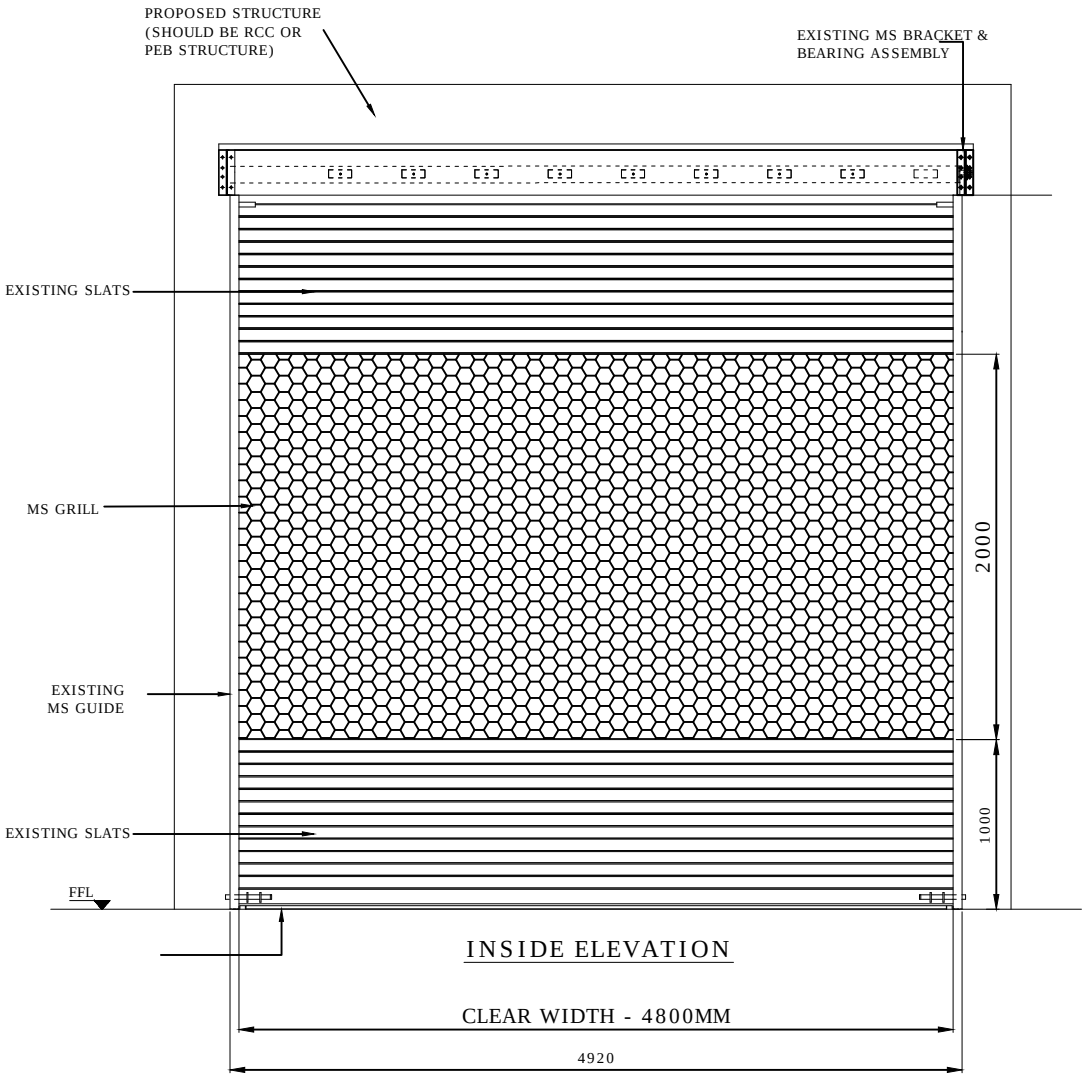



INSIDE ELEVATION

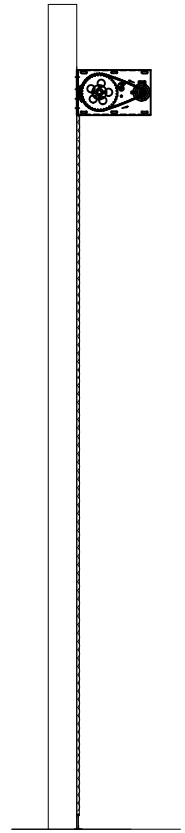

SIDE VIEW

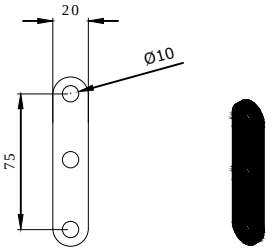


5 m m THK. LINK

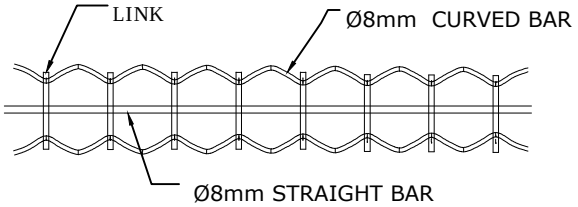

GRILL DETAILS

PLEASE PROVIDE 4 MM DIA BAR FOR
GRILL & SHUTTER SLAT LOCKING = 2 NOS

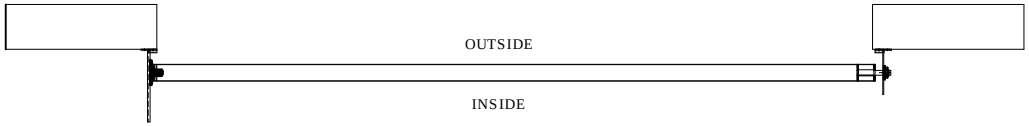

PLAN

NOTE:-

1. ONLY M.S GRILL IS ADDED IN EXISTING ROLLING SHUTTER.
2. SLAT NOTCHES IS REQ. FOR SHUTTER & GRILL BAR LOCKING.

This drawing & designing is the property of NIHVA TECHNOLOGIES. Not to be sold or copied to any other concern.

TITLE				
GRILLED ROLLING SHUTTER				NIHVA TECHNOLOGIES PVT. LTD. PUNE Tel : 020 66304033 Email:- info@nihva.com Website:- www.nihva.com
	NAME	SIGN	DATE	
DRAWN	P.A		28.11.2019	CLIENT -
CHECK	V.T		28.11.2019	PROJECT -
APPROVAL				SITE -
REV.				DWG. NO. : NIHVA/19-20/VDR/230 | REV : R00
If any queries contact : projects@nihva.com				SCALE: NTS | WT: | SHEET: 01 OF 01
ALL DIMENSION ARE IN mm				