MATERIAL:-G.I

DOOR HANDLING:
SINGLE DOOR ???? HAND ACTIVE

INFILL: HONEY COMB

RAL NO FRAME:-
RAL NO LEAF:-

PANIC BAR :
MODEL NO.- LOCKWOOD MAKE
PE RM501P
PHT LOCK :
MODEL NO. LOCKWOOD MAKE
PE ACC004


DOOR CLOSER : STD ARM - MODEL NO-YADC 6003 -YALE MAKE

ACCESSORIES:-
1.SS BALL BEARING HINGES
3S2BB403030-CE-M =YALE MAKE
2.SMOKE SEAL-S88BL-PEMKO MAKE


FRAME SHEET THIK.1.2mm
LEAF SHEET THIK.0.8 mm

POWDER COATED METAL CAP WITH RAL

2 HRS FIRE RATED

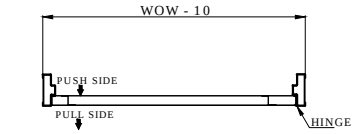


TOP VIEW

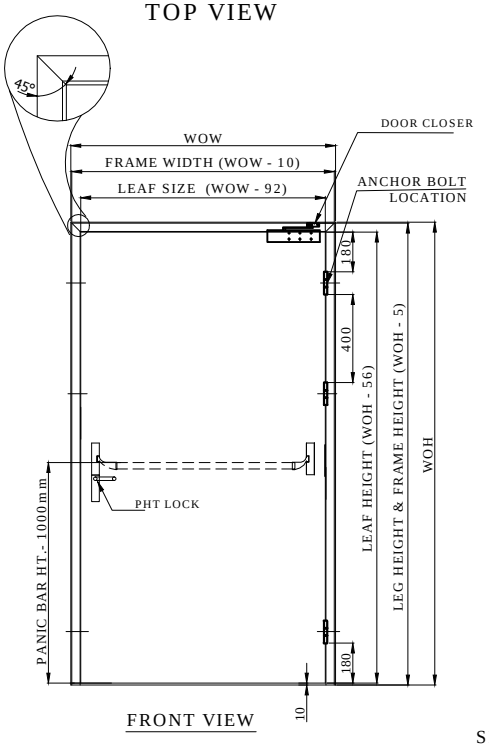


FRONT VIEW




SIDE VIEW
SECTION A-A'

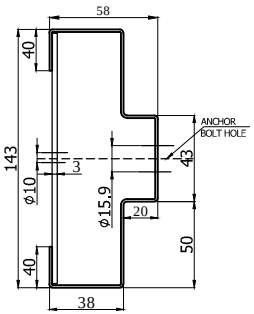


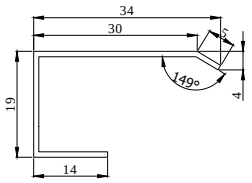

SEE DETAIL 'C'

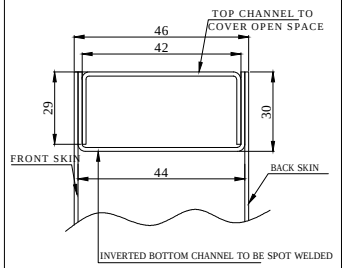

DOOR TOP SECTION DETAIL

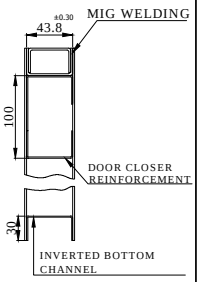

DOOR BOTTOM & TOP DETAIL

SR. NO	WALL OPENING WIDTH	WALL OPENING HEIGHT	QTY	RAL	LOCATION	HARDWARE
04	1200	2100	12	3020	Block F	Hinges , Door closer , Single point panic bar, with external trim
03	1200	2100	04	3020	Block D	Hinges , Door closer , Single point panic bar, with external trim
02	1200	2100	12	3020	Block C	Hinges , Door closer , Single point panic bar, with external trim
01	1200	2100	01	3020	A-Block North Side Mezzanine Exit Door (GD2)	Hinges , Door closer , Single point panic bar

TOLERANCE - ±05mm

REV. NO	DATE	DRAWN	REMARK
R01	18.03.19	P.V.A	1.SPECIFICATION CHANGE

This drawing & design is the property of NIHVA TECHNOLOGIES. Not to be sold or copied to any other concern.

TITLE: FIRE RATED SINGLE LEAF STEEL DOOR

NIHVA TECHNOLOGIES PVT. LTD.
NIHVA TECHNOLOGIES PVT. LTD. PUNE
Tel : 020 66304033
Email:- info@nihva.com
Website:- www.nihva.com

	NAME	SIGN	DATE
DRAWN	P.V.A		16.03.2019
CHECK	V.M.T		16.03.2019
APPRD.			

CLIENT - SYNERGY
PROJECT - EMBASSY
SITE LOCATION - CHAKAN, PUNE.

If any queries contact : design@nihva.com
DWG. NO. : NIHVA/18-19/0293
REV- R00

ALL DIMENSION ARE IN mm
SCALE: NTS
WT:
SHEET: 01 OF 01