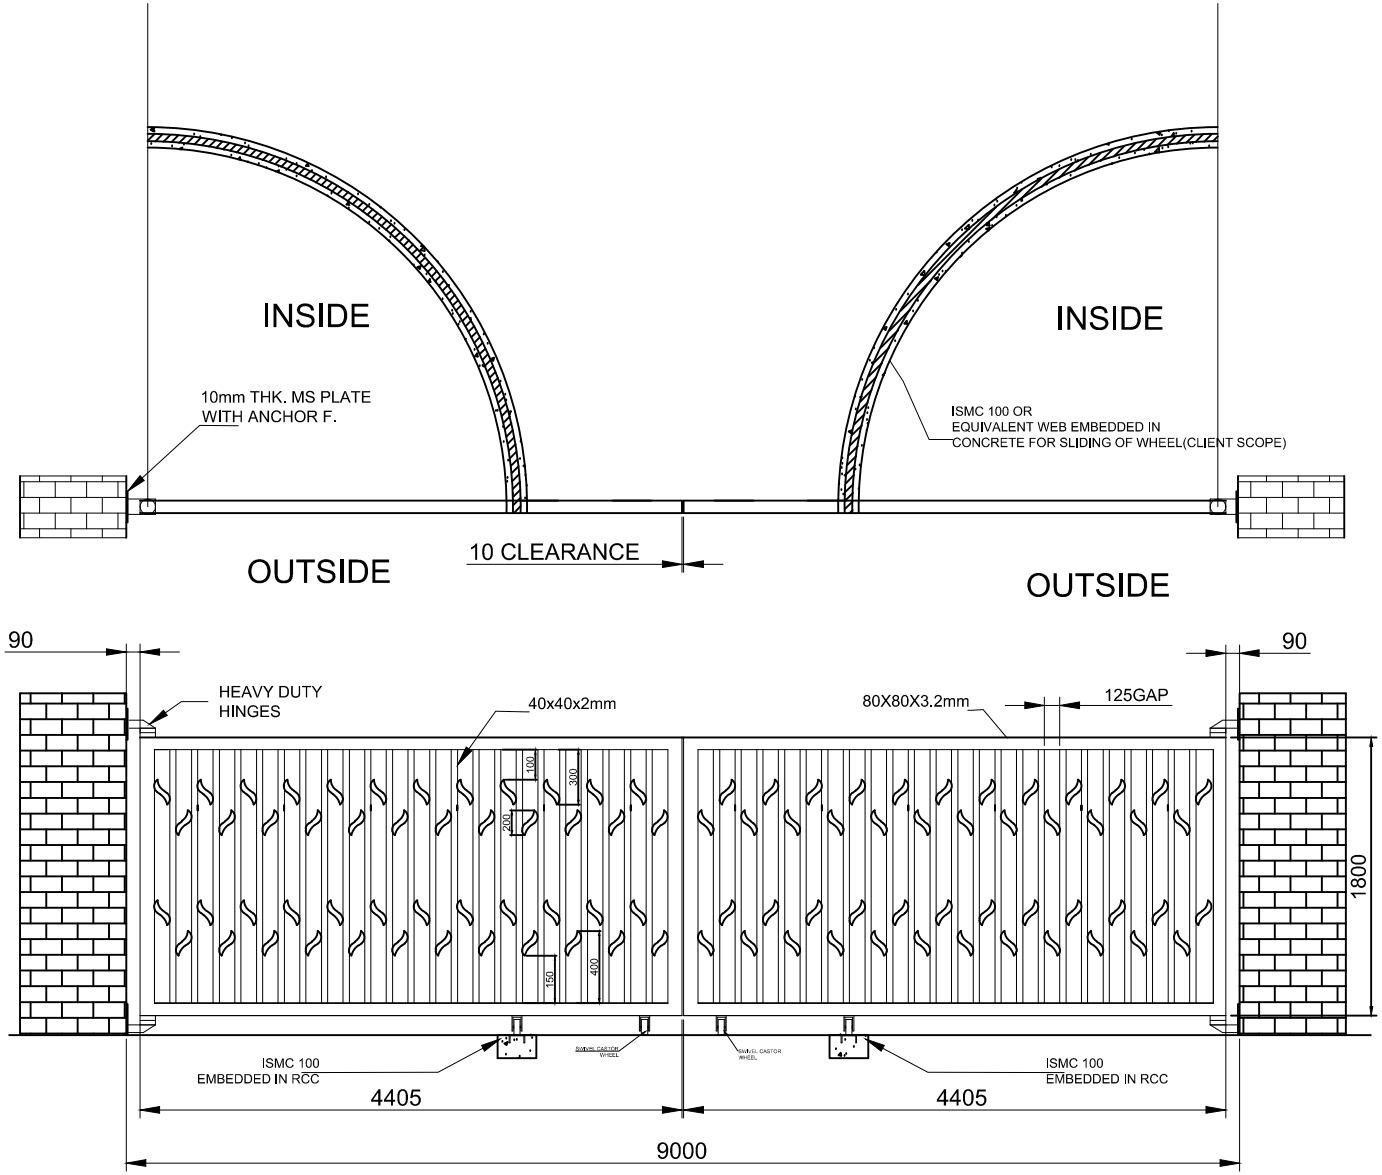


OUTSIDE ELEVATION

REV.	DESCRIPTION	DRAWN	DATE
R02	CLEAR WIDTH CHANGED TO 9000	S.M.S.	30.12.20
R01	PROFILE PATTERN ADD	P.V.A	24.05.2019

SR.NO	RAL CODE	RAL COLOR
04	RAL 7035	LIGHT GREY
03	RAL 5002	ULTRAMARINE BLUE
02	RAL 9002	GREY WHITE
01	RAL 1004	GOLDEN YELLOW

DIMENSION :

CLEAR WIDTH	CLEAR HEIGHT	QUANTITY
6000mm	1800mm	2 NOS

MATERIAL: M.S

THICKNESS :

NOTE-
1. ALL REQUIRED CIVIL WORK WILL BE IN CLIENTS SCOPE.

2.IN NECESSARY GATE LEAF WILL BE IN TWO PARTS FOR TRANSPORTATION AND WILL BE WELDED TOGETHER ON SITE

NIHVA
NIHVA TECHNOLOGIES PVT. LTD.
NIHVA TECHNOLOGIES PVT. LTD. PUNE
Email:- info@nihva.com
Website:- www.nihva.com

TITLE:

MANUAL DOUBLE LEAF SWING GATE.

CLIENT'S APPROVAL :

CLIENT - INDAMER TECHNICS PVT. LTD.

PROJECT -

SITE LOCATION -

DWG. NO. : NIHVA/18-19/0198/R02 | REV. : 01

SCALE: NTS | WT: | SHEET:1 OF 1

DRAWN:	SURAJ		08-12-2018
CHECK :	PRADEEP		08-12-2018
APPROVED	R.D		08-12-2018

If any queries contact : design@nihva.com

NOTE: ALL DIMENSIONS ARE IN mm

THIS DRAWING & DESIGN IS THE PROPERTY OF NIHVA TECHNOLOGIES. NOT TO BE SOLD OR COPIED TO ANY OTHER CONCERN.