


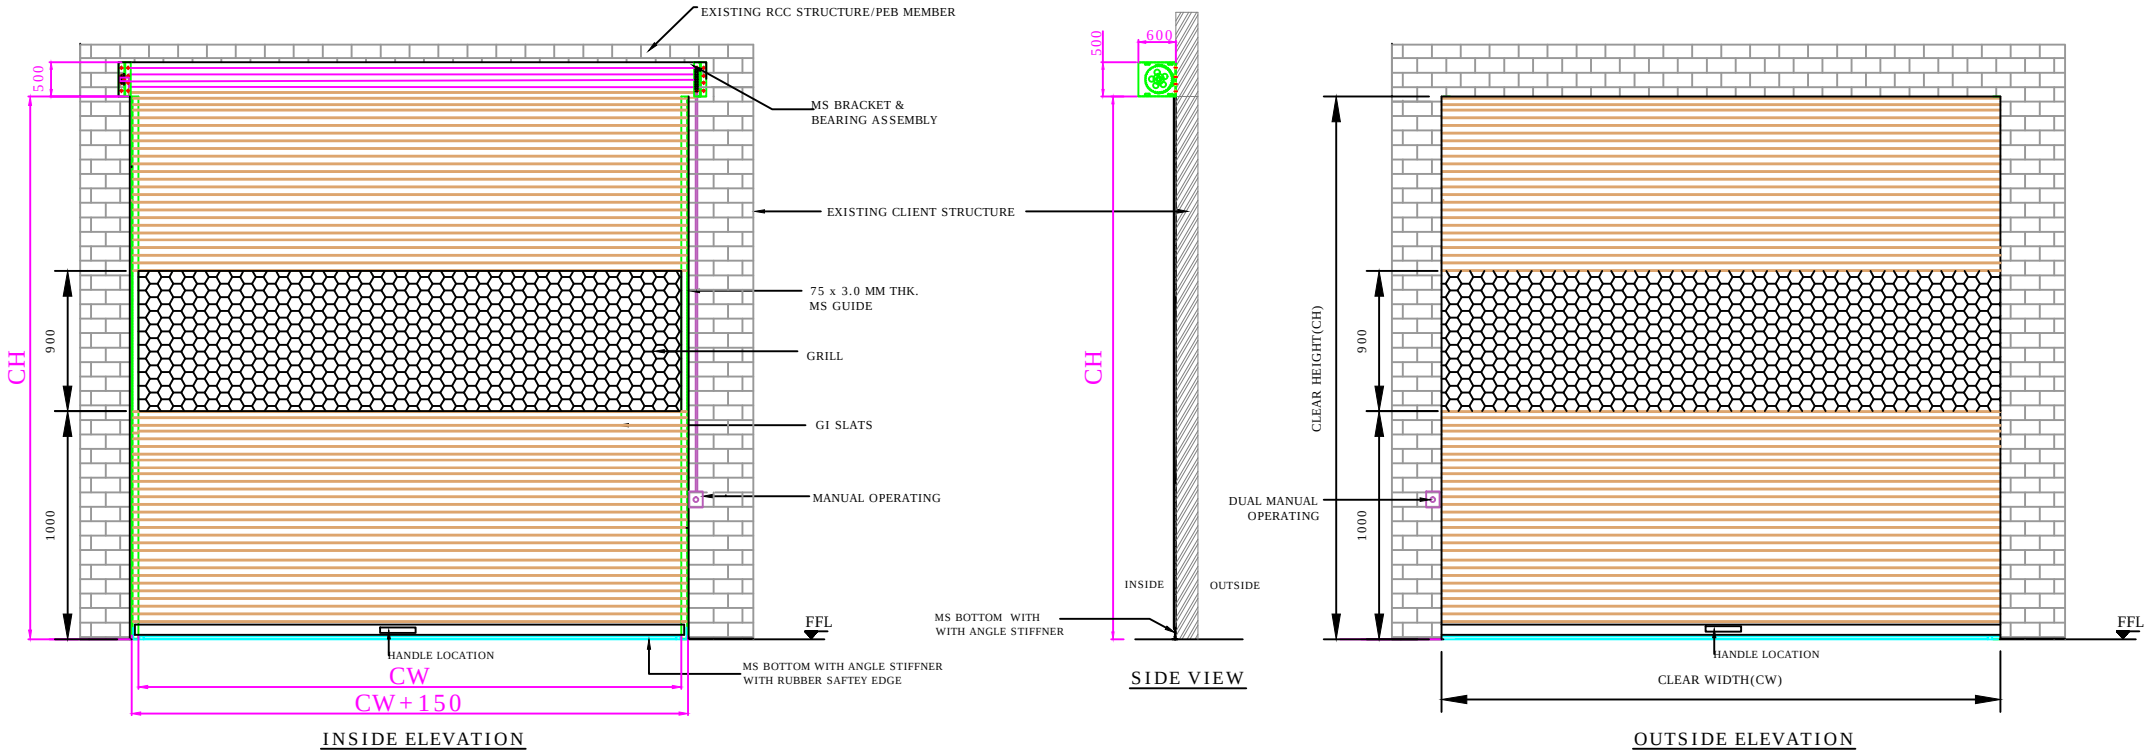


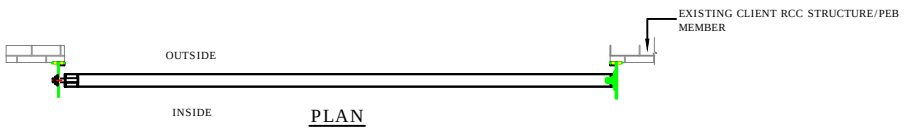

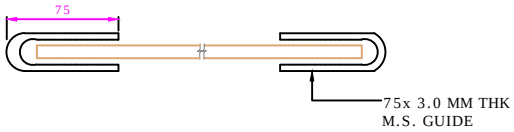

CLEAR WIDTH	CLEAR HEIGHT	QUANTITY	LOCATION
2980	3960	1	BOILER ROOM 1

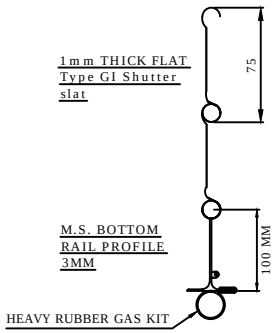

This drawing & designing is the property of NIHVA TECHNOLOGIES. Not be sold or copy to any other concern.

TITLE

GEAR OPERATED ROLLING SHUTTER

CLIENT APPROVAL

ALL DIMENSION ARE IN mm

	NAME	DATE	SIGN.
DRAWN	OMKAR	03/03/16	
CHECK	ANIL	03/03/16	
REV.	00		
APPRD.			
MFG			
Ref. No.			

NIHVA TECHNOLOGIES PVT. LTD.

NIHVA TECHNOLOGY PVT. LTD. PUNE
Tel : 020 66304033
Email:- info@nihva.com
Website:- www.nihva.com

CLIENT - LUPIN

PROJECT -

SITE -

DWG. NO. - NIHVA/15-16/206

SCALE: 01 | WT: | SHEET: 01 OF 01

If any queries contact : projects@nihva.com