


NOTE : ~ PLEASE MAINTAIN 8 MM GAP BETWEEN TWO LIP BUSHES.

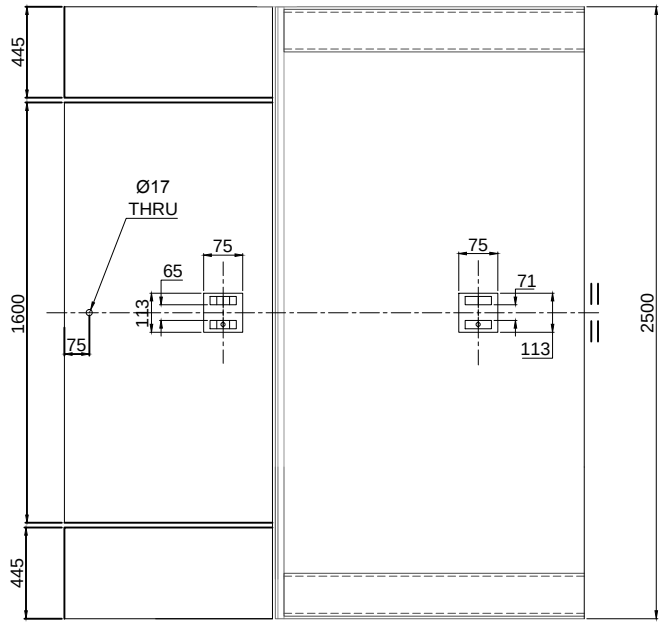



1

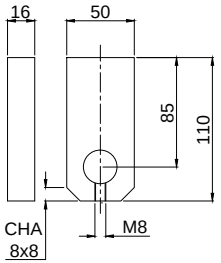

2

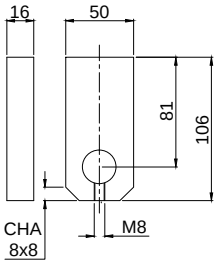

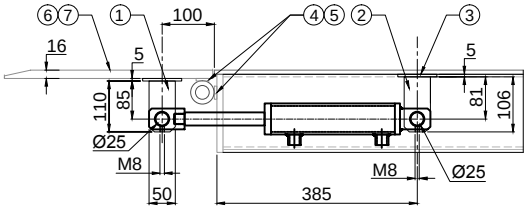

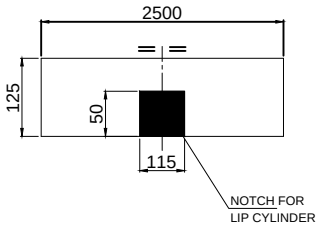

NOTE:~ MTL : MS

PART NO.	PART NAME	DESCRIPTION	QTY
1.	FLAT	50 X 16 X 113L	2 NOS
2.	FLAT	50 X 16 X 110L	2 NOS
3.	FLAT	75 X 5 X 113L	2 NOS
4.	FLAT	25 X 5 X 80L	14 NOS
5.	FLAT	25 X 5 X 60L	8 NOS
6.	PROFILE	400 X 16 X 1600L	1 NO
7.	PROFILE	400 X 16 X 445L	2 NOS

NOTE:~ MTL : MS

1. FLAT 50 X 16 X 113L = 2 NOS (SEE DRG)
2. FLAT 50 X 16 X 110L = 2 NOS (SEE DRG)
3. FLAT 75 X 5 X 113L = 2 NOS
4. FLAT 25 X 5 X 80L = 16 NOS
5. FLAT 25 X 5 X 60L = 10 NOS
6. PROFILE LIP 400 X 16 X 1600L = 1 NO
7. PROFILE LIP 400 X 16 X 445L = 2 NOS

TOLERANCE - ±5mm

This drawing & design is the property of NIHVA TECHNOLOGIES. Not to be sold or copied to any other concern.

TITLE

LIP CYL MOUNTING

NIHVA TECHNOLOGIES PVT. LTD.

NIHVA TECHNOLOGIES PVT. LTD. PUNE
Tel : 020 66304033
Email:- info@nihva.com
Website:- www.nihva.com

	NAME	SIGN	DATE
DRAWN	PRADEEP		23.04.2018
CHECK	PRADEEP		23.04.2018
APPRD.	PRADEEP		23.04.2018

CLIENT -

PROJECT - DLMP1004

SITE LOCATION -

If any queries contact : design@nihva.com

DWG. NO. : NIHVA/18-19/DLMP1004_008

ALL DIMENSION ARE IN mm

SCALE: NTS | WT: | REV- 0