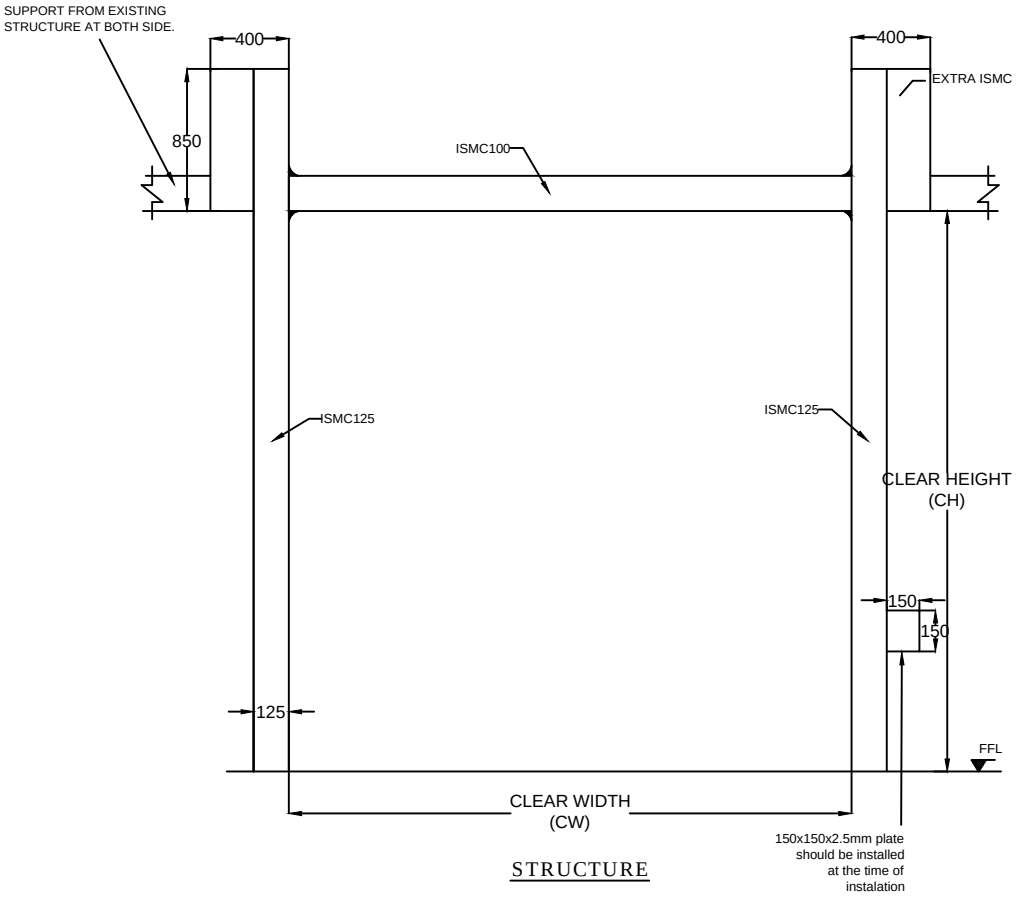

STRUCTURE

GRILL SIZE (CW) X (CH)	CLEAR WIDTH (CW)	CLEAR HEIGHT (CH)	QUANTITY
-	3000	6000	02
-	5000	6000	12
7000 X 1000	7000	8000	21
7000 X 1000	7000	7000	04
8000 X 1000	8000	6000	03
6000 X 1000	6000	6000	04

This drawing & designing is the property of NIHVA TECHNOLOGIES. Not to be sold or copied to any other concern.

TITLE
MOTORIZED ROLLING SHUTTER STRUCTURE

NIHVA TECHNOLOGIES PVT. LTD. PUNE
Tel : 020 66304033
Email:- info@nihva.com
Website:- www.nihva.com

	NAME	SIGN	DATE
DRAWN	SURAJ		19/06/18
CHECK	PRADEEP		19/06/18
APPROVAL	PRADEEP		19/06/18

If any queries contact : design@nihva.com

ALL DIMENSION ARE IN mm

CLIENT -REWARD

PROJECT - MMBPL

SITE - INDAPUR.

DWG. NO. : NIHVA/21-22/0220 REV. - 0

SCALE: NTS WT: SHEET: 01 OF 01