SR. NO.	DESCRIPTION	SIZE
1	WICKET GATE	2.0 (w) x 1.8 (h) m

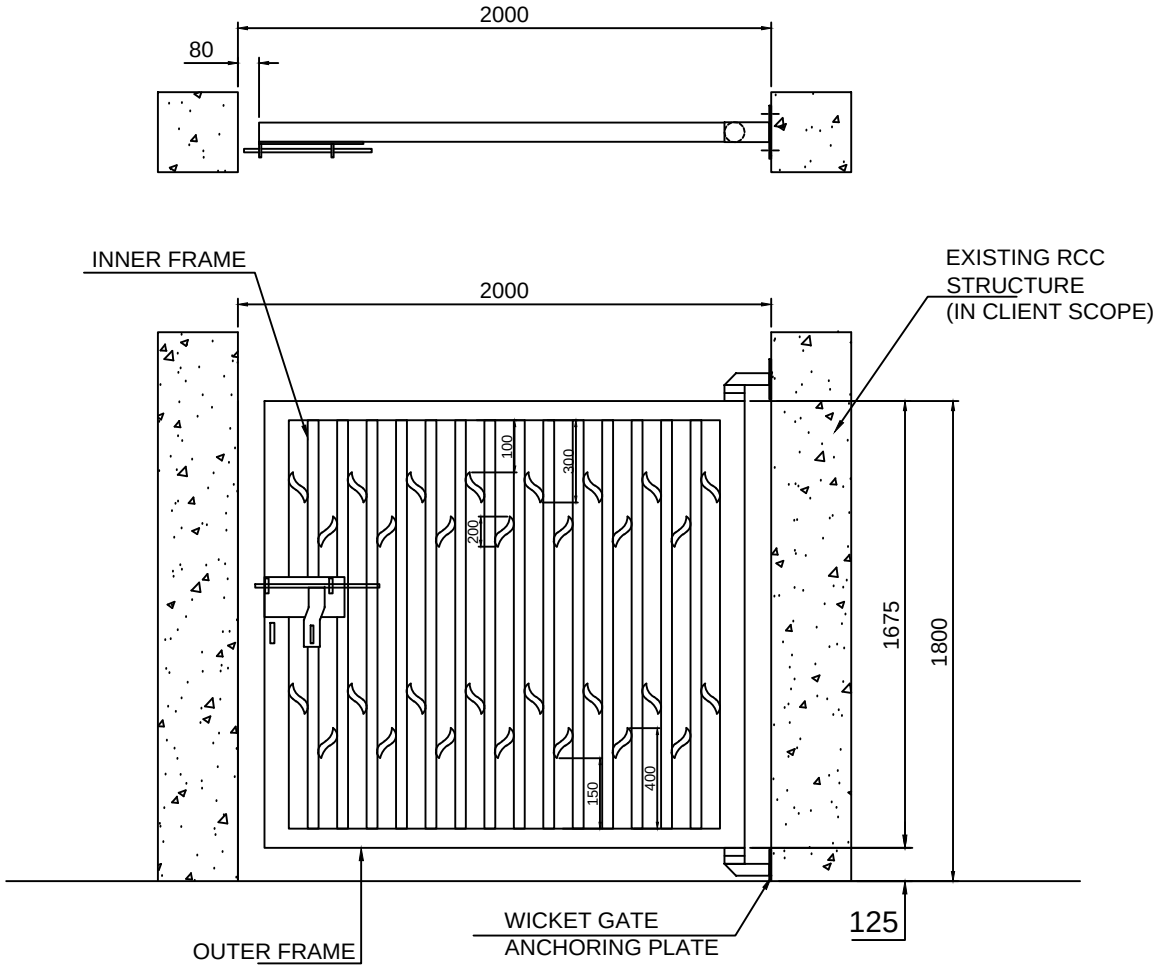

REV.	DESCRIPTION	DRAWN	DATE
R01	PROFILE PATTERN ADD	P.V.A	24.05.2019

This drawing & designing is the property of NIHVA TECHNOLOGIES. Not be sold or copy to any other concern.

TITLE	WICKET GATE 2 x 1.8		
	SIGN	DATE	
DRAWN	A.K.	07.05.2019	CLIENT - IDAMAR
CHECK	P.A.	07.05.2019	PROJECT -
REV.			SITE - NAGPUR
APPROVAL	V.T.		DWG. NO. : NIHVA/19-20/0016/R01 / REV : R01
If any queries contact : design@nihva.com			SCALE: NTS / WT: / SHEET: 01 OF 01
ALL DIMENSION ARE IN mm			

NIHVA TECHNOLOGIES PVT. LTD.
NIHVA TECHNOLOGY PVT. LTD. PUNE
Tel : 020 66304033
Email:- info@nihva.com
Website:- www.nihva.com