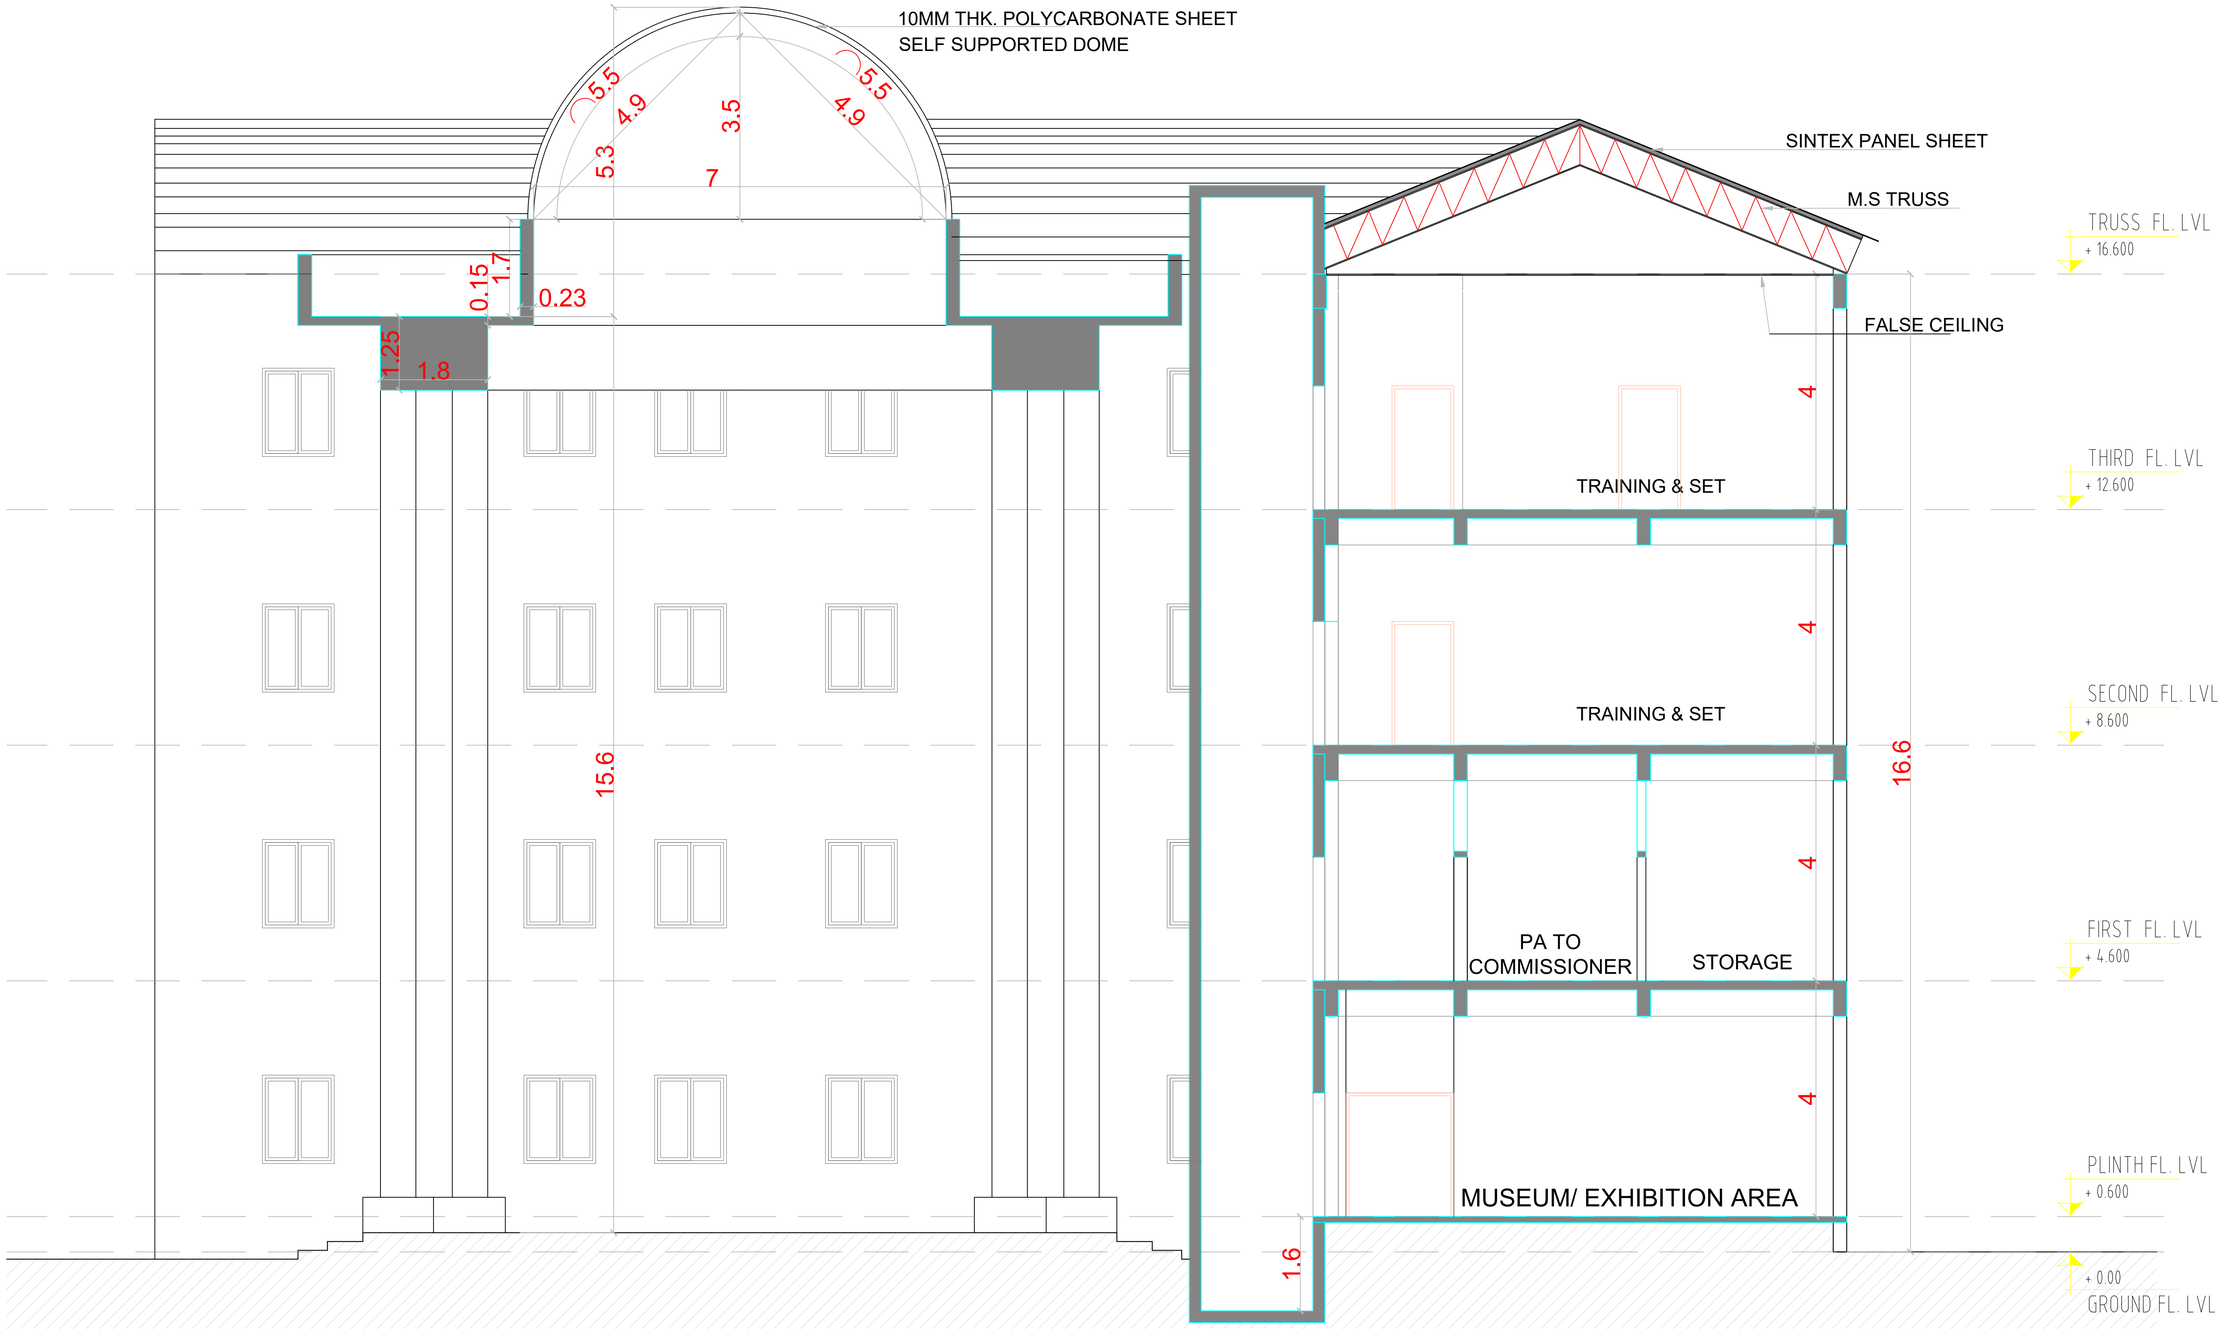

10MM THK. POLYCARBONATE SHEET
SELF SUPPORTED DOME
5.5
4.9
3.5
5.3
7
0.15
1.7
0.23
1.25
1.8
15.6
SINTEX PANEL SHEET
M.S TRUSS
TRUSS FL. LVL
+ 16.600
FALSE CEILING
4
TRAINING & SET
THIRD FL. LVL
+ 12.600
4
TRAINING & SET
SECOND FL. LVL
+ 8.600
16.6
4
PA TO
COMMISSIONER
STORAGE
FIRST FL. LVL
+ 4.600
4
MUSEUM/ EXHIBITION AREA
PLINTH FL. LVL
+ 0.600
1.6
+ 0.00
GROUND FL. LVL

SECTION-XX'