



Gate Opening Position

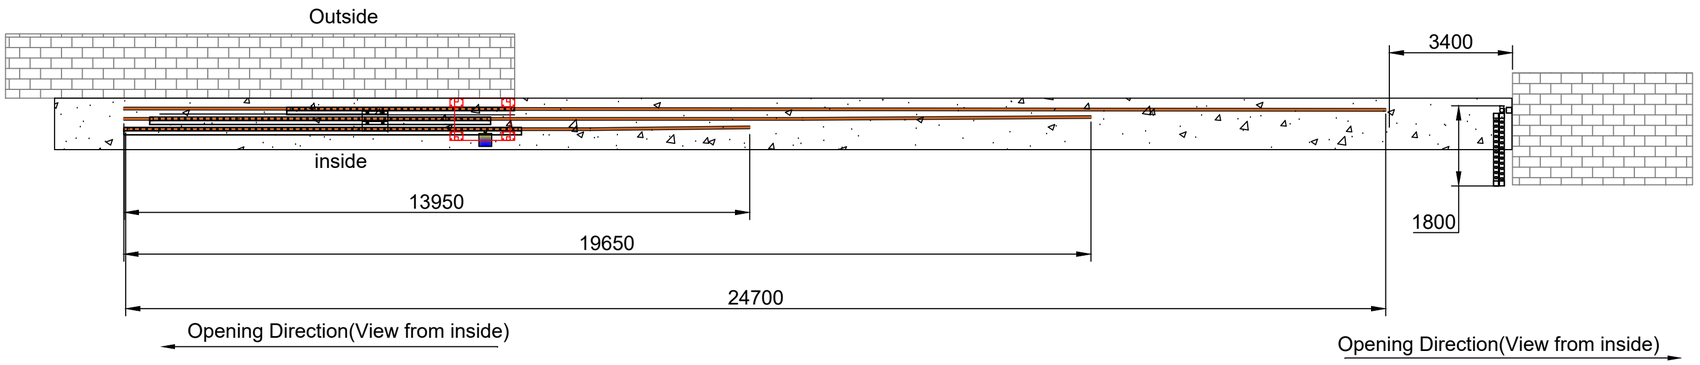

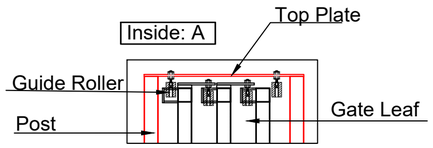

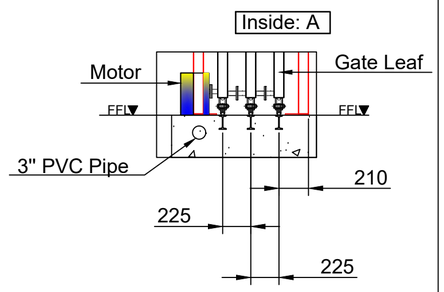

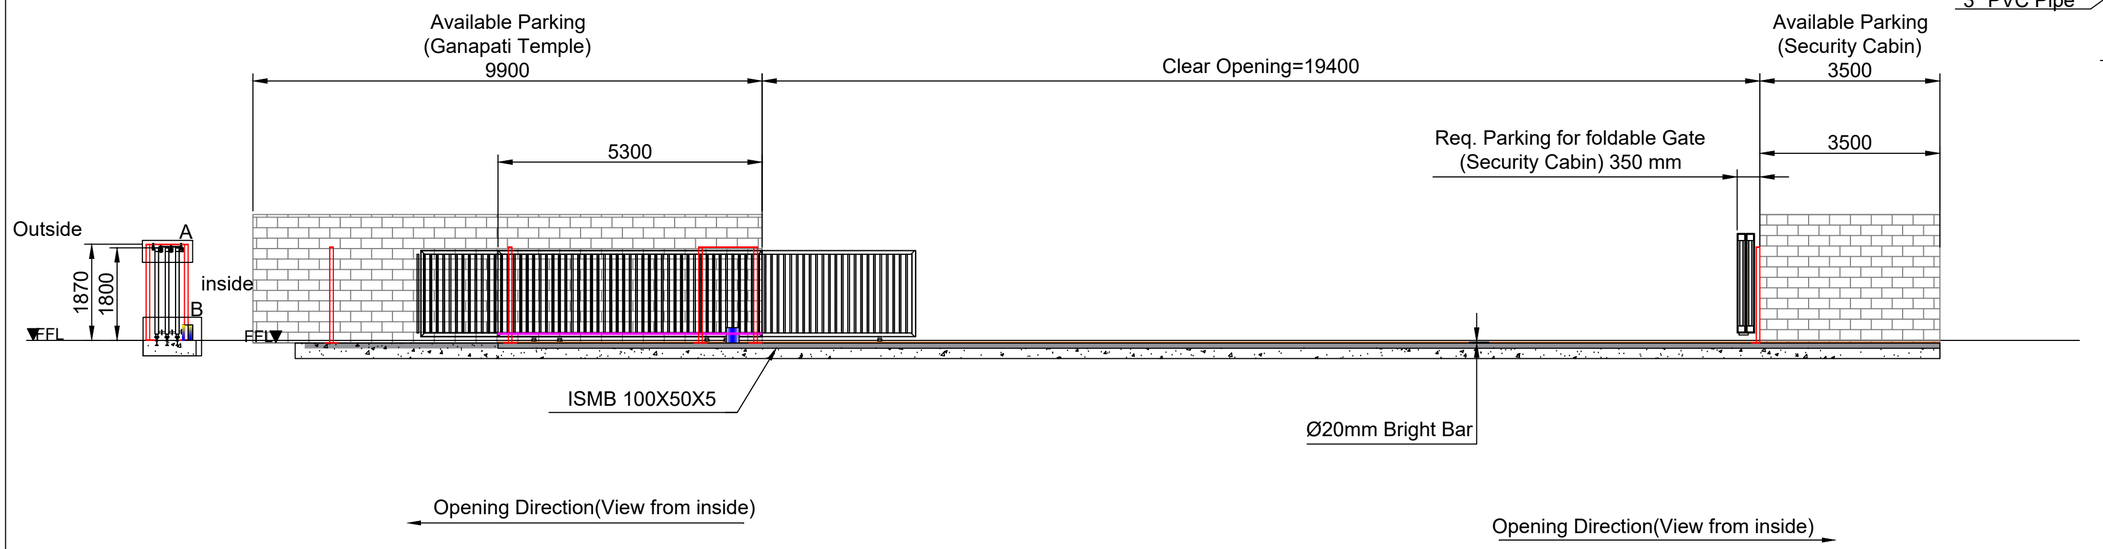

Note:-

1.All Dimension are in MM

2.Required All civil work will be in Client scope

3.Installlation and Fabrication tolerance will be ±20mm

4. Required Parking will be 8000 mm

5. Gate Color will be Metalic color,shade stone gray(RAL7030)

Rev No.	Revision	Date	Revised By
01	As per New Opning	30/07/2022	Sujata

This drawing & design is the property of NIHVA TECHNOLOGIES. Not to be sold or copied to any other concern.

TITLE:- Bi-Parting Tel.Sliding Gate				NIHVA TECHNOLOGIES PVT. LTD. PUNE Tel : 020 66304033 Email:- info@nihva.com Website:- www.nihva.com	
	NAME	DATE	SIGN		
DRAWN	MAHESH.S	30/07/2022		CLIENT - NAVNEET EDUCATION LTD	
CHECK	MAHESH.S	30/07/2022		LOCATION - PALGHAR	
APPRD.	AMIT.K	30/07/2022		PRODUCT - TEL.SLIDING GATE	QTY-01
If any queries contact : design@nihva.com				DWG NO:- NIHVA/22-23/CLT/0071_7	REV-01
ALL DIMENSION ARE IN mm				SCALE: NTS	SCALE:-- 1:1 SHEET: 01 OF 01