
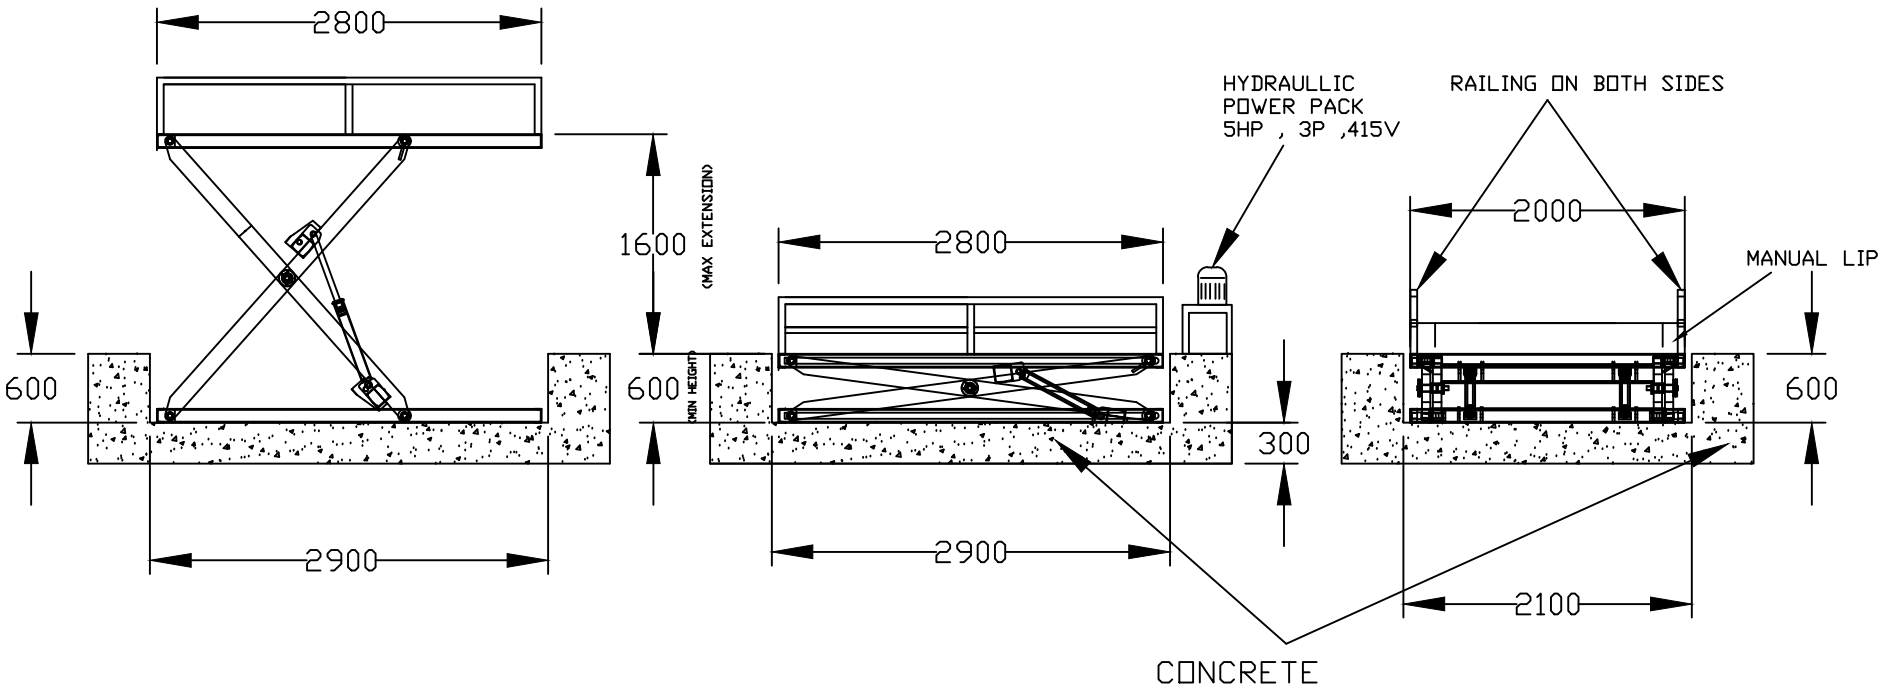



PIT SIZE = 2900X2100X600 MM

NOTE:

1. PIT FOR SCISSOR LIFT HAS TO BE DIAGONALLY WITHIN 3-5MM
2. BASE OF THE PIT HAS TO BE IN WATER LEVEL AND RIGHT ANGLE TO THE VERTICAL SIDE WALL
3. PROPER ARRANGEMENTS FOR ROUTING HOSES AND CABLES HAVE TO BE MADE DEPENDING ON SITE CONDITIONS AND POSITION OF POWER PACK
4. COVERING REQUIRED FOR CABLES AND RELEATED CIVIL WORK IS IN CLINT SCOPE
5. WATER DRAINAGE AND PIT CLEANING NEEDS TO BE CONSIDERED AND DONE BY CLINT
6. PIT & CIVIL WORK IS IN CLINT SCOPE
7. TOLERANCE ±10 MM

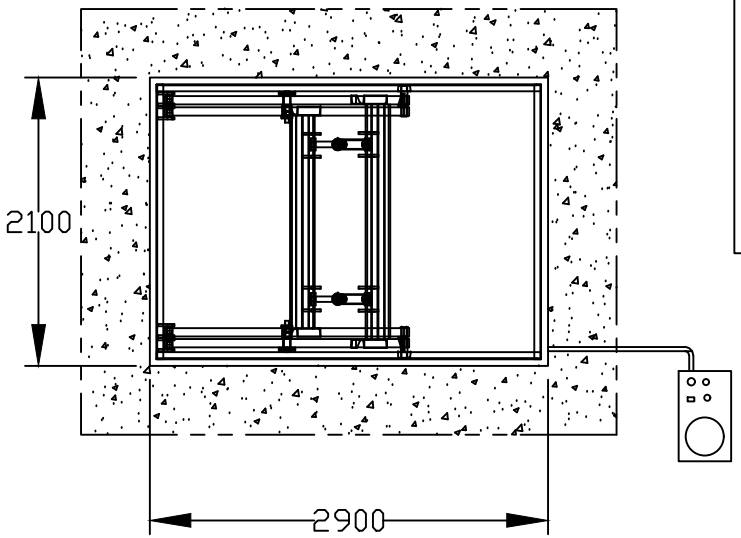


TECHNICAL SPECIFICATIONS

1. PLATFORM SIZE: 2800X2000 MM
2. CAPACITY : 1500 KGS
3. MAX EXTENSION: 1600 MM
4. MINIMUM HEIGHT: 600 MM
5. HYDRAULIC POWERPACK OPERATED
6. MOTOR = 5HP , 3ø, 415V
7. MANUAL LIP ON ONE SIDE
8. RAILING ON TWO SIDES

**NIHVA TECHNLOGIES PVT LTD**

| | | | |
|---|---|---|---|
| | | TITLE; HYDRAULIC SCISSOR LIFT | |
| DRAWN | 19/11/21 | CAPACITY; 1500KGS. | SHEET; 1 OF 1 |
| CHKD | | DRAWING NO. | REV. |
| APPD. | | NIHVA\21-22\0254 | R01 |
| SCALE NTS | A4 | THIRD ANGLE | |