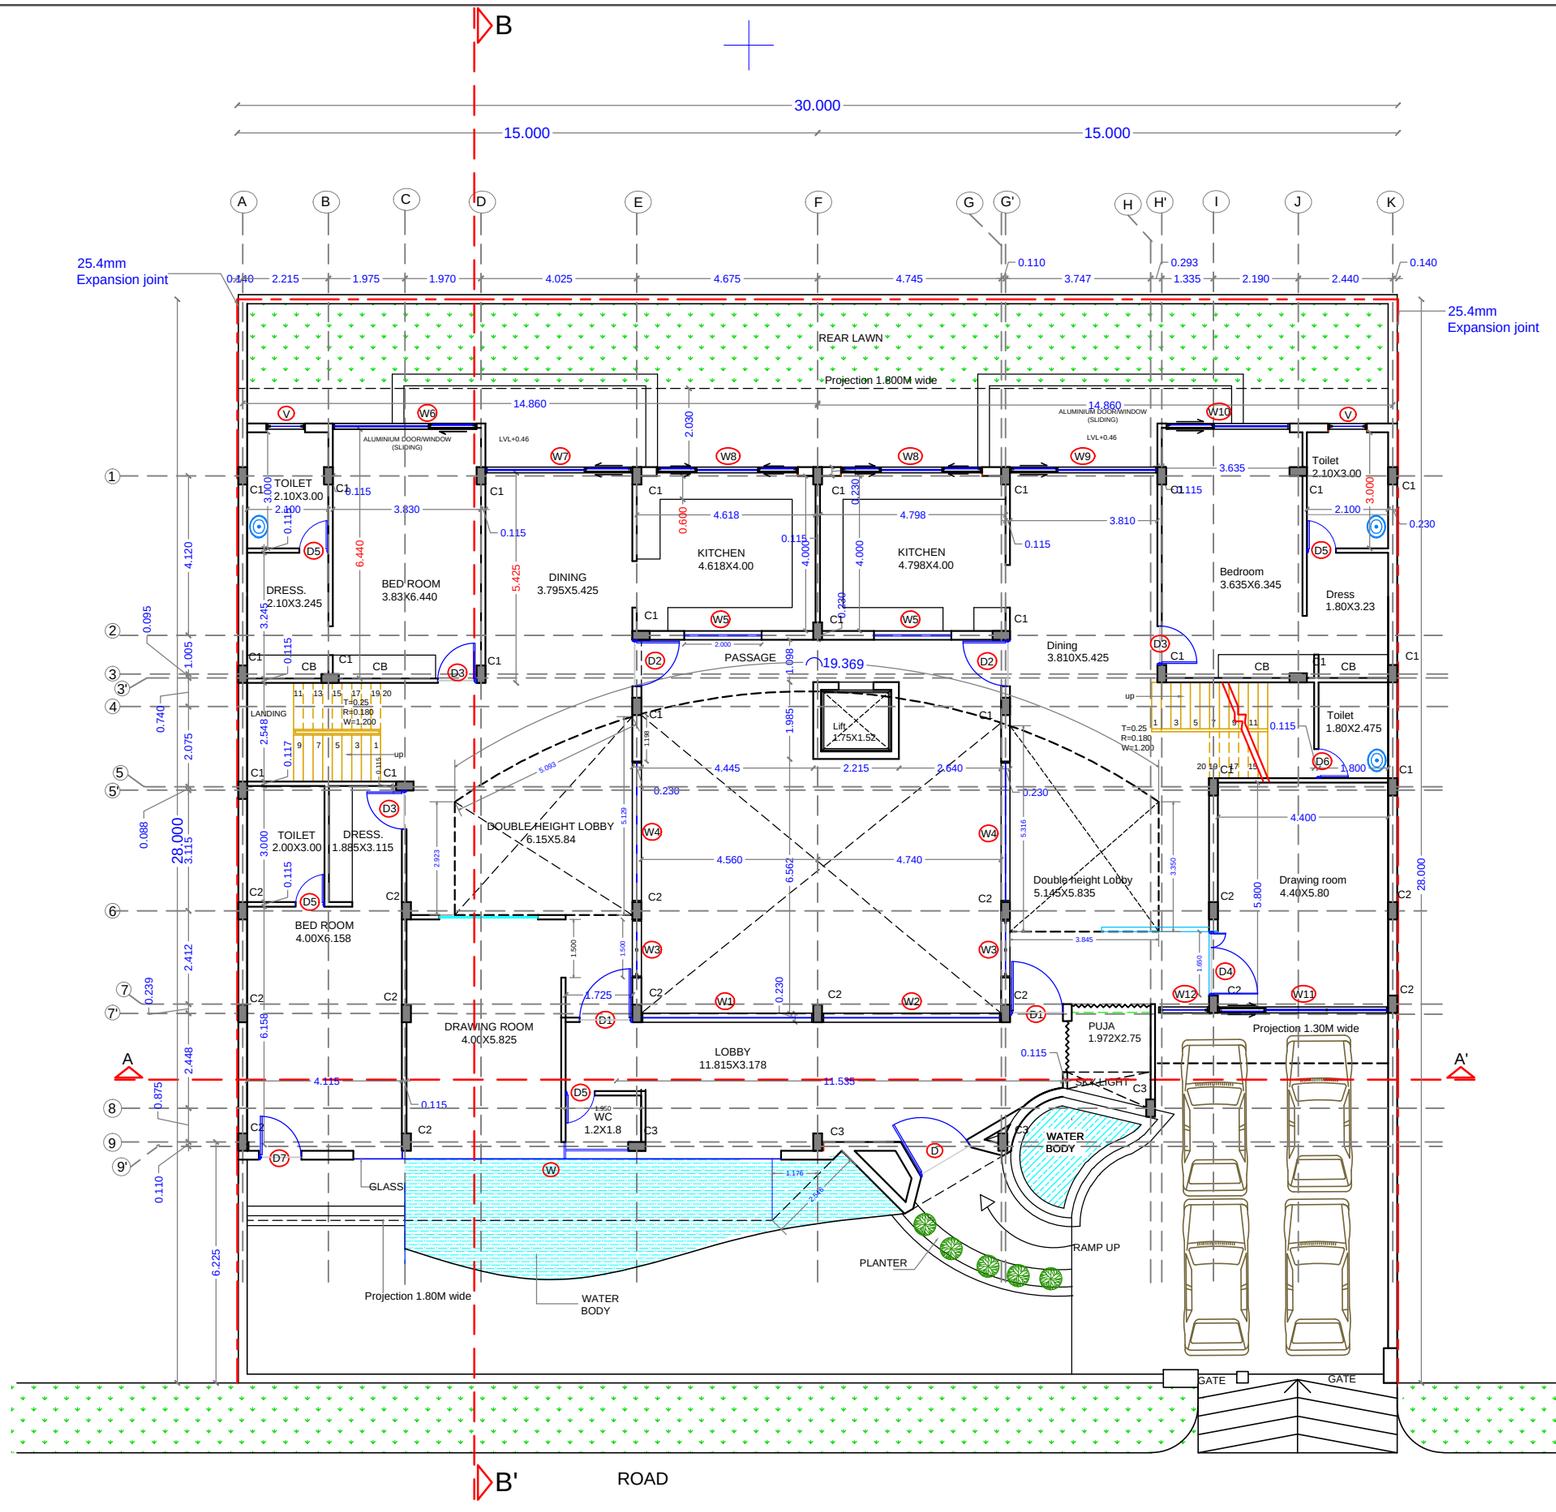


GROUND FLOOR PLAN

PROJECT:-

PROPOSED HOUSE FOR ROMIL GARG & KAVITA GARG PLOT NO. 11, B-1 STREET B BLOCK, VATIKA CITY CENTRAL, SECTOR 23 AMBALA

REVISIONS

S.NO.	NOTES	DATE

SHEET TITLE:-

WORKING DRAWING

DRG.TITLE:-

GROUND FLOOR PLAN

DEALT BY:-	JATINDER
CHKD BY:-	
DATE:-	17-04-2021
DRG.NO :- **WD/RS/WD-01**	SCALE :-
CLIENT:-	P.M.C:-

ARCHITECT:-

Renu Khanna & Associates
architects, engineers,interiors and landscape planners
off/res:138, sec.-10 panchkula
Ph: 0172 - 2563379
M: 09872627180, fax: 01722584538
Email: renukhanna.architect@gmail.com
renukhanna.architect@yahoo.com
Web: architectsrenukhanna.com