

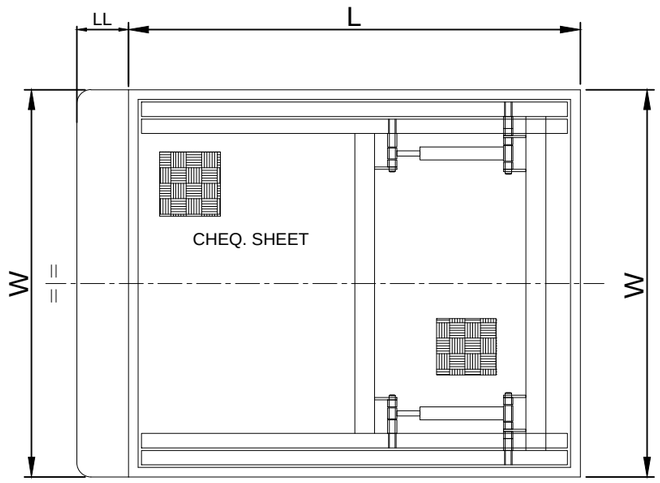



TOP VIEW

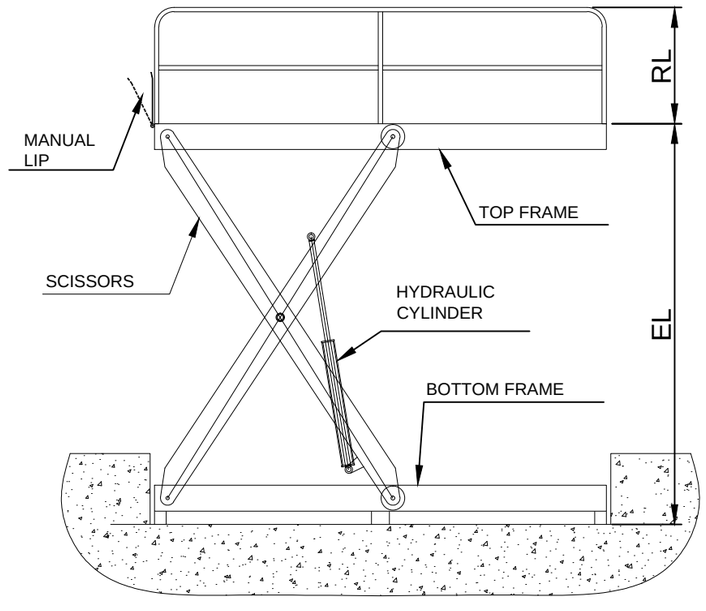

OPEN HEIGHT FRONT VIEW

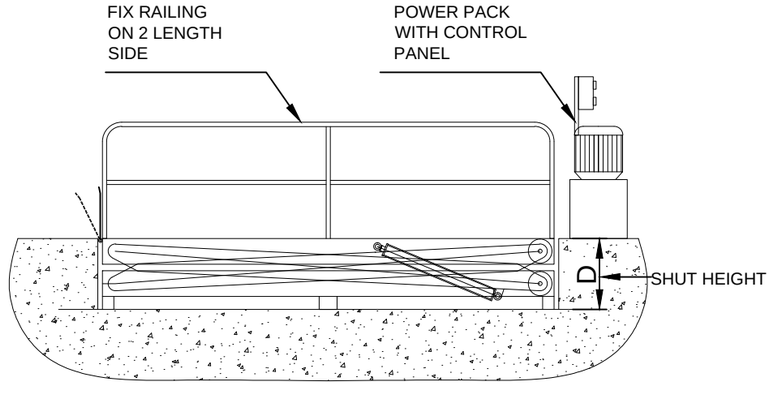

CLOSED HEIGHT FRONT VIEW

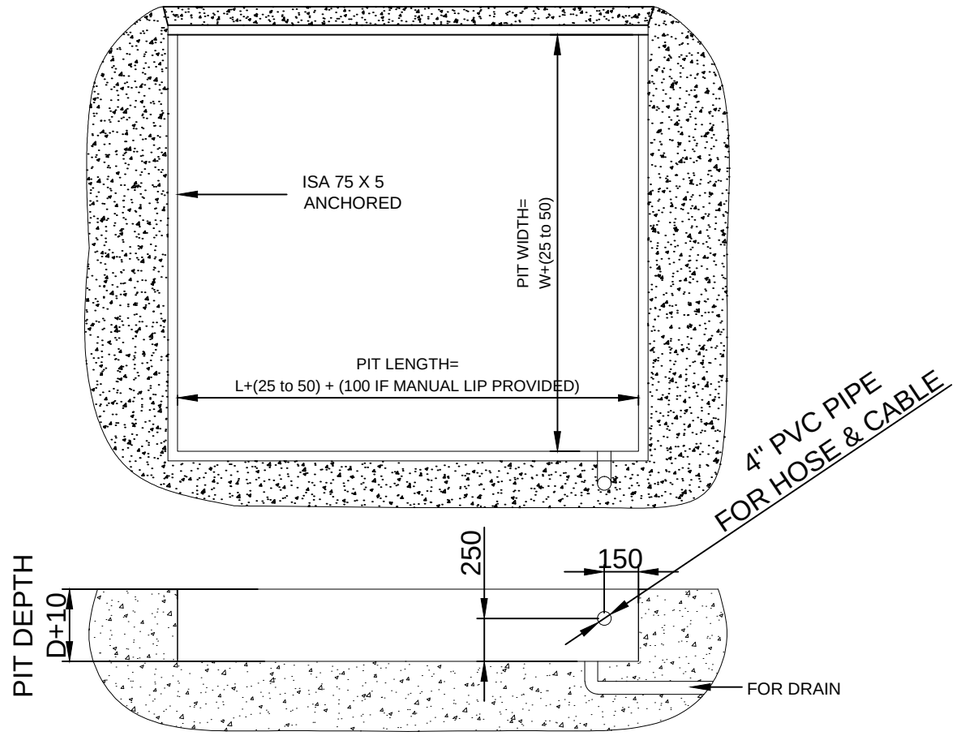

PIT DRAWING

NOTE :

1. PIT FOR SCISSORLIFT HAS TO BE DIAGONALLY WITHIN 3-5 MM
2. BASE OF THE PIT HAS TO BE IN WATER LEVEL AND RIGHT ANGLE TO THE VERTICAL SIDE WALLS
3. PROPER ARRANGEMENT FOR ROUTING HOSES AND CABLES HAVE TO BE MADE DEPENDING ON SITE CONDITIONS AND POSITION OF POWER PACK
4. COVERING REQUIRED FOR CABLES AND RELATED CIVIL WORK IS IN CLIENTS SCOPE
5. WATER DRAINAGE AND PIT CLEANING NEEDS TO BE CONSIDERED AND DONE BY CLIENT
6. PIT & ALL CIVIL WORK IS IN CLIENT SCOPE.
7. TOLERANCE ± 10 MM.

W	WIDTH
L	LENGTH
LL	LIP LENGTH
EH	EXTENSION HEIGHT
RH	RAILING HEIGHT
D	PIT DEPTH

Rev No.	Revision 00	Date:	Revised By :

This drawing & design is the property of NIHVA TECHNOLOGIES. Not to be sold or copied to any other concern.

TITLE:- PIT MOUNTED SCISSOR LIFT-STD

NIHVA TECHNOLOGIES PVT. LTD. PUNE
Tel : 020 66304033
Email:- info@nihva.com
Website:- www.nihva.com

	NAME	DATE	SIGN
DRAWN	G.PATIL	25/12/2021	
CHECK	A.KURHADE	25/12/2021	
APPRD.			

CLIENT -

LOCATION -

PRODUCT - SCISSOR LIFT STD

If any queries contact : design@nihva.com

DWG NO:-NIHVA\21-22\CLT\291 REV- 00

ALL DIMENSION ARE IN mm

SCALE: NTS SCALE:-- 1:1 SHEET: 01 OF 01