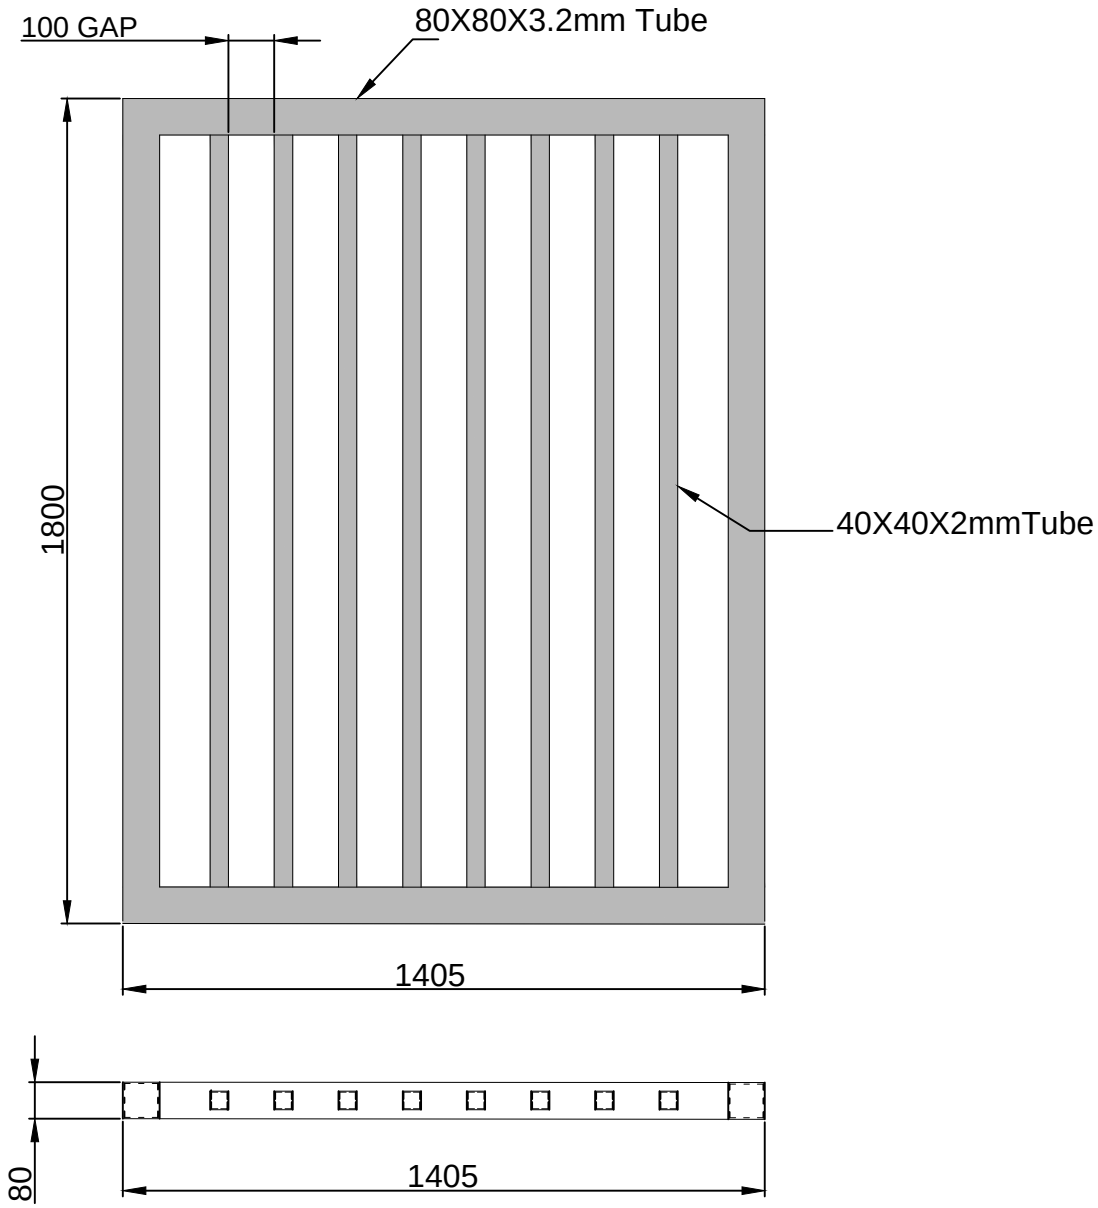

QTY :-01 NOS
MATERIAL: MS

DIMENSION :		
CLEAR WIDTH	CLEAR HEIGHT	QUANTITY
1500	1800	01

MATERIAL: MS

THICKNESS : 5mm

NIHVA TECHNOLOGIES
PVT. LTD. PUNE
Email:- info@nihva.com
Website:- www.nihva.com

TITLE:

WICKET GATE (6)

CLIENT'S APPROVAL :

CLIENT -

PROJECT -

SITE LOCATION -

DWG. NO. :-NIHVA/18-19/VDR/104

SCALE: NTS	WT:	SHEET:1 OF 1

DRAWN BY: SURAJ	30-08-2018	
CHECK BY : OMKAR	30-08-2018	
APPROVED BY : S.S	30-08-2018	

If any queries contact : projects@nihva.com

NOTE: ALL DIMENSIONS ARE IN mm

THIS DRAWING & DESIGN IS THE PROPERTY OF NIHVA TECHNOLOGIES. NOT TO BE SOLD OR COPIED TO ANY OTHER CONCERN.