
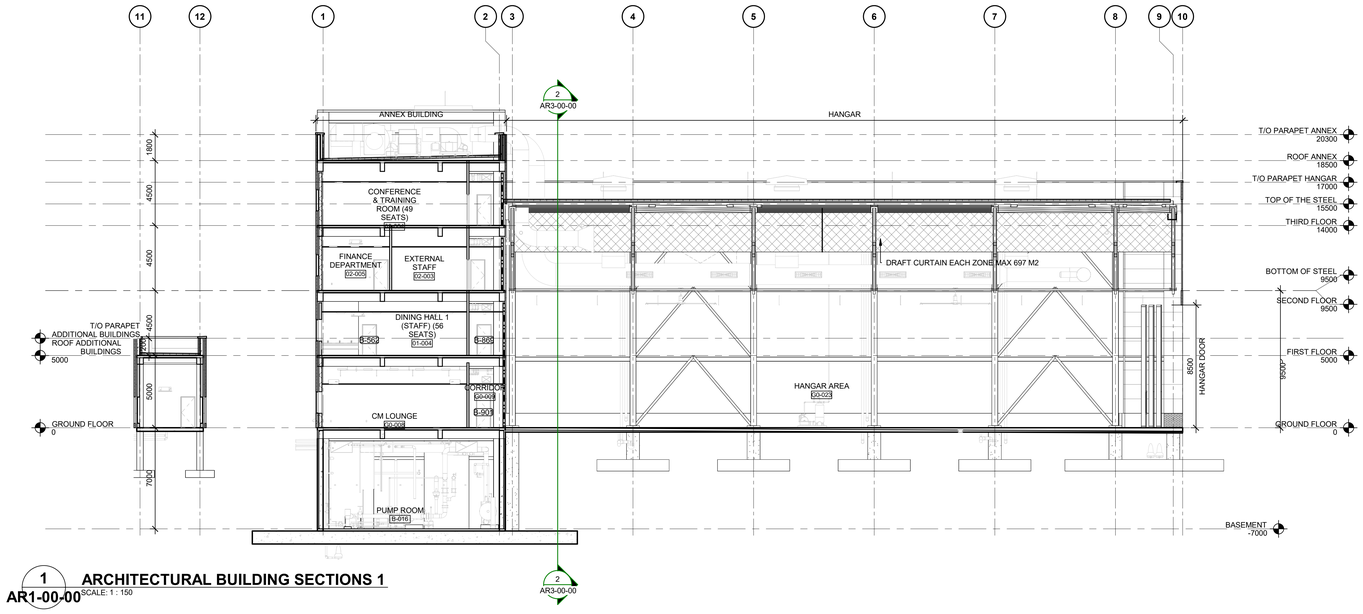


1 ARCHITECTURAL BUILDING SECTIONS 1
AR1-00-00 SCALE: 1 : 150

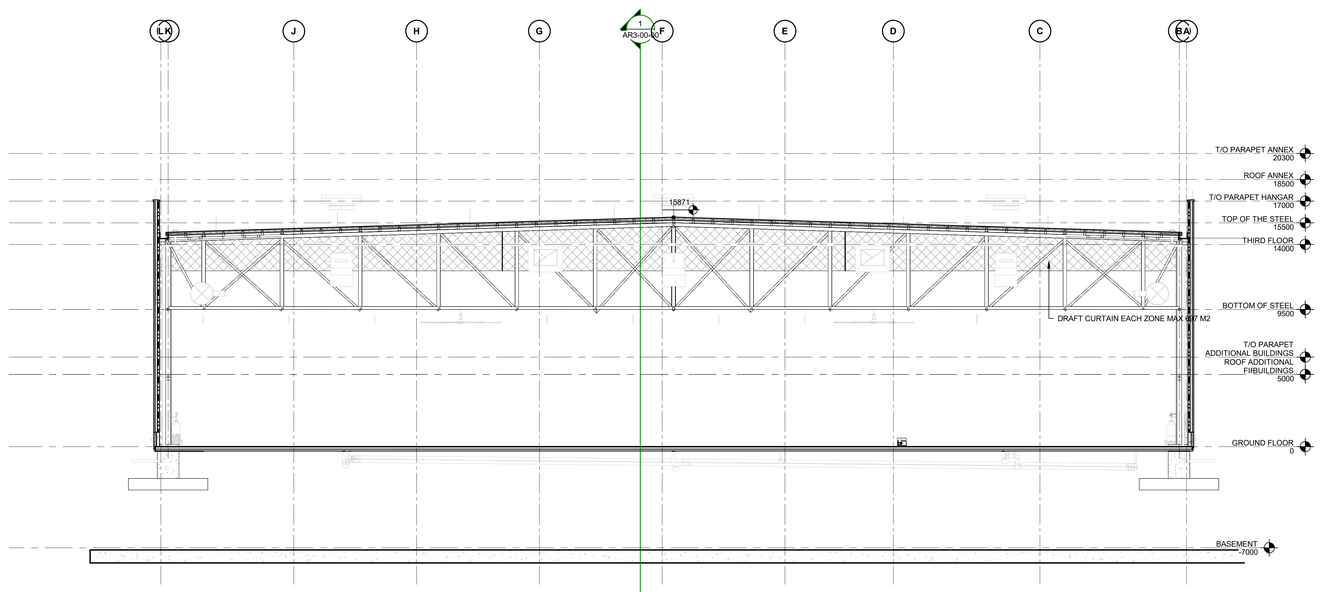

2 ARCHITECTURAL BUILDING SECTIONS 2
AR1-00-00 SCALE: 1 : 150

GHAFARI ASSOCIATES © 2020
25-07-2024 18:31:13

adani

AHMEDABAD INTERNATIONAL AIRPORT LTD
TERMINAL-1, BUILDING, 1ST FLOOR
SARDAR VALLABHBHAI PATEL INT. AIRPORT
AHMEDABAD 382475
GUJARAT, INDIA

GUJSAIL HANGAR
AHMEDABAD INTERNATIONAL AIRPORT
AHMEDABAD 382475
GUJARAT, INDIA

GHAFARI PUROHIT
Architects & Engineers Pvt. Ltd.

2ND FLOOR, 201 NOTUS PRIDE BUILDING
SARABHAI CAMPUS
VIKRAM SARABHAI ROAD
VADODARA - 390007
GUJARAT, INDIA
TEL +91.728.484.1670
www.ghafari.com

CONSULTANT INFORMATION

REGISTRATION SEAL

NOT FOR CONSTRUCTION

REV	DATE	DOC REL ## - DESCRIPTION
1	25/07/2024	ISSUED FOR PRE-BID MEETING PURPOSE

PROJECT #	2180003
PROJECT MANAGER	V. BAPAT
DESIGNED BY	M. PATTANI
DRAWN BY	M. PATTANI
QUALCHECK	N. PUROHIT

SHEET TITLE

ARCHITECTURAL BUILDING SECTIONS

AR3-00-00
SHEET NUMBER