

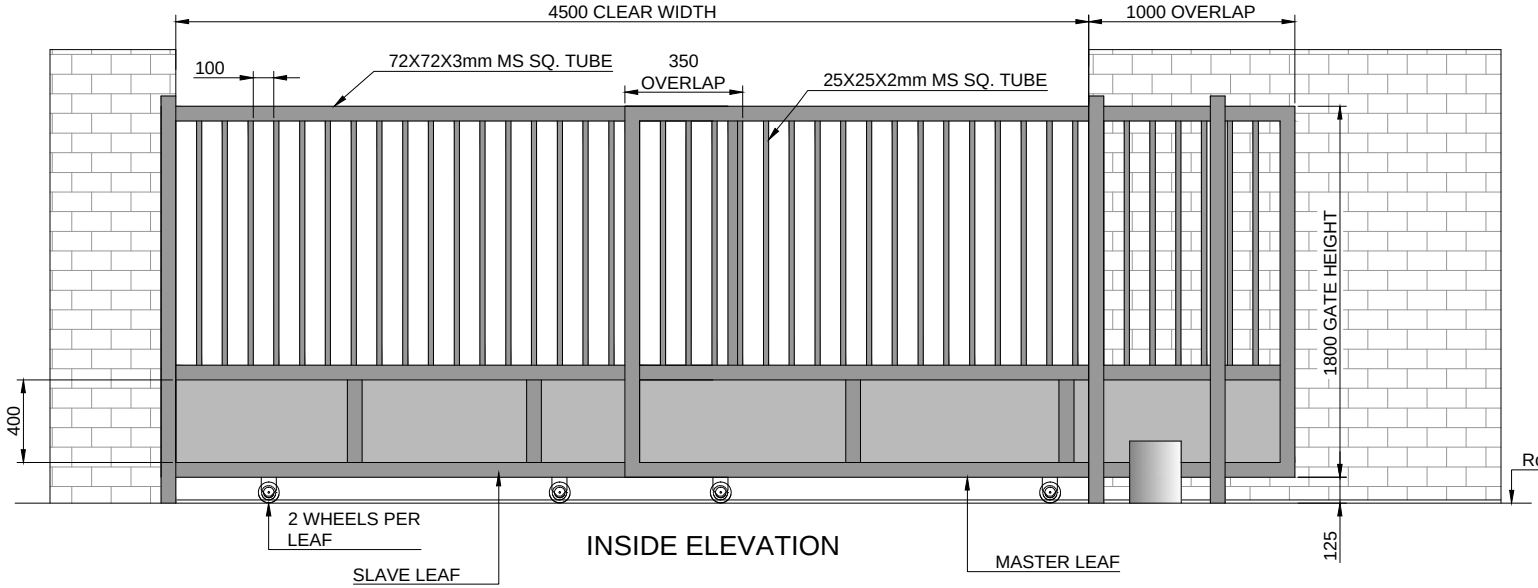



INSIDE ELEVATION

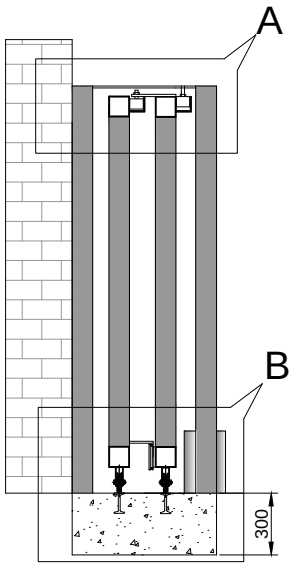


SIDE VIEW

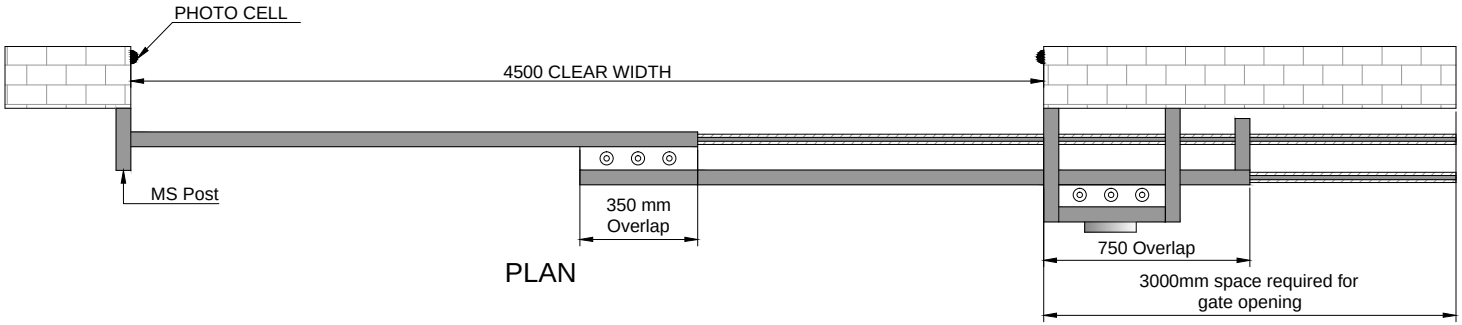

PLAN

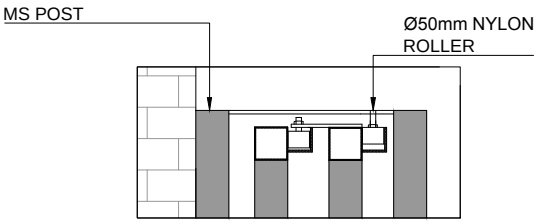

DETAILED VIEW A

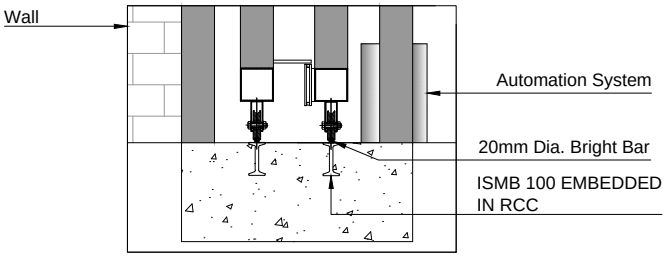

DETAILED VIEW B

This drawing & designing is the property of NIHVA TECHNOLOGIES. Not to be sold or copied to any other concern.

TITLE	3 LEAF TELESCOPIC GATE 15000X1800mm	
	SIGN	DATE
DRAWN	OMKAR	14/03/17
CHECKED	SAGAR P.	14/03/17
REV.		
APPROVED	R.K.	14/03/17
If any queries contact : projects@nihva.com		
ALL DIMENSION ARE IN mm		

NIHVA TECHNOLOGIES PVT. LTD. PUNE
Tel : 020 66304033
Email:- info@nihva.com
Website:- www.nihva.com

CLIENT - SHIMZU CORPORATION INDIA PVT.LTD.		
PROJECT - GSK		
SITE - KOLAR, KARNATAKA		
DWG. NO. : NIHVA/16-17/177		
SCALE: NTS	WT:	SHEET: 01 OF 01