
LEGEND	NEW COLUMN 01 230 X 450	NEW COLUMN 02 150 X 450	BEAM - 230 X 450 - 230 X 300	LINTEL PROJECTION 450MM WIDE	TOTAL BUILT UP AREA 2556.00 SQ.M.

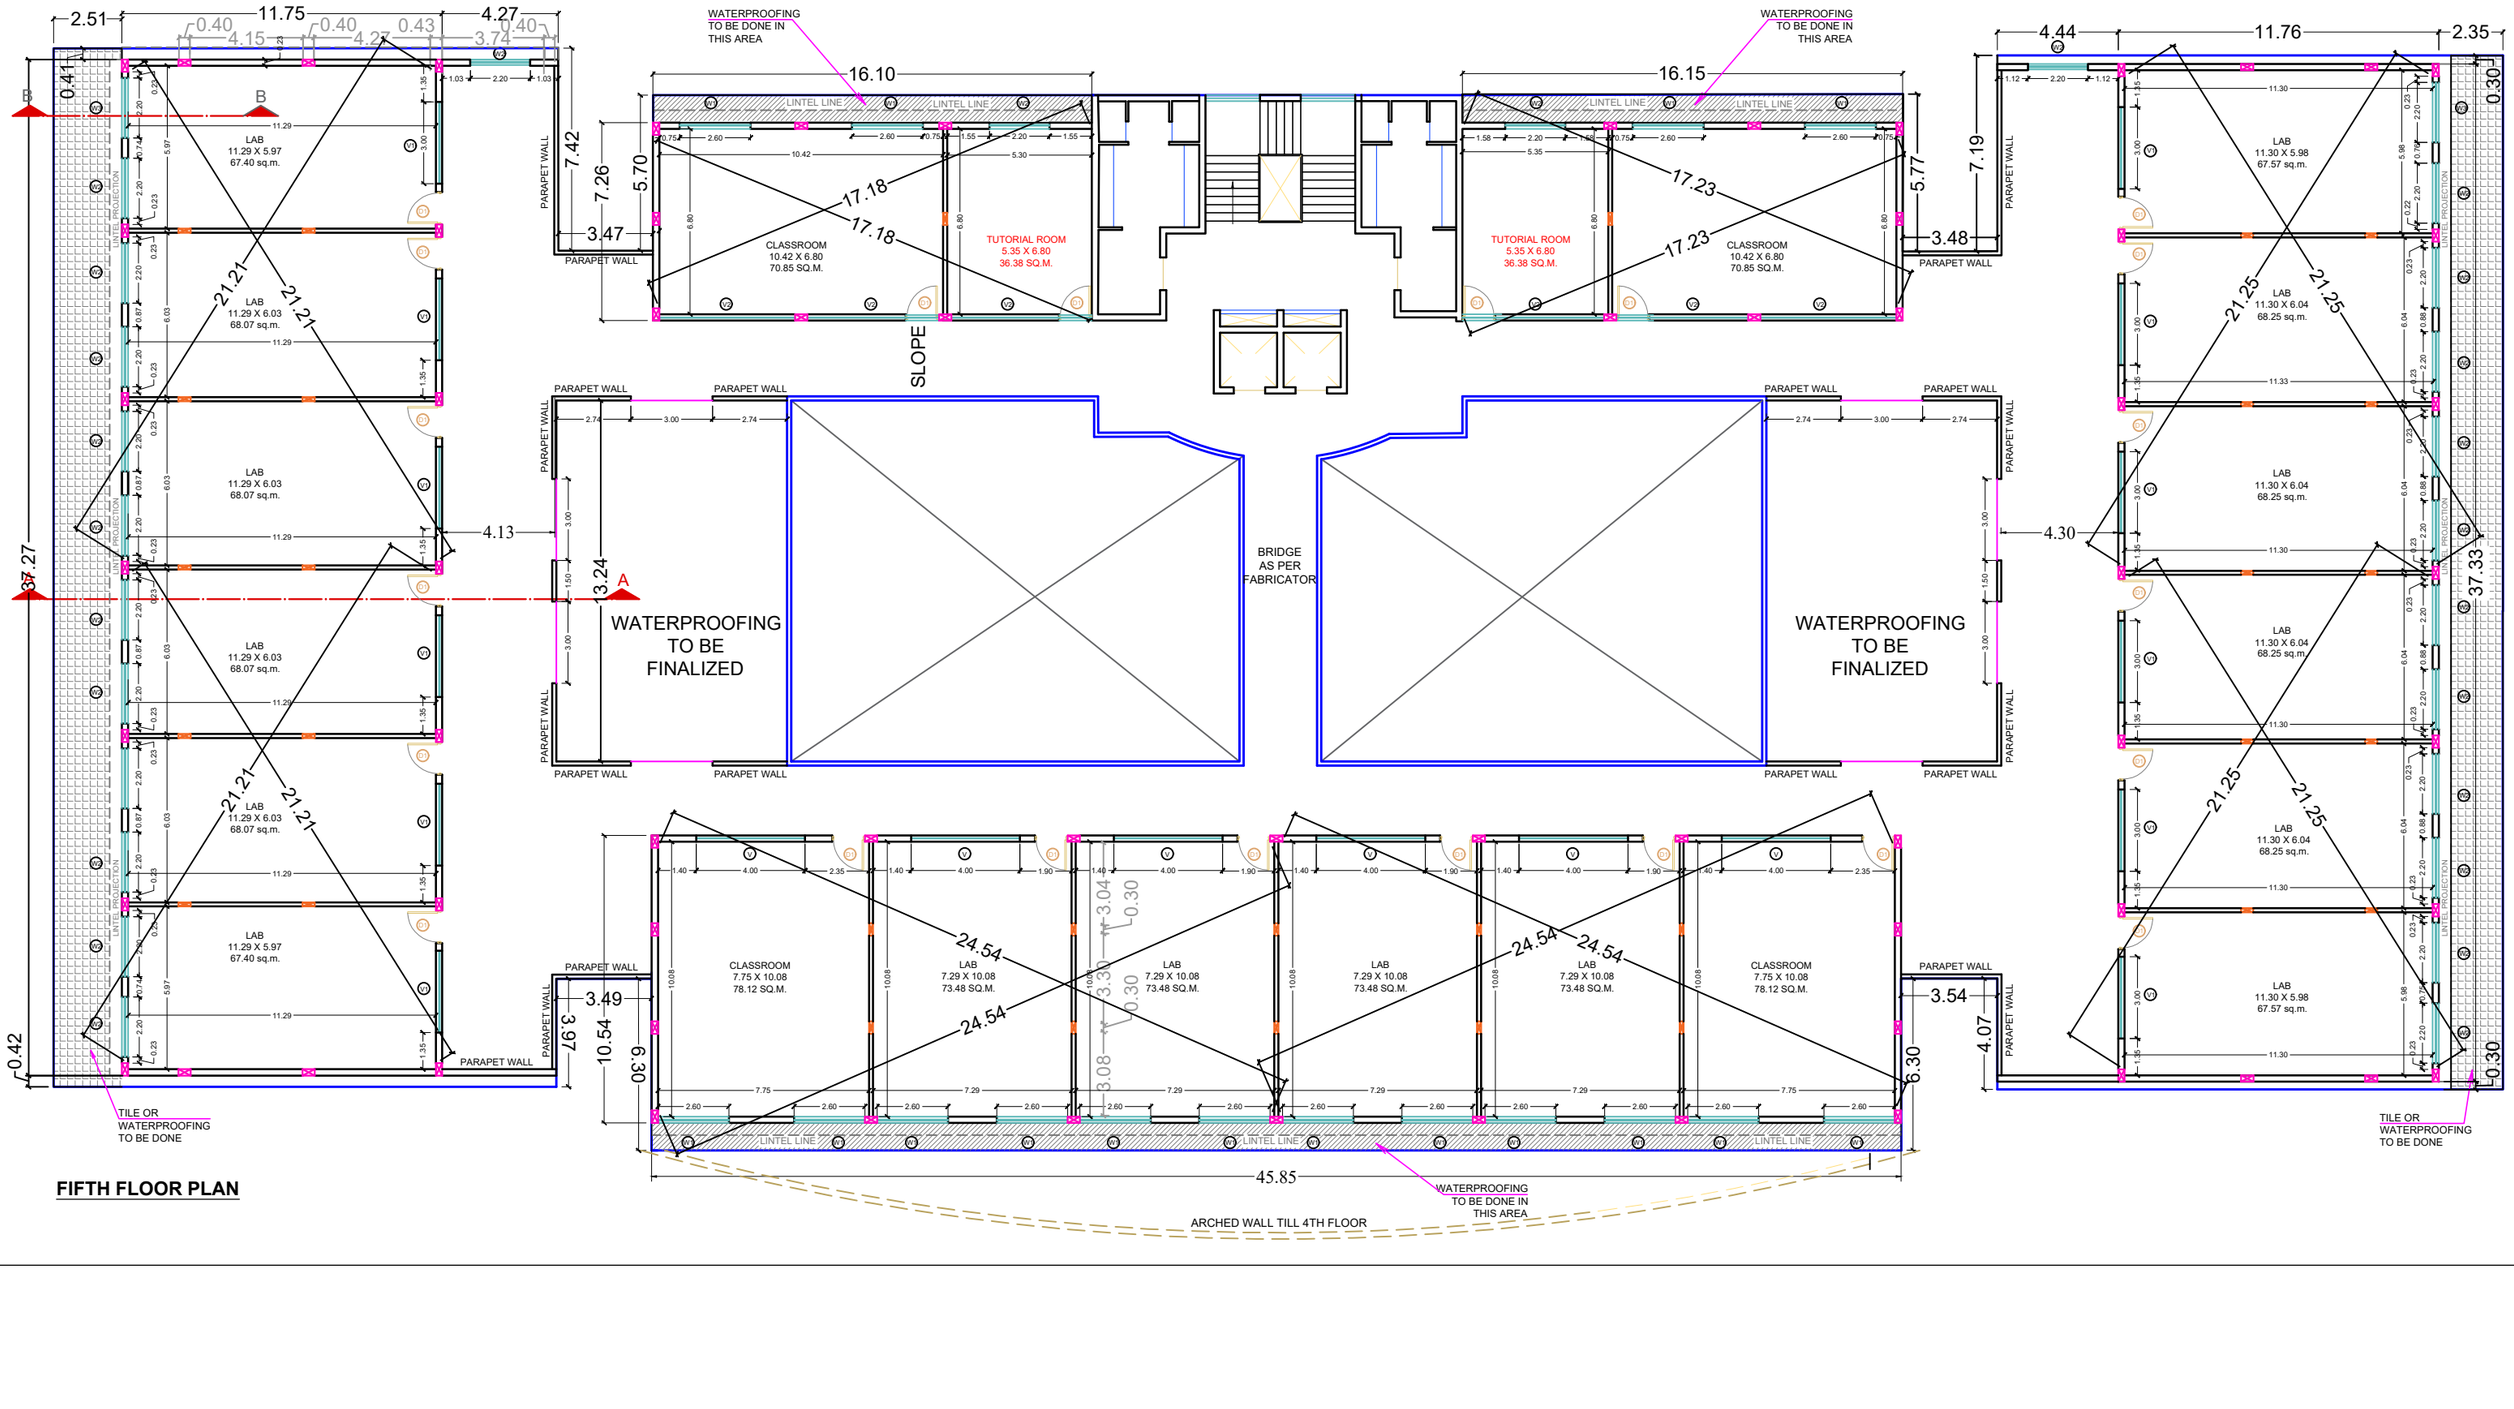

FIFTH FLOOR PLAN