


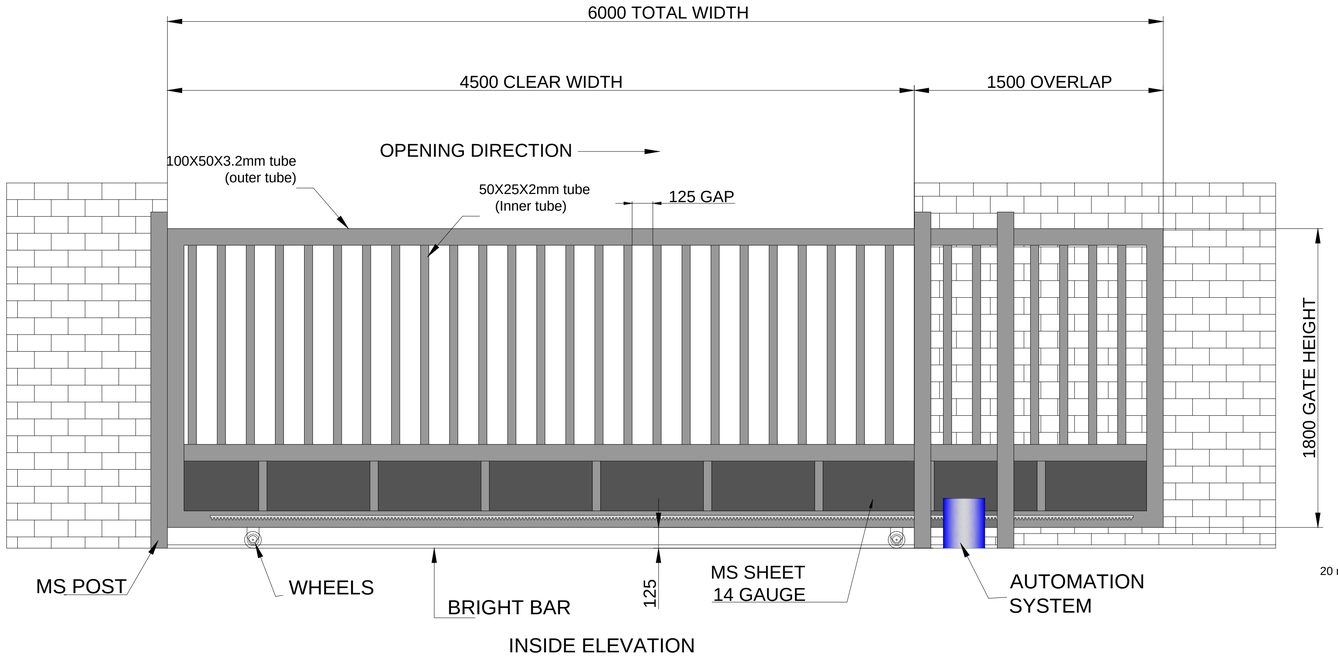


INSIDE ELEVATION

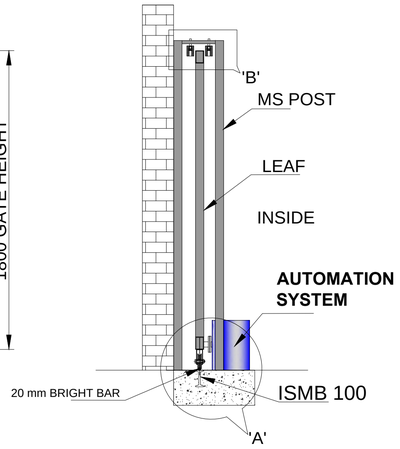


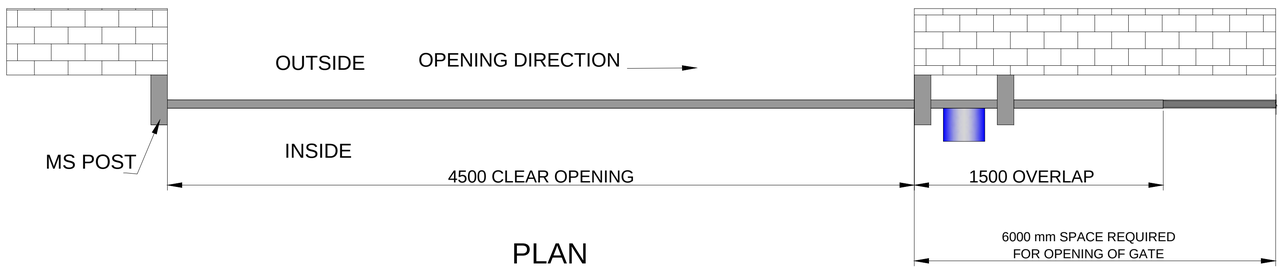

PLAN

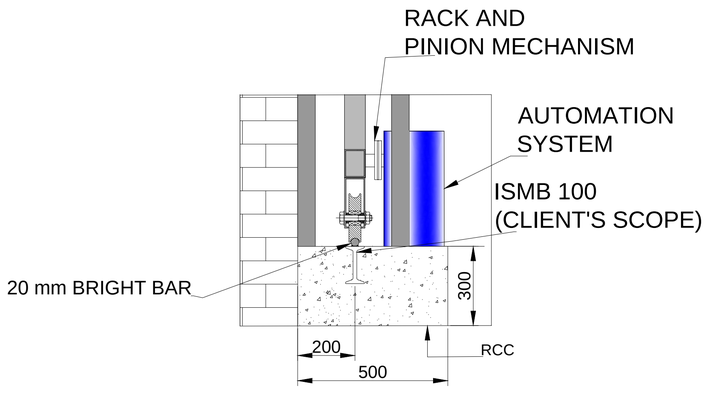

DETAIL VIEW OF A

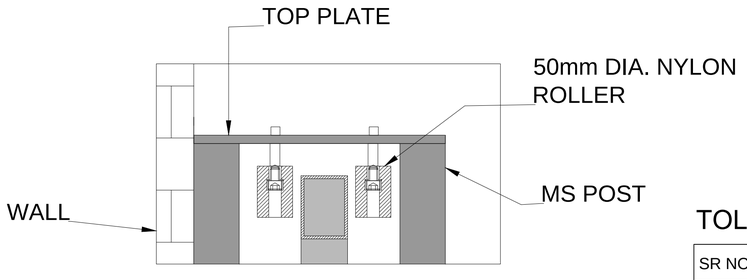

DETAIL VIEW OF B

TOLERANCE- ±10mm

SR NO	TUBE SPECIFICATION	
1	100X50X3.2mm	OUTER FRAME
2	50X25X2mm	INNER PATTERN
3	100X50X3.2mm	FOR MS POST

TOTAL NO OF POST ARE 3

DIMENSION :

CLEAR WIDTH	CLEAR HEIGHT	QUANTITY
4500mm	1800mm	1 NOS

MATERIAL:

THICKNESS :

NOTE-
1. ALL REQUIRED CIVIL WORK WILL BE IN CLIENTS SCOPE.
2. ONE COAT OF RED OXIDE & TWO COAT OF APPROVED RAL SHADE WILL BE GIVEN TO THE GATE.

NIHVA TECHNOLOGIES PVT. LTD.
NIHVA TECHNOLOGIES PVT. LTD. PUNE
Email:- info@nihva.com
Website:- www.nihva.com

TITLE:

AUTOMATIC SINGLE LEAF SLIDING GATE

CLIENT'S APPROVAL :

CLIENT -ERICSSON INDIA PVT. LTD.

PROJECT -

SITE LOCATION -CHAKAN,PUNE

DWG. NO. : NIHVA/17-18/0195

SCALE: NTS	WT:	SHEET:1 OF 1
DRAWN BY: SURAJ		DATE: 01-09-2017
CHECK BY : SAGAR P		DATE: 01-09-2017
APPROVED BY : SHEKHAR		DATE: 01-09-2017

If any queries contact : projects@nihva.com

NOTE: ALL DIMENSIONS ARE IN mm

THIS DRAWING & DESIGN IS THE PROPERTY OF NIHVA TECHNOLOGIES. NOT TO BE SOLD OR COPIED TO ANY OTHER CONCERN.