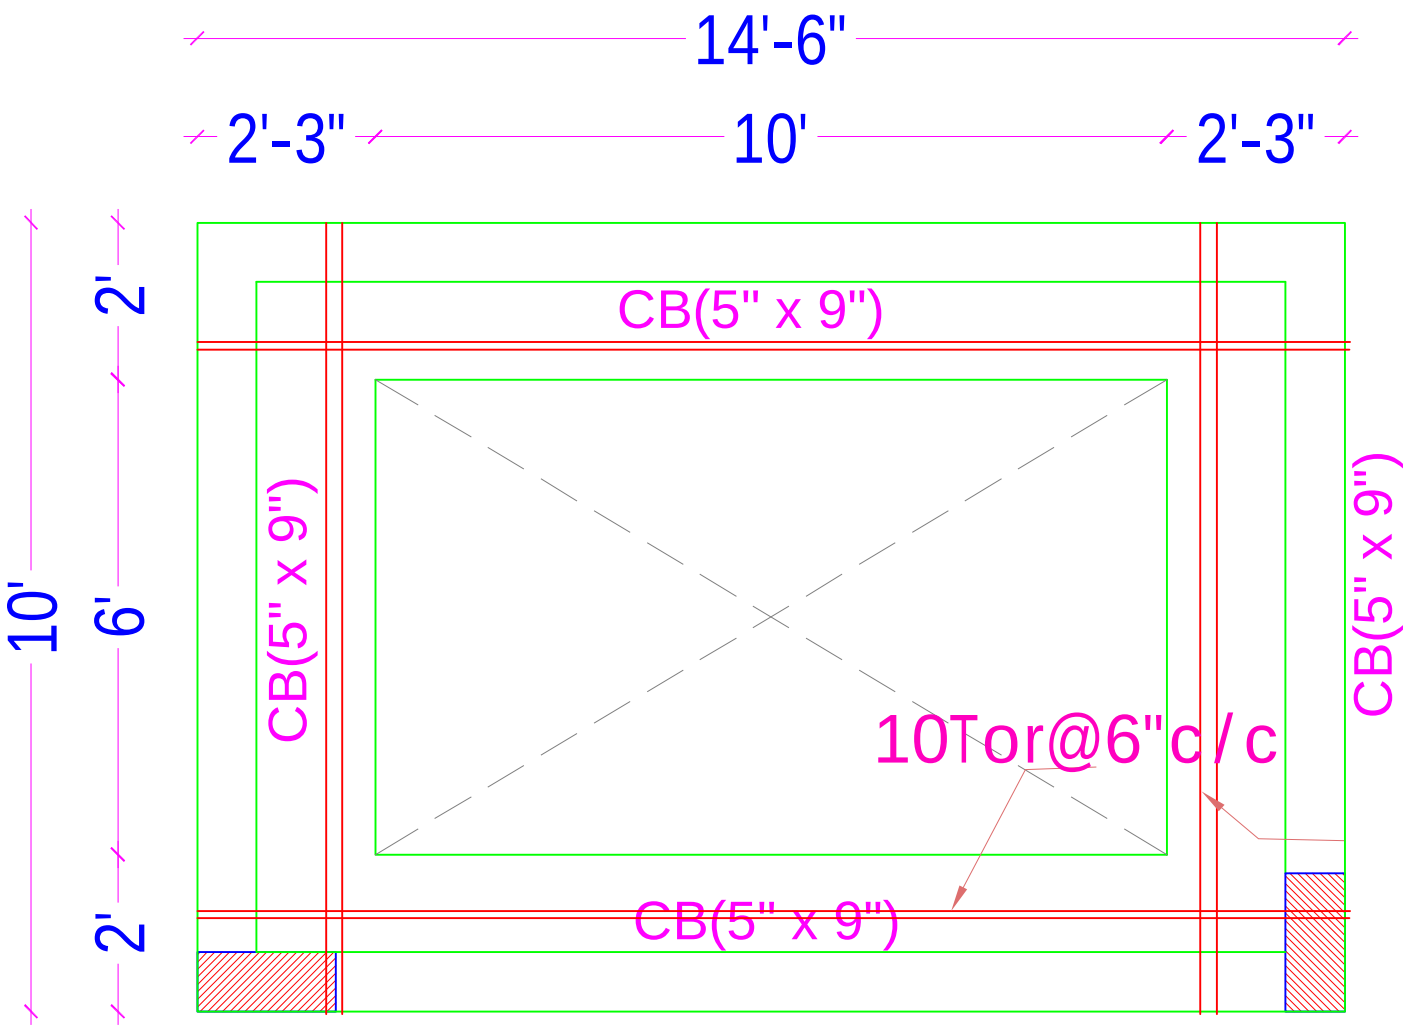


PROJECT TITLE

PROPOSED DUPLEX RESIDENCE FOR SRI SAI RAMI REDDY @ KURNOOL.

DRAWING TITLE

SKYLIGHT DETAILS

TOT FLOORS: (G+3)

DRAWN BY: Chiranjeevi

SHEET NUM: A-08

CHKD BY:

SCALE: N.T.S

AREA STATEMENT

SITE AREA	: 1800.00 S.ft
	: 167.28 S.qm

PLINTH AREAS

GROUND FLOOR	:	1404.00 S.ft
FIRST FLOOR	:	1404.00 S.ft
SECOND FLOOR	:	1404.00 S.ft
THIRD FLOOR	:	671.72 S.ft

DATE: 05-04-2021

NOTE

(1)THIS DRAWING IS THE PROPERTY OF STHAPATHI ARCHITECTS & ENGINEERS, OFFICE ADD:43-128J,SRINIVASA NAGAR, KURNOOL IT IS NOT ALLOWED TO REPRODUCE ITS CONTENTS IN ANY FORM EXCEPT FOR THE PURPOSE FOR WHICH IT IS INTENDED.
(2) THIS DRAWING IS NOT TO BE SCALED, WRITTEN DIMENSIONS ONLY ARE TO BE CONSIDERED.
(3) ANY DISCREPANCIES ARE TO BE BROUGHT TO THE NOTICE OF THE

STHAPATHI
ARCHITECTS & ENGINEERS
43/128-J, SRINIVAS NAGAR
KURNOOL, PH NUM: 225441