

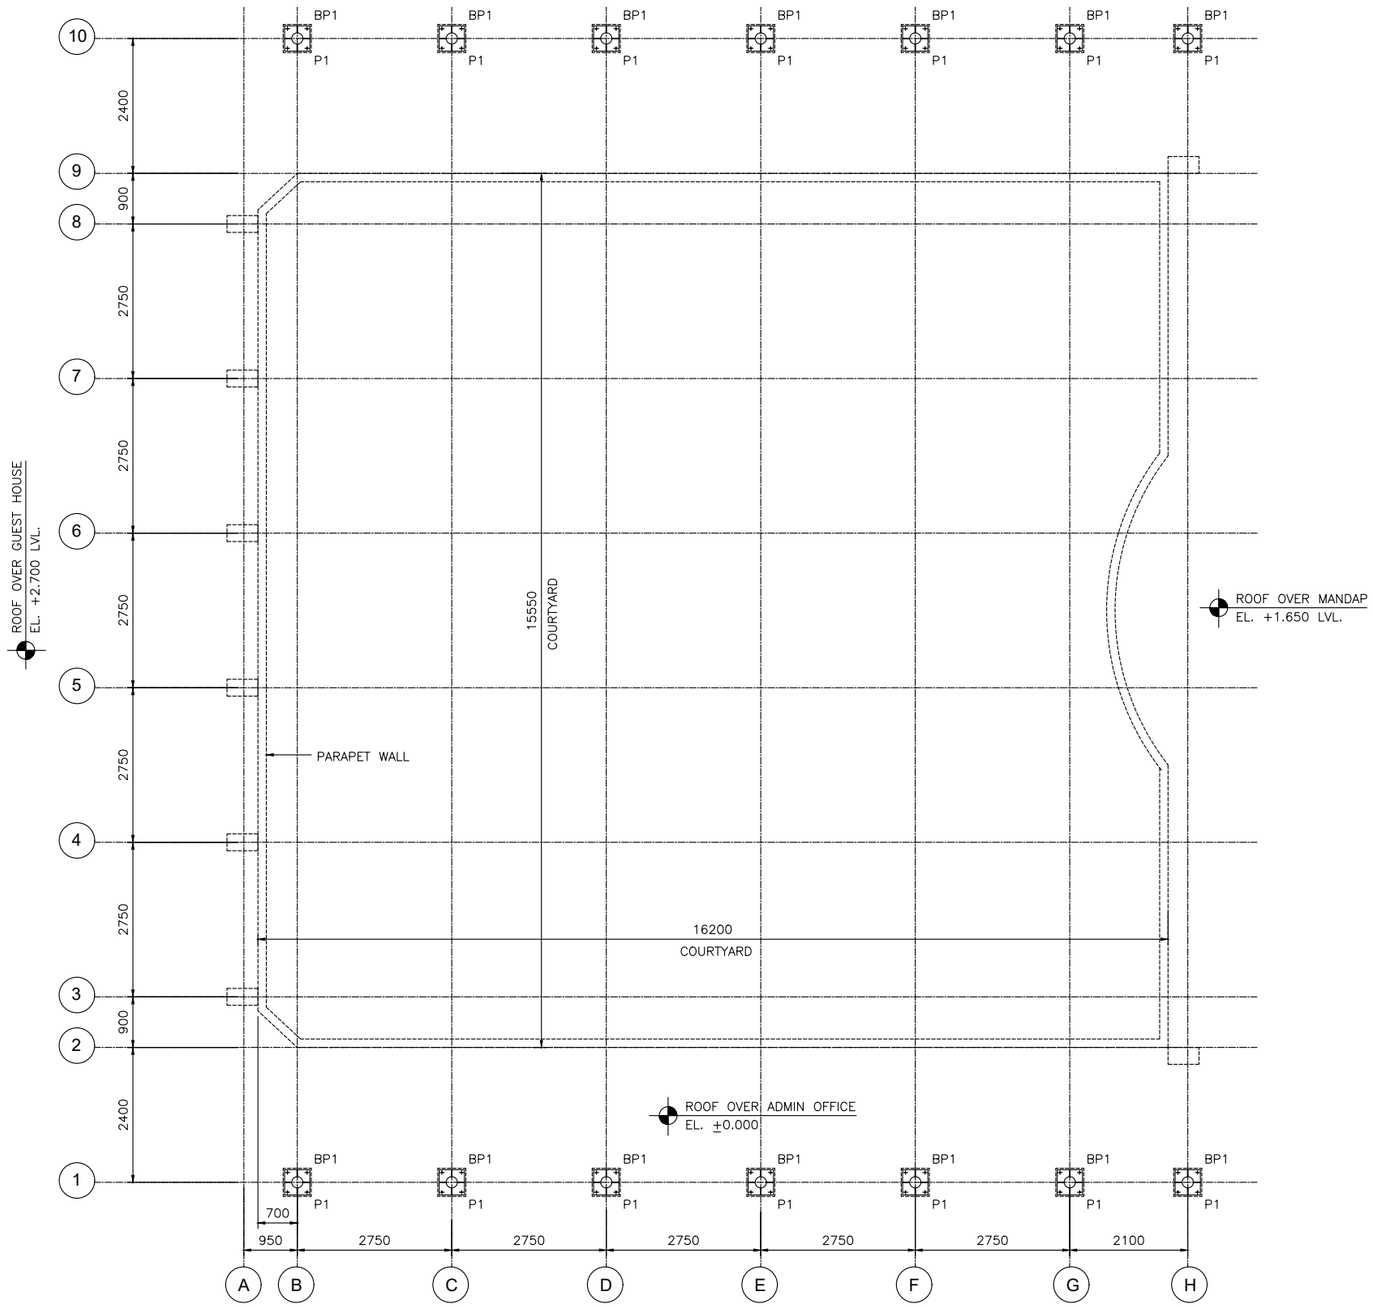



BASE PLATE LAYOUT
SCALE 1:50

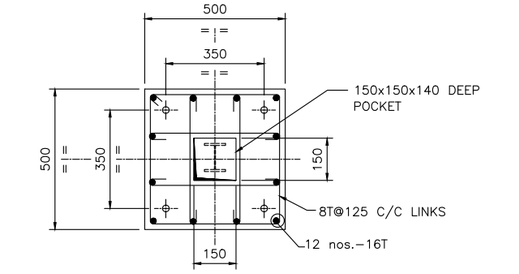

SECTION B-B
SCALE 1:25

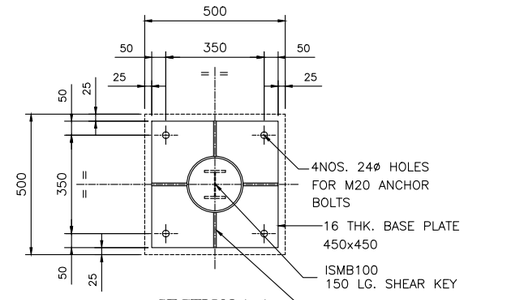

SECTION A-A
SCALE 1:25

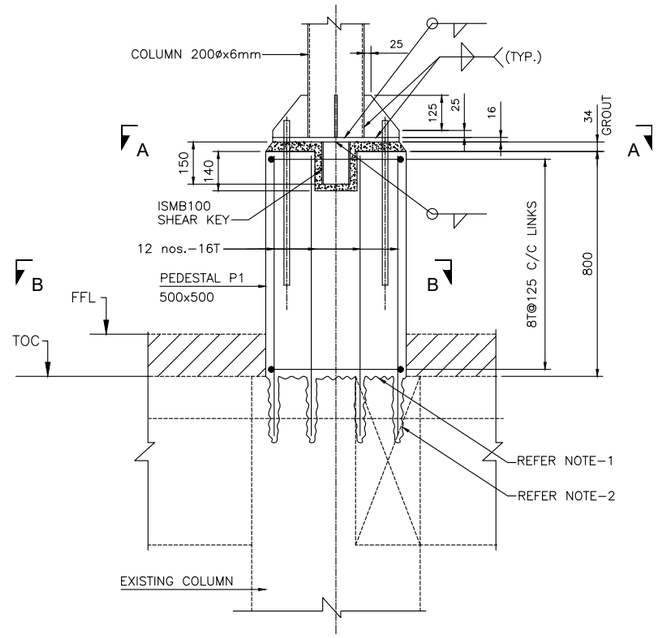

PEDETSAL P1 DETAIL
SCALE 1:25

NOTES FOR STEEL WORK:

1. ALL PLATES ARE 8mm THK. UNLESS NOTED
2. ALL HOLES ARE 18mm DIA FOR 16mm DIA BOLTS U.N.O.
3. ALL SHOP WELDS ARE 6mm FILLET MIN. AND SITE WELDS ARE 8mm FILLET MIN. U.N.
4. ALL INCLINED DIMENSIONS TO BE CHECKED AT SHOP/SITE BY FULL SCALE LAYOUT BEFORE FABRICATION OF STRUCTURAL STEEL WORK
5. RECTANGULAR HOLLOW SECTIONS (RHS) & SQUARE HOLLOW SECTIONS (SHS) USED SHALL BE 'TATA STRUCTURA' MANUFACTURED BY TATA STEEL. GRADE OF STEEL SHALL BE YST 310. STRUCTURAL HOLLOW SECTIONS SHALL CONFIRM TO IS : 4923 & IS : 1161.
6. ONLY ADVANI–ORIEKON ELECTRODES SHALL BE USED FOR WELDING WORK. METAL BOND OR OVERCHORD ELECTRODES SHALL BE USED.
7. WELDING SHALL BE DONE BY QUALIFIED WELDERS ONLY.
8. GRINDING OF EXTRA WELDS SHALL BE DONE TO HAVE UNIFORM CONVEX WELD FINISH.
9. ALL STRUCTURAL MEMBERS SHALL BE TREATED BY SHOT BLASING AND WITH ONE COAT OF EPOXY PAINT, AT SITE AFTER COMPLETING ERRECTION, WELDING AND GRINDING WORK, TWO COATS OF FINAL EPOXY PAINT SHALL BE APPLIED

GENERAL NOTES

1. ALL DIMENSIONS ARE IN MILLIMETERS (MM) & LEVELS IN METERS.
2. READ IN CONJUNCTURE WITH ARCHITECTURAL DWG. FOR ALL DIMENSIONS & LEVELS
3. IN CASE OF ANY DESCRIPANCY OR DOUBTS, CLARIFY PRIOR TO FABRICATION.
4. DO NOT SCALE DRAWING FOLLOW ONLY WRITTEN DIMENSIONS.

DRAWINGS

REV	DRAWN BY & DATE	CHECKED BY & DATE	APP/AUTH BY & DATE	REVISION
06				
05				
04				
03				
02				
01				
00	SM 26.03.2024	DJB 26.03.2024	DJB 26.03.2024	RELEASE FOR CONSTRUCTION

THIS DRAWING IS VALID ONLY IF SIGN IN ORIGINAL

ISCKON - COURTYARD

PROJECT

ARCHITECT :

TITLE : BASE PLATE LAYOUT AND DETAIL

SCALE : –

CAD FILE : ST–01

DRG.NO. : ST–01

REV 0

HDB DESIGN SERVICES
CONSULTING STRUCTURAL ENGINEER
2/40, JUHU GULMOHAR CO–OP HSG. SOCIETY,
GULMOHAR ROAD, JUHU SCHEME, MUMBAI – 400 049.