






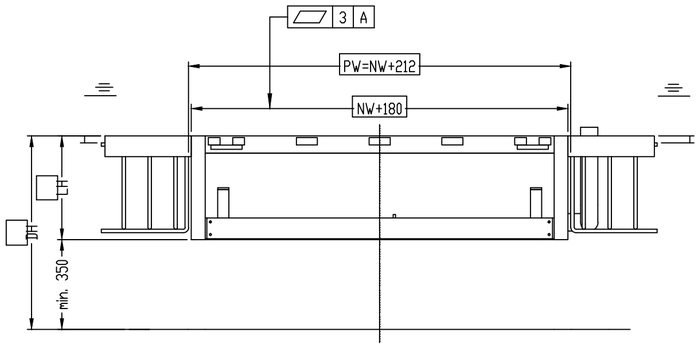


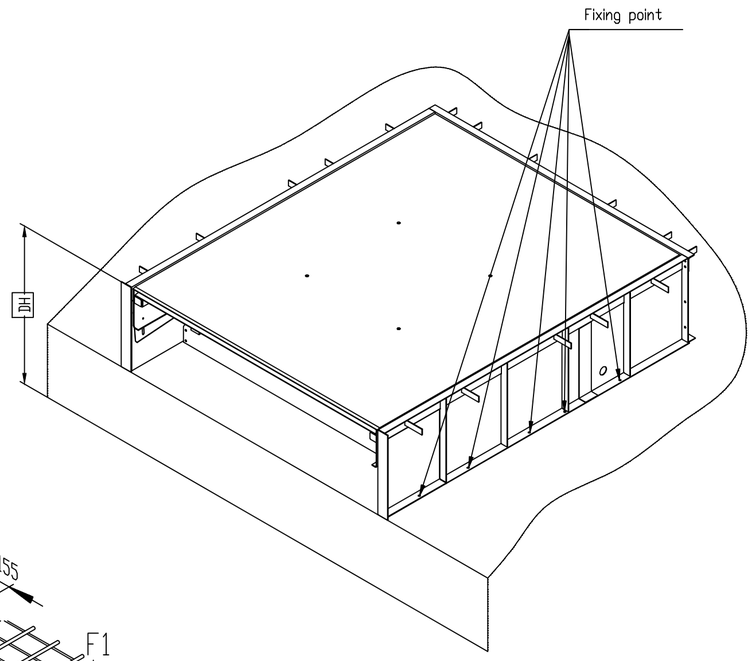


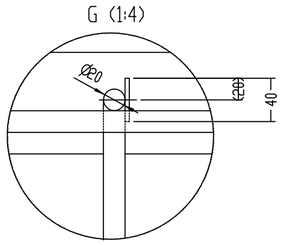

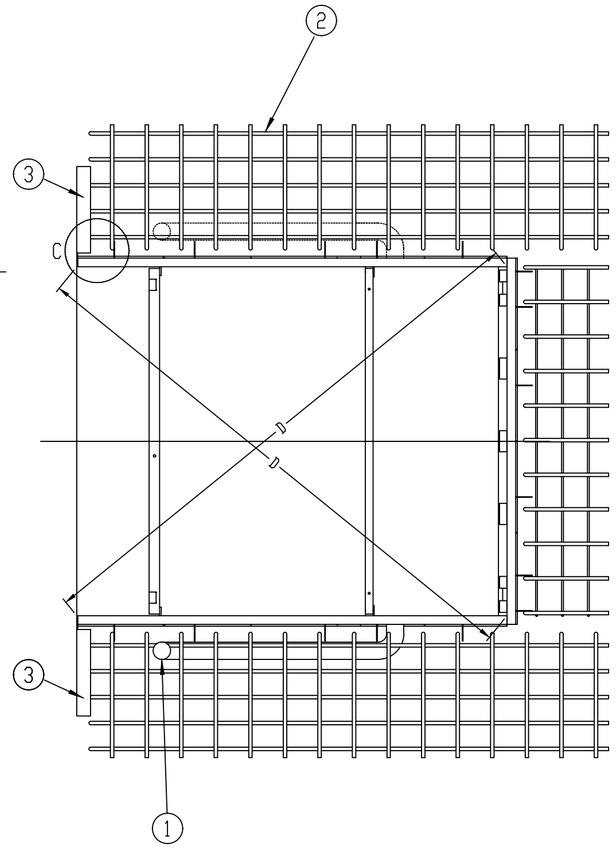

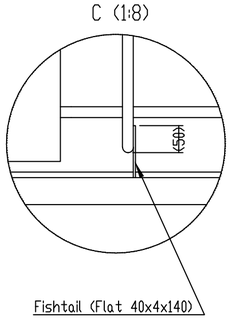

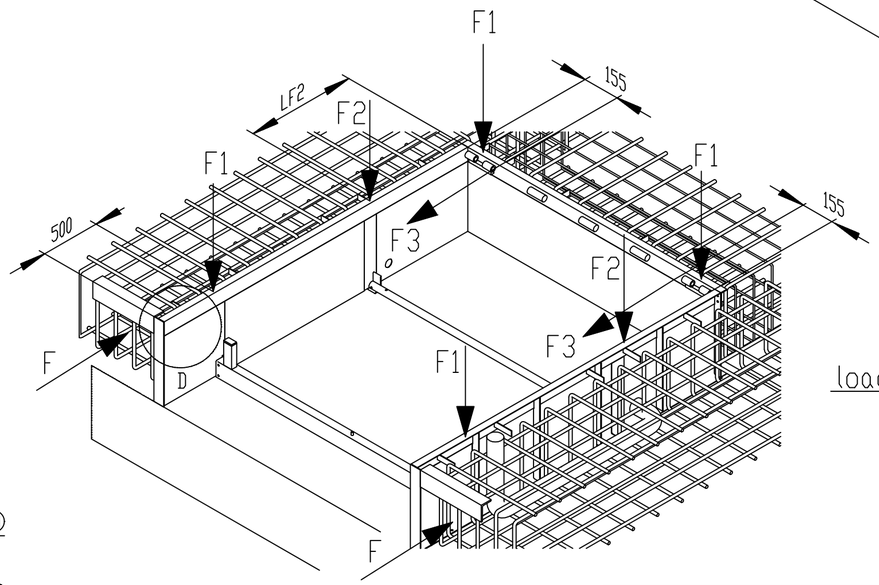

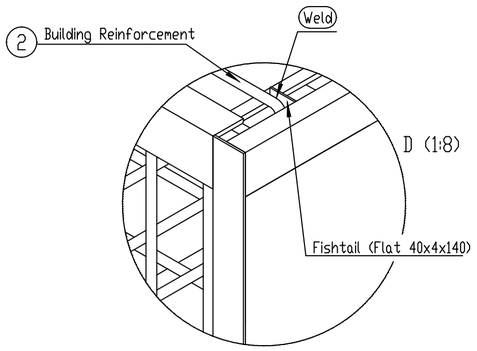

NL	3000
NW	2000
PL	3086
PW	2212
LH	600
e	2107
LF2	980

load

F = The horizontal impact load F (100kN) must be absorbed by the structure, recommended according to DIN 1055-9
F1 = 57 kN (cross traffic position)
F2 = 42 kN (emergency stop)
F3 = 12 kN (brake force)

DH = Dock height
OK-FF= Finish floor level
OK-H = Yard level
PL = Pit length
PW = Pit width
NL = Nominal length
NW = Nominal width
LH = Leveller height

by others
(1) Conduit for wiring internal diameter min.70mm, angles < 45° (Left/right, acc. specification of sales company)
(2) Reinforcement (e.g. ø20)
(3) Steel profile, e.g. angle 120x80x10

Attention
- All dimension have a maximum tolerance of ± 5, unless specified
- Diagonals must be equal
- The frame walls must be vertical
- The preperation of the pit by others

It is forbidden by law to copy, duplicate this document, to transmit it to any third party or to misuse it in any way. The drawing remains our property and is to be returned immediately after use.

General tolerance EN ISO 13920-BF

Index	Modification	Date	Name

	Date	Name
Drawn	16.03.2015	bra
Released		
Blocked		
Archived		

ASSA ABLOY
ASSA ABLOY Entrance Systems

Version: 2
Material:
Printed:
Semifinished product:
Scale: 1 : 25
Weight:
Subject: DL6020T/DL6120T TD type B without Tail lift
Drawing Number: 5143.0269
Sheet: 1
1 Sheets
Replaced by:
Format: A2