




SECTION E
SCALE 1:4

SECTION E

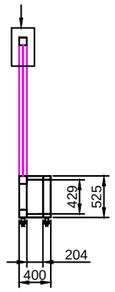


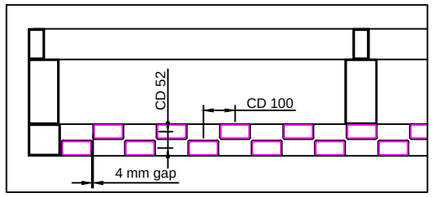


SECTION D
SCALE 1:4

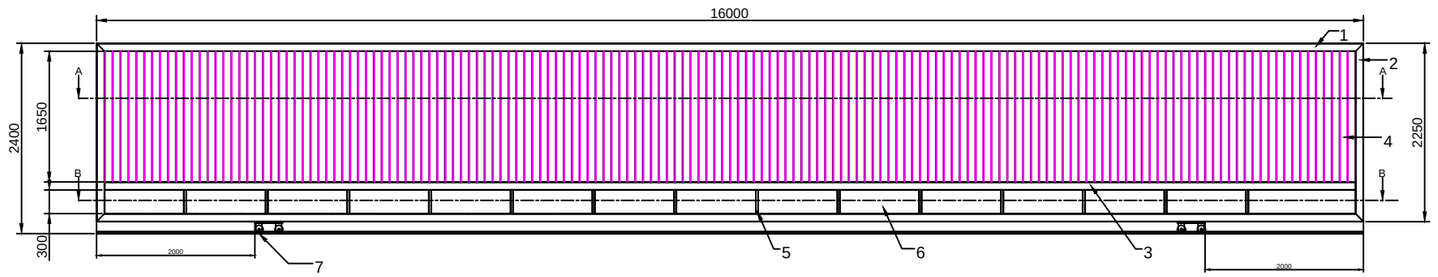


SECTION D

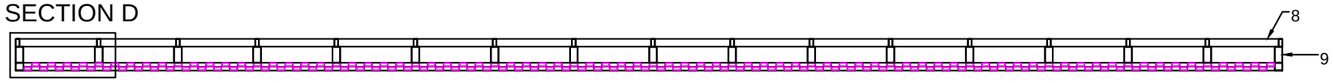

SECTION A-A

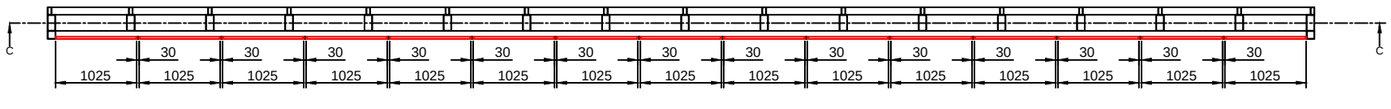

SECTION B-B

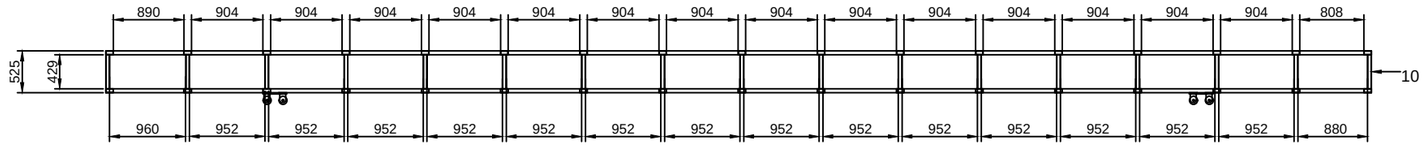

SECTION C-C

SR. NO.	DESCRIPTION	SPECIFICATION	QTY
1	SQ. TUBE	100 X 100 X 4, 16000 LENGTH	2 NOS
2	SQ. TUBE	100 X 100 X 4, 2250 LENGTH	2 NOS
3	SQ. TUBE	100 X 100 X 4, 15800 LENGTH	1 NOS
4	RECT. TUBE	96 X 48 X 3.2, 1650 LENGTH	158 NOS
5	SQ. TUBE	32 X 32 X 2.6, 300 LENGTH	14 NOS
6	MS PERFORATED TRAY	1015 X 298 X 29, 1.5 THK	15 NOS
7	WHEEL	4" WHEEL WITH BRACKET	4 SET
8	RECT. TUBE	96 X 48 X 3.2, 16000 LENGTH	2 NOS
9	RECT. TUBE	96 X 48 X 3.2, 204 LENGTH	34 NOS
10	RECT. TUBE	96 X 48 X 3.2, 429 LENGTH	17 NOS

NOTE: This drawing is for latest revised gate size 14000 CW x 2400 CH

This drawing & design is the property of NIHVA TECHNOLOGIES. Not to be sold or copied to any other concern.

TITLE
MOTORIZED SLIDING GATE FRAME

	NAME	SIGN	DATE
DRAWN	G.P.		11.03.22
CHECK	A.K.		11.03.22
APPRD.	V.T.		11.03.22

If any queries contact : design@nihva.com

ALL DIMENSION ARE IN mm

NIHVA
NIHVA TECHNOLOGIES PVT. LTD.

NIHVA TECHNOLOGIES PVT. LTD. PUNE
Tel : 020 66304033
Email:- info@nihva.com
Website:- www.nihva.com

CLIENT - SRF
LOCATION - PITHAMPUR
PRODUCT - MOTORIZED SLIDING GATE
NIHVA\21-22\MFG\041 | REV- 00
SCALE: NTS | SHEET: 01 OF 01