THIS DRAWING & DESIGN IS THE SOLE PROPERTY OF VMS & SHALL NOT BE COPIED, TRACED OR REPRODUCED BY ANY MEANS WITHOUT PRIOR WRITTEN CONSENT OF THE FIRM.

GENERAL NOTES :


1. ALL THE DIMENSIONS ARE UNFINISHED DIMENSIONS.
2. ALL DIMENSIONS ARE IN MILLIMETERS, RL IN METERS UNLESS OTHERWISE MENTIONED.
3. ALL THE DIMENSIONS SHALL BE READ & NOT TO BE MEASURED.
4. IN CASE OF ANY DISCREPANCY, BRING IT TO THE NOTICE OF THE ARCHITECT IMMEDIATELY.
5. DETAIL DRAWING PRECEDES THE GENERAL DRAWING.

STANDARD DRAWING SYMBOLS:


- FINISHED LEVEL / UNFINISHED LEVEL
- SECTION SYMBOL, UPPER HALF INDICATES DIAGRAM NO. LOWER HALF INDICATES IN DRAWING SHEET & LOWER HALF INDICATES DRAWING NO.
- ELEVATION SYMBOL, UPPER HALF INDICATES DIAGRAM NO. IN DRAWING SHEET & LOWER HALF INDICATES DRAWING NO.
- WINDOW SYMBOL, UPPER HALF INDICATES WINDOW NO. & LOWER HALF INDICATES DRAWING NO.
- DOOR SYMBOL, UPPER HALF INDICATES DOOR NO. & LOWER HALF INDICATES DRAWING NO.

GRAPHIC LEGEND :


- MASONRY CUT IN PLAN/SECTION.
- RCC COLUMN CUT IN PLAN.

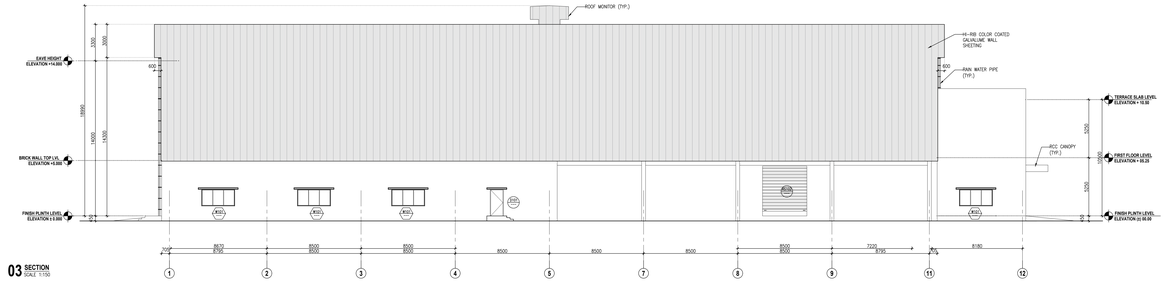


03 SECTION
SCALE 1:150

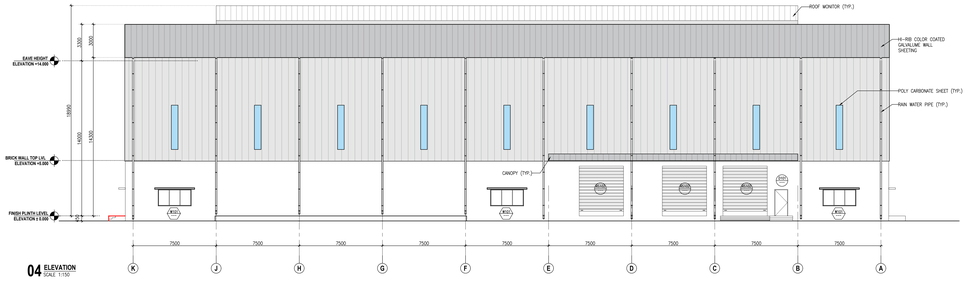

04 ELEVATION
SCALE 1:150

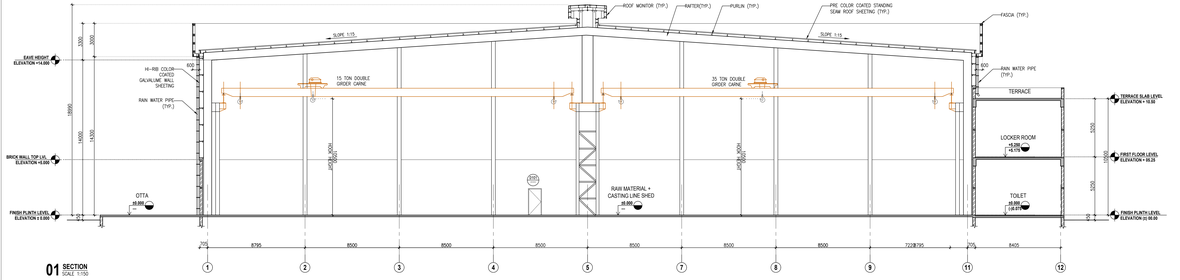

01 SECTION
SCALE 1:150

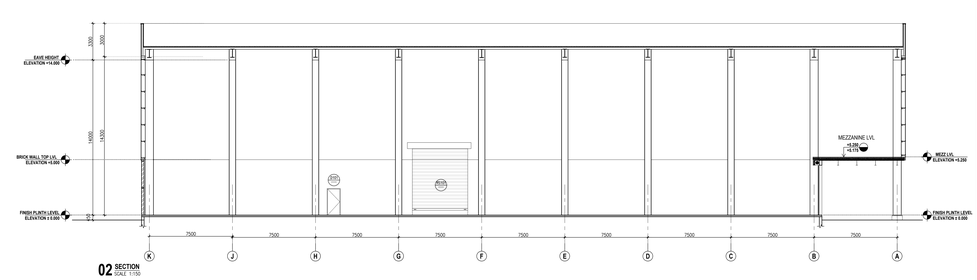


02 SECTION
SCALE 1:150

FOR TENDER

NO.	DATE	DESCRIPTION	DRAWN BY	CHECKED BY

REVISION HISTORY

KEY PLAN
SCALE : N.T.S.

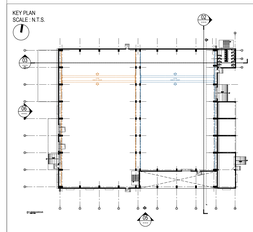

REFERENCE DRAWINGS :

01. ARCHITECTURAL : -
02. STRUCTURAL : -
03. HVAC : -
04. ELECTRICAL : -
05. UTILITIES : -

SECTION & ELEVATION

RM & CASTING LINE SHED

AGRAWAL METAL WORKS(P) LTD.

PROJECT NO.	SCALE :	DRAWN :	ASHISH C.
3824	1:150	CHECKED:	BHAKTI B.
	DATE :	APPROVED:	DARSH D.
	03-12-2024	COORDINATION CHECKED	DARSH D.

VMS ENGINEERING & DESIGN SERVICES (P) LTD.
CHITRAKOOT FLATS, B/H TIMES OF INDIA, OFF ASHRAM ROAD,
AHMEDABAD-380 009. PHONE: +91 (079) 2658-8826, 4023-4039
WWW.VMSCONSULTANTS.COM

SHEET SIZE	DRAWING NO.	TENDER	REVISION
841x 1500	T.A.1.201	R	S0