


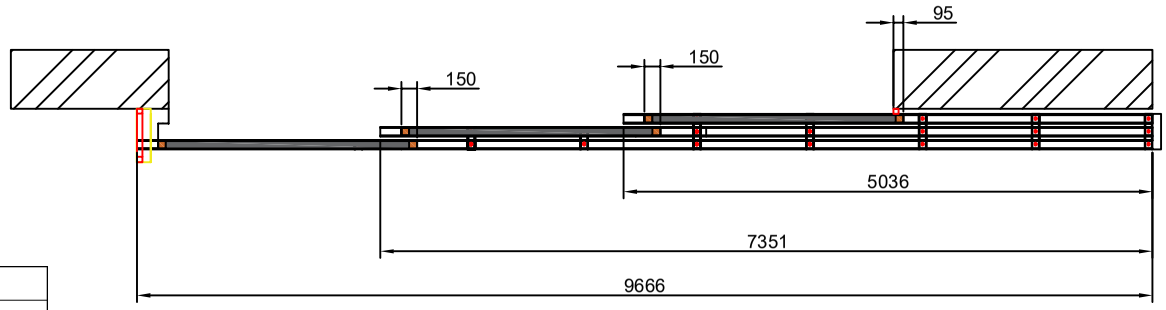


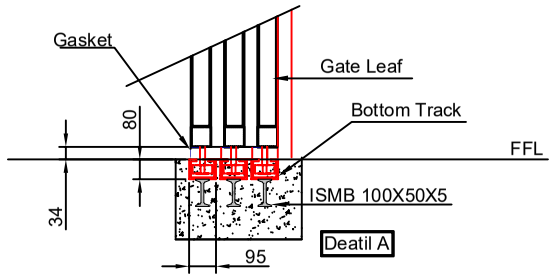

Client scope
*Front Gutter need to be shift. * roof need to be shifted by 300 mm approx. *Civil foundation need to be done for tracks

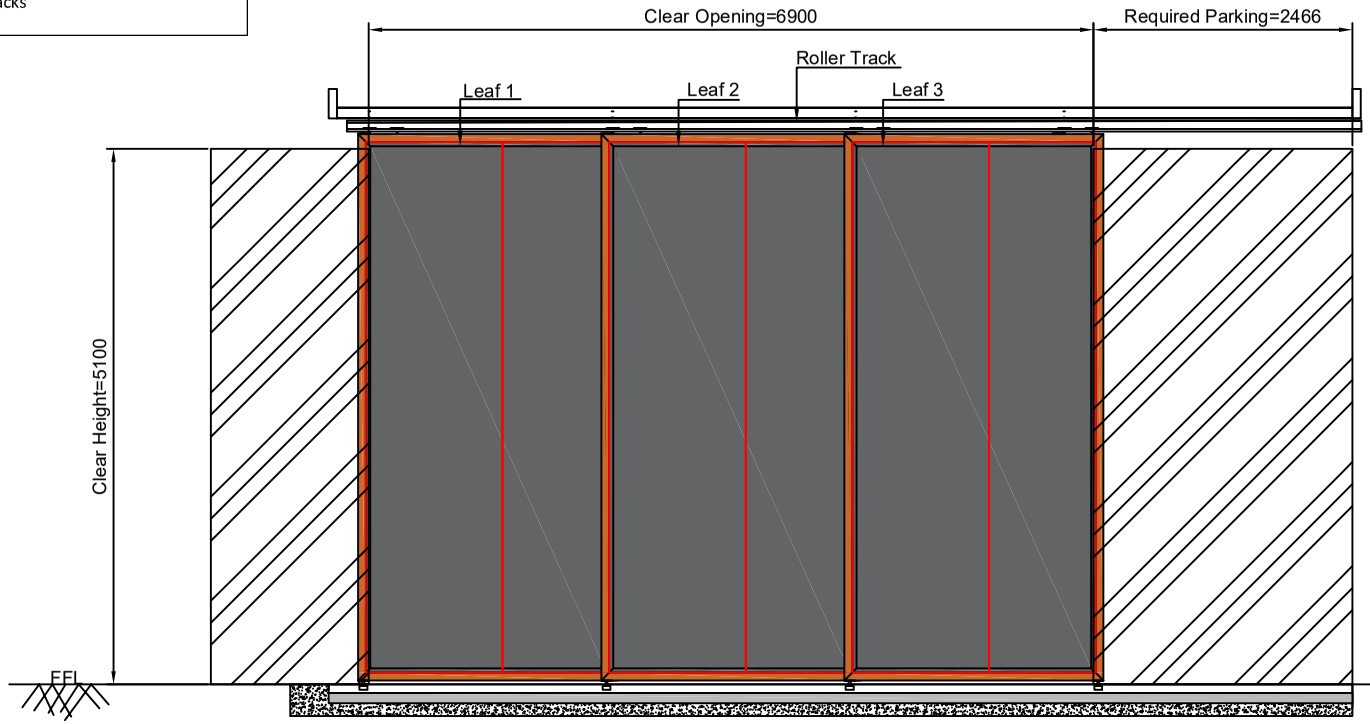

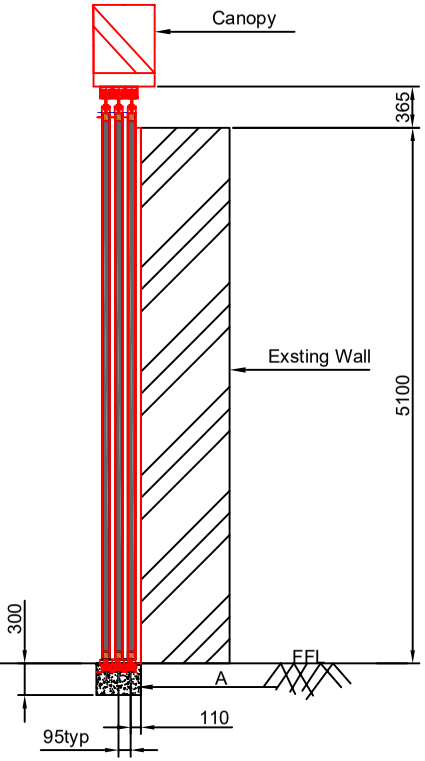

Note:--

1.All dimension are in MM
2.All Civil work will be in client scope
3.Required Parking space will be 2465
4.Manufacturing,civil and installation tolerance will be ±10mm
5.Top and Bottom track should be in parallal within ±3mm

Rev No.	Revision	Date	Revised By

This drawing & design is the property of NIHVA TECHNOLOGIES. Not to be sold or copied to any other concern.

TITLE:- 3 LEAF RIGHT SIDE CRM DOOR 11

	NAME	DATE	SIGN
DRAWN	SUJATA	25/04/2022	
CHECK	M.SUTAR	25/04/2022	
APPRD.	V.TARAK	25/04/2022	

NIHVA TECHNOLOGIES PVT. LTD.
NIHVA TECHNOLOGIES PVT. LTD. PUNE
Tel : 020 66304033
Email:- info@nihva.com
Website:- www.nihva.com

CLIENT - LESTECH
LOCATION - POSCO MANGAON
PRODUCT - SLIDING DOOR

If any queries contact : design@nihva.com | DWG NO:-NIHVA/22-23/CLT/0016 | REV- 0

ALL DIMENSION ARE IN mm | SCALE: NTS | SCALE:-- 1:1 | SHEET: 01 OF 01