
PRODUCED BY AN AUTODESK EDUCATIONAL PRODUCT

PRODUCED BY AN AUTODESK EDUCATIONAL PRODUCT

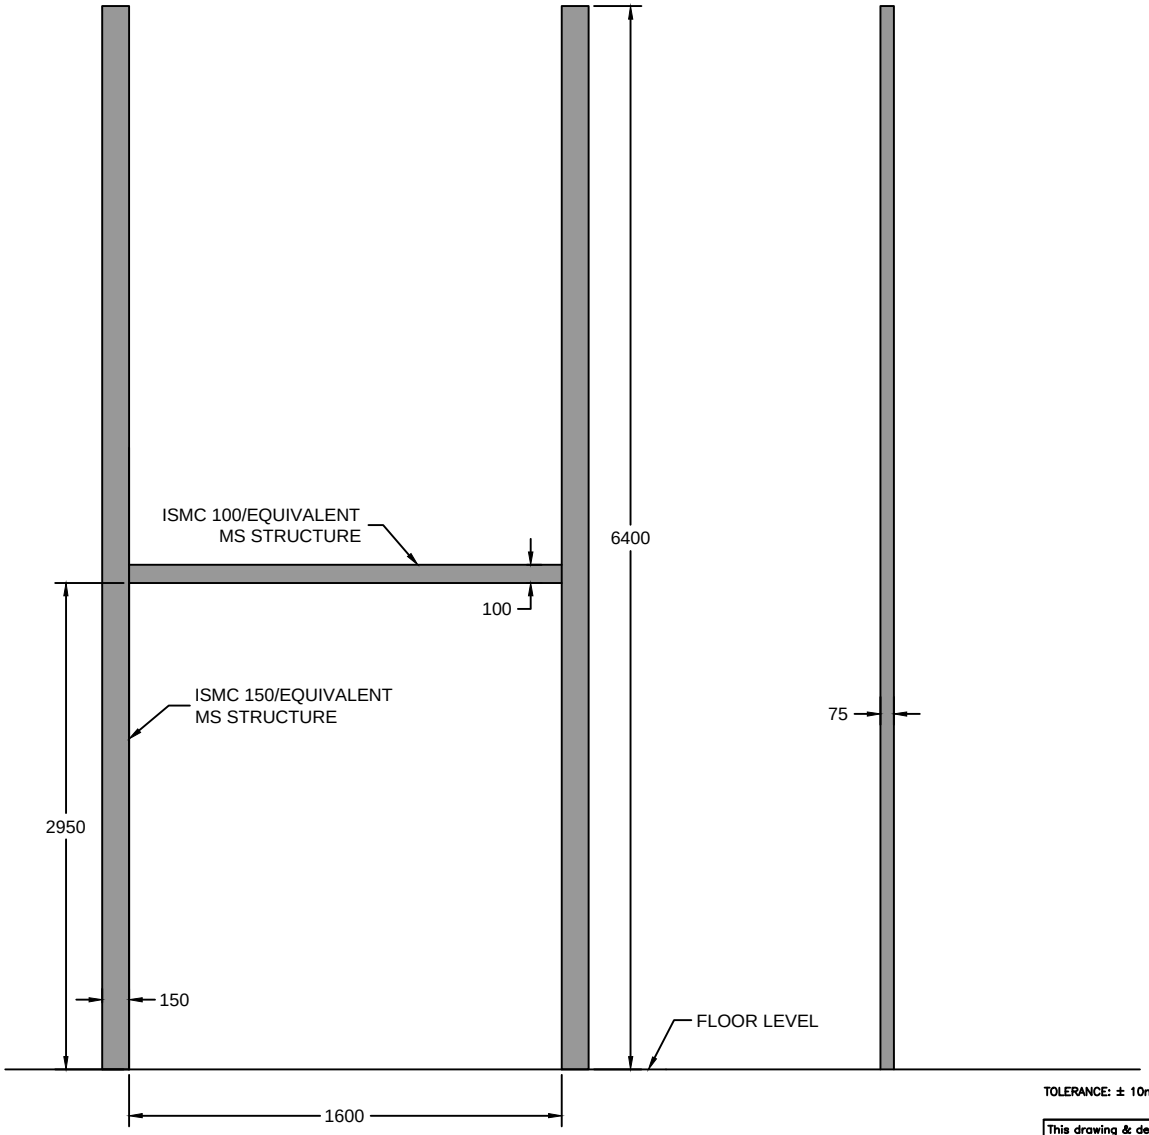

MS STRUCTURE

TOLERANCE: ± 10mm

This drawing & design is the property of NIHVA TECHNOLOGIES. Not to be sold or copied to any other concern.

TITLE: SECTIONAL DOOR (VERTICAL LIFTING)

NIHVA TECHNOLOGIES PVT. LTD.
NIHVA TECHNOLOGIES PVT. LTD. PUNE
Website:- www.nihva.com
Tel : 020 66304033
Email:- info@nihva.com

	NAME	SIGN	DATE
DRAWN	P.A		10.02.20
CHECK	G.J		10.02.20
APPROVAL			

CLIENT - R.P TECH

PROJECT -

SITE - PUNE

If any queries contact : design@nihva.com

DWG. NO. : NIHVA/19-20/ REV: 0

ALL DIMENSION ARE IN mm

SCALE: NTS WT: SHEET: 01 OF 01

PRODUCED BY AN AUTODESK EDUCATIONAL PRODUCT