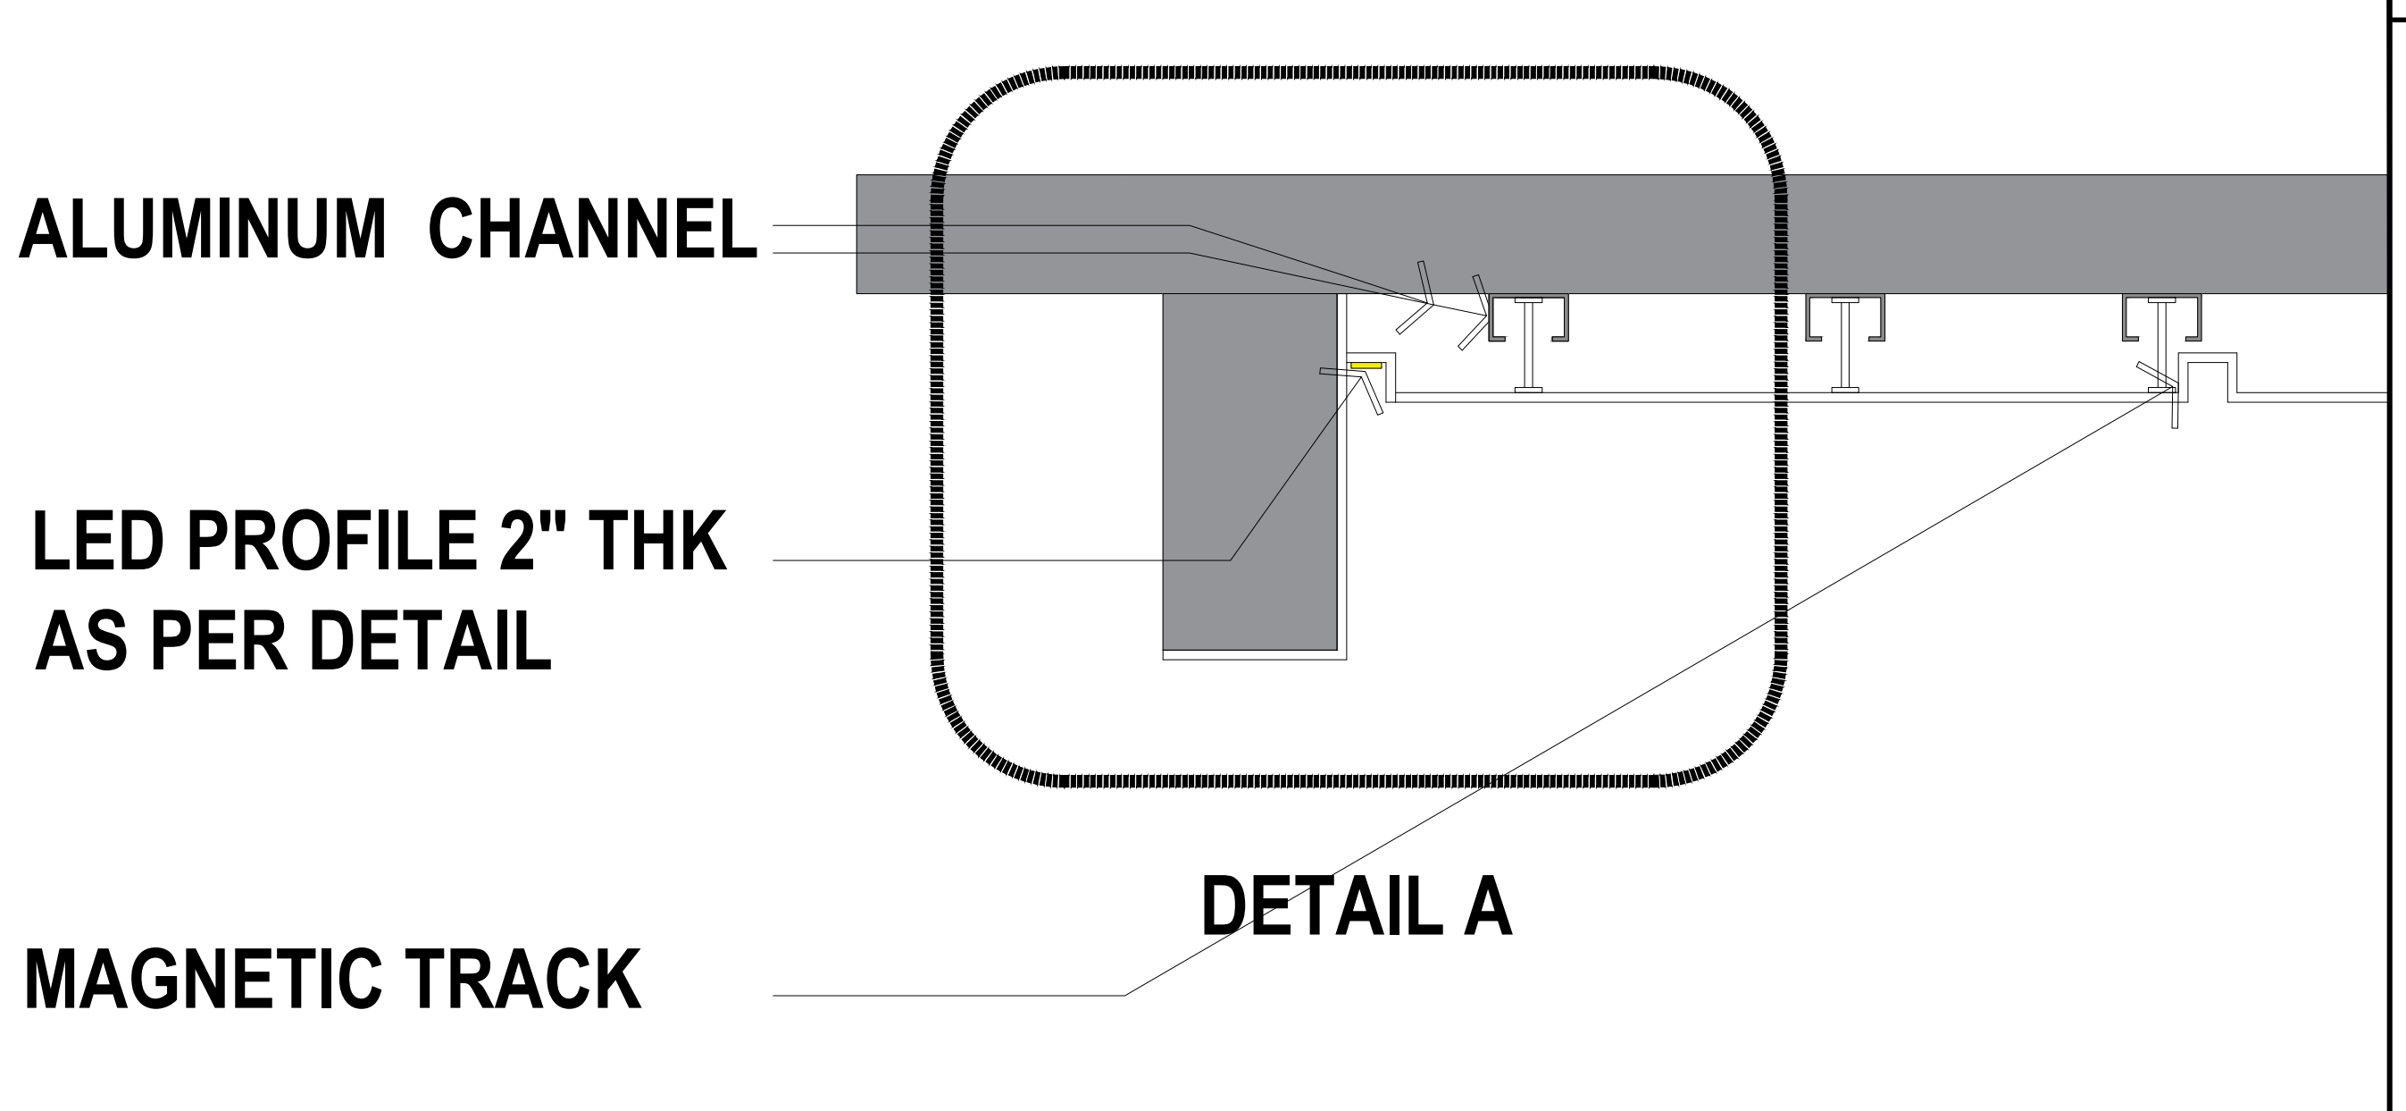

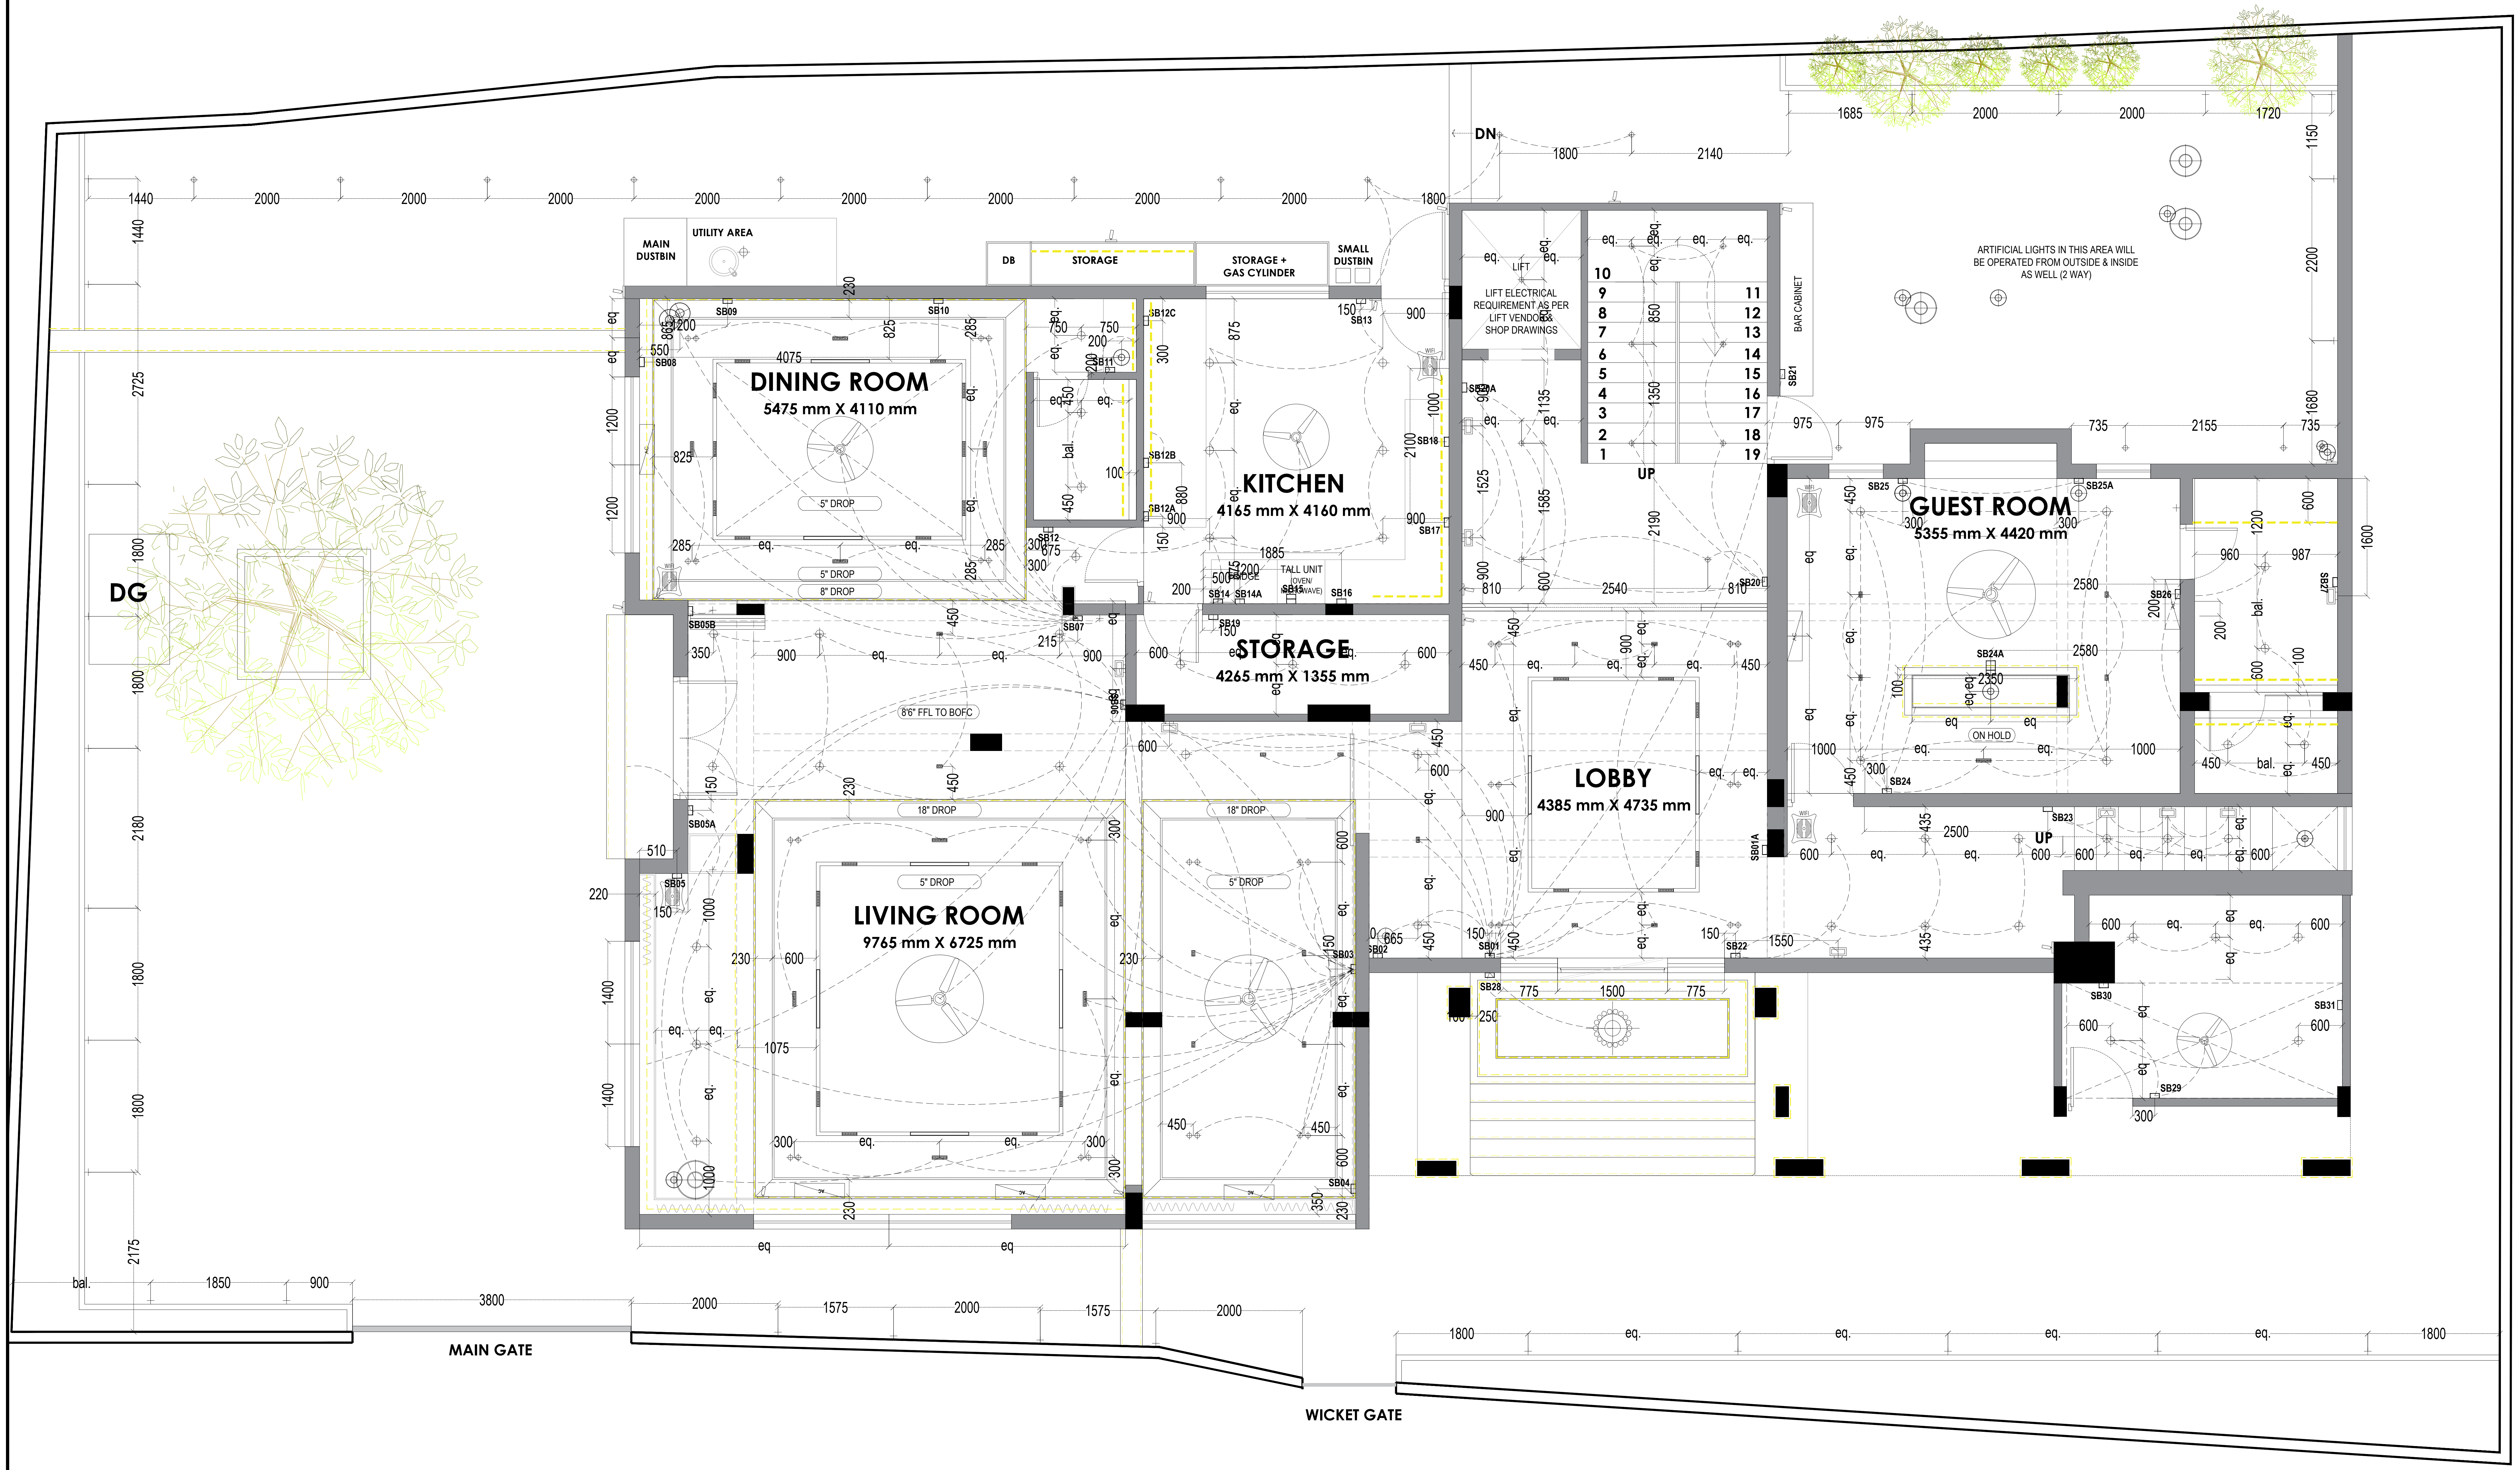

01 GROUND LEVEL - LIGHTING LAYOUT

SCALE: 1:30

NOTES :

- THIS DRAWING IS A RIGHT & PROPERTY OF ABD. IS NOT TO BE PRODUCED, COPIED, HANDED OVER TO THIRD PARTY OR USED FOR ANY OTHER PURPOSE OTHER THAN FOR WHICH IT IS INTENDED. AND REMAIN OUR SOLE PROPERTY. THIS DRAWING TOGETHER WITH ANY COPIES MADE BY THE RECIPIENT SHALL BE RETURNED ON DEMAND TO US.
- ONLY WRITTEN DIMENSIONS TO BE FOLLOWED.
- THE CONTRACTOR MUST CHECK ALL DIMENSIONS & DETAILS & BE RESPONSIBLE FOR THE SAME. ANY DISCREPANCY SHALL BE BROUGHT TO THE NOTICE OF THE ARCHITECT.
- THIS DRAWING SHOULD BE READ IN CONJUNCTION WITH RELEVANT WORKING & DETAILED DRAWINGS.
- ALL DIMENSIONS SHALL BE VERIFIED ON SITE PRIOR TO START OF WORK.
- DWG. TO BE READ IN CONJUNCTION WITH STRUCTURAL DRAWINGS.
- REF. MEP. DRAWINGS / STRUCTURAL DRAWINGS TO CONFIRM SLEEVES LOCATIONS & SIZE.

KEY PLAN

LEGEND				
SR.N.	SYMBOL	TYPE	REMARKS	
1	⌖	COB LIGHT	15 WATT NATURAL	
2	▭	WALL LIGHTS	LIGHT POINT ON WALL	
3	— —	COVE/PROFILE LIGHT	CEILING COVE LIGHT /SHELF PROFILE LIGHT	
4	⊛	FAN	4' DIAMETER	
5	+	WIRE POINT	7WATTS NATURAL	
6	⊛	CHANDELIER	PLYWOOD PIECE ABOVE TO ACCOMMODATE CHANDELIER	
7	◎	HANGING LIGHT	PLYWOOD PIECE ABOVE TO ACCOMMODATE CHANDELIER	
8	▭	TRACK LIGHT	15 WATT NATURAL	

No.	ISSUE	DATE

REVISIONS

WORKING DRAWING

CLIENT
Mr.Lokesh Thakkar

PROJECT
BUNGALOW @ BHOSALE NAGAR,PUNE

TITLE
GROUND FLOOR -
ELECTRICAL LAYOUT

02
02

SCALE	AS SHOWN
DATE	18/03/2024
DRAWN	AB
CHKD	AB
APRVD	AB
JOB No.	DWG No.

NORTH

..\20231118\WhatsApp Image 2022-04-04 at 9.11.55 AM.jpeg

The content of this Document/Drawing is the exclusive property of 'Aboli Bambal Designs' and that of our Client and is, unless specifically stated otherwise, protected by copyright.