

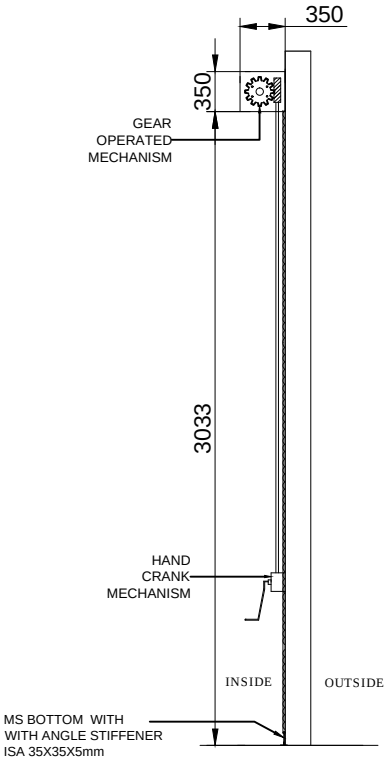



SIDE VIEW

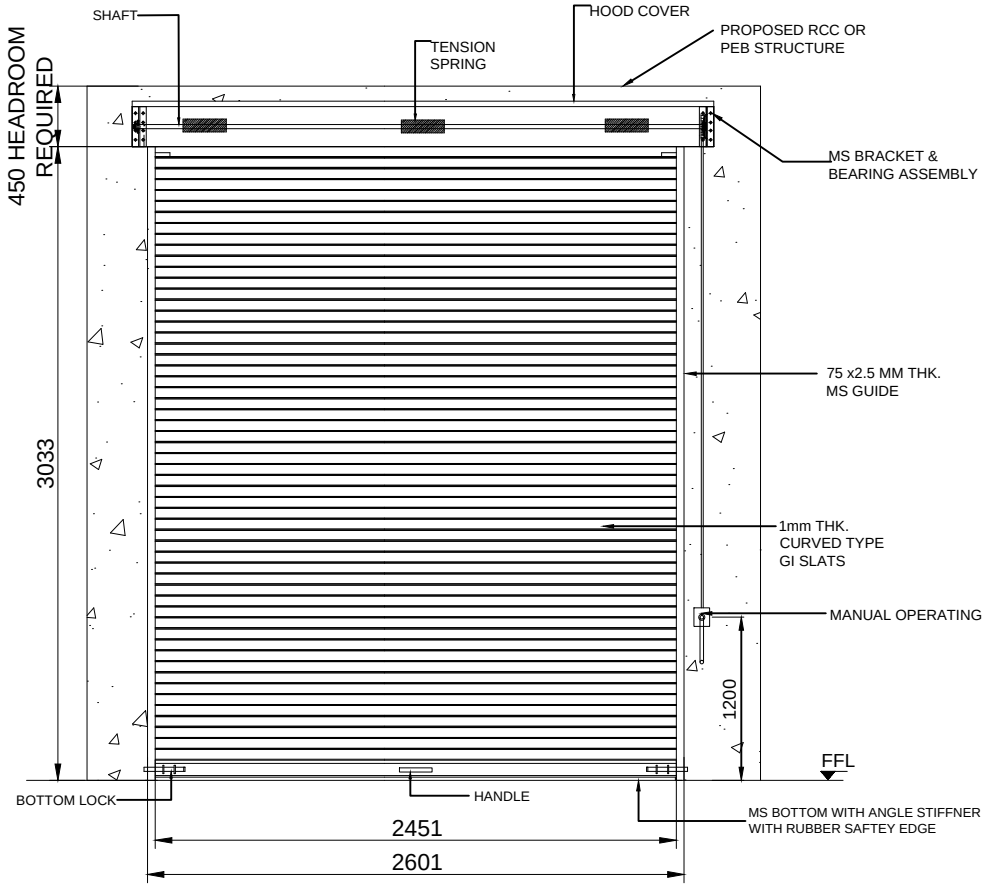


INSIDE ELEVATION

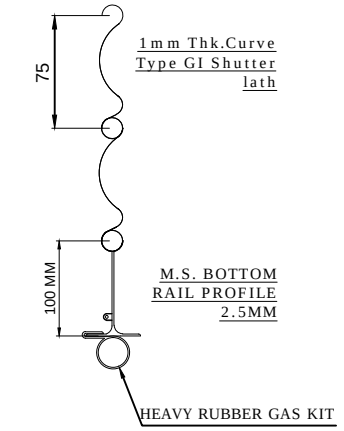

M.S. BOTTOM RAIL PROFILE 2.5MM

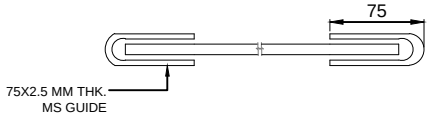

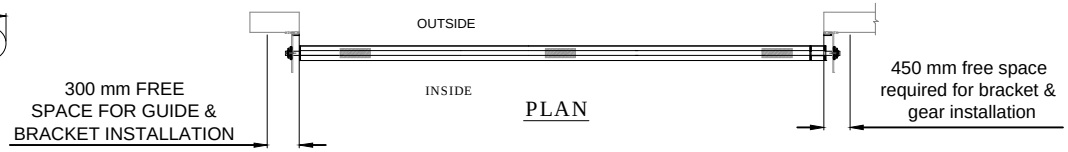

PLAN

S.N.	LOCATION	SIZE	QUANTITY
1	B6A	2451(W)X3033(H)	06 Nos

NOTE-
1. ALL CIVIL WORK WILL BE CLIENT'S SCOPE.
2.STRUCTURE REQUIRED FOR SHUTTER IS IN CLIENT'S SCOPE.
3.FINAL FINISH OF SHUTTER WILL BE IN POWDER COATING OF APPROVED COLOR i.e.RAL 7001.

TOLERANCE - ±10mm

This drawing & design is the property of NIHVA TECHNOLOGIES. Not to be sold or copied to any other concern.

TITLE	GEAR OPERATED ROLLING SHUTTER 2.451mX3.033m Right side gear box.			NIHVA TECHNOLOGIES PVT. LTD. PUNE
	NAME	SIGN	DATE	Website:- www.nihva.com Email:- info@nihva.com
DRAWN	SURAJ		04.09.2018	CLIENT -
CHECK	PRADEEP		04.09.2018	PROJECT -
APPRD.	R.D		04.09.2018	SITE LOCATION -
If any queries contact : design@nihva.com				DWG. NO. : NIHVA/18-19/VDR/113 REV- 0
ALL DIMENSION ARE IN mm				SCALE: NTS WT: SHEET: 01 OF 01