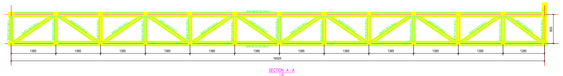
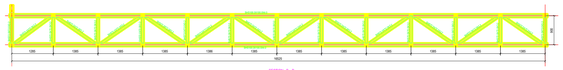
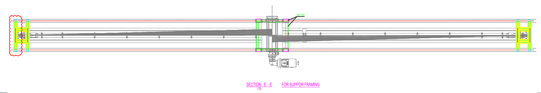
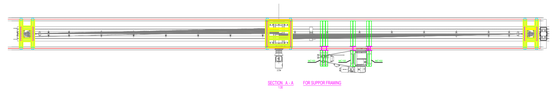
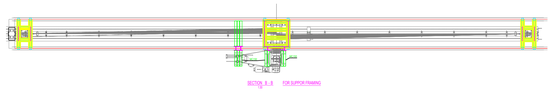

SECTION E-E

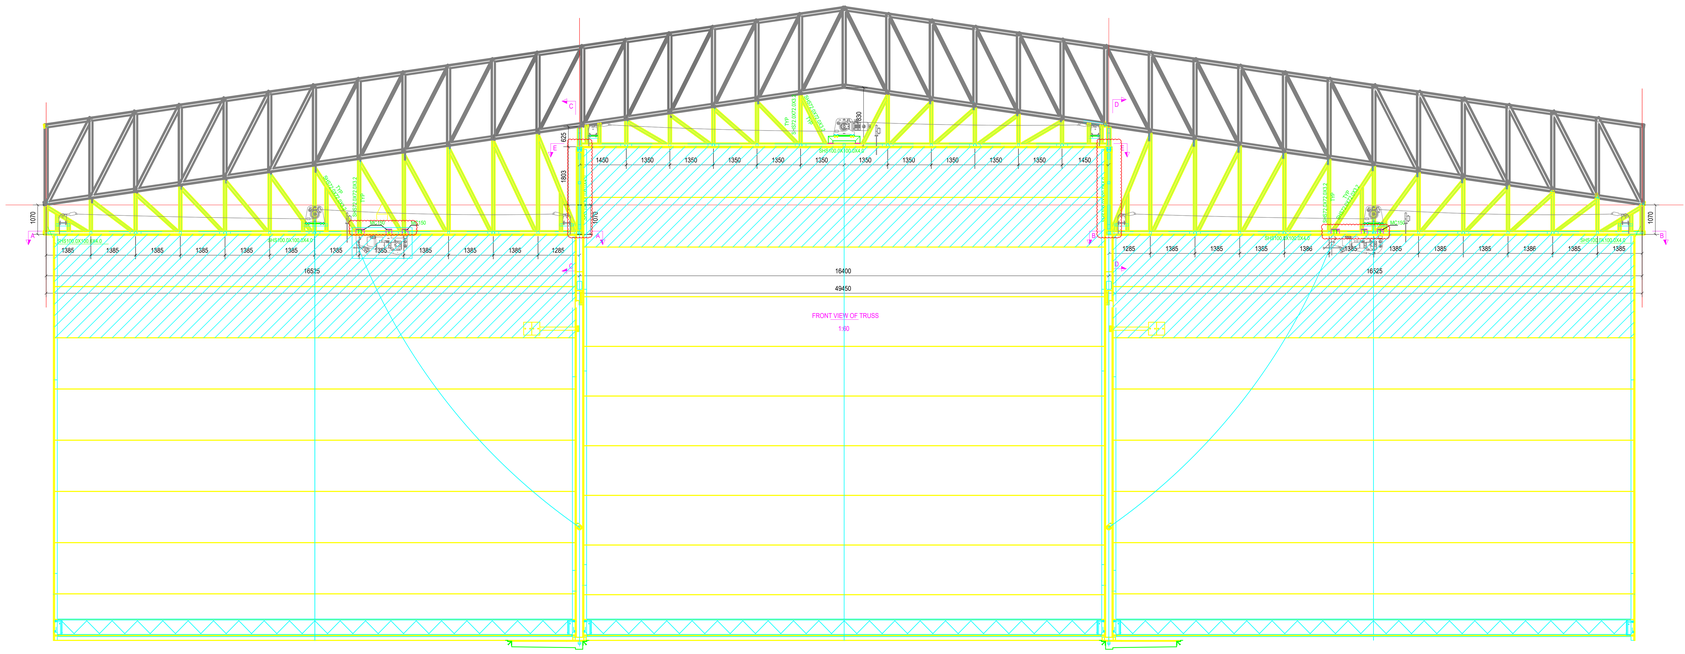

SECTION A-A

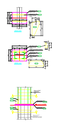

SECTION B-B


SECTION E-E FOR SUPPOR FRAMING

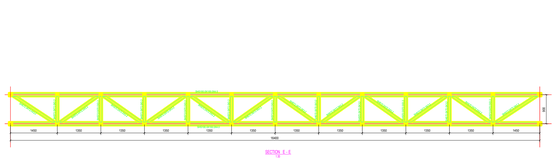

SECTION A-A FOR SUPPOR FRAMING

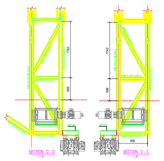

SECTION B-B FOR SUPPOR FRAMING

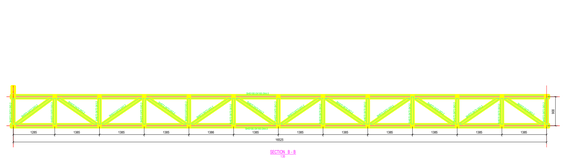

1400
1350
1350
1350
1350
1350
1350
1350
1350
1350
1350
1450
16400
49450
FRONT VIEW OF TRUSS

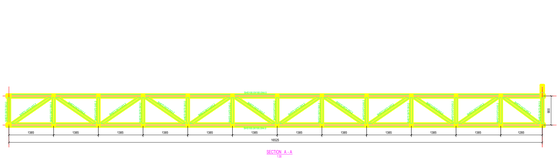





SECTION A-A


SECTION B-B
SECTION C-C


SECTION B-B


SECTION A-A