

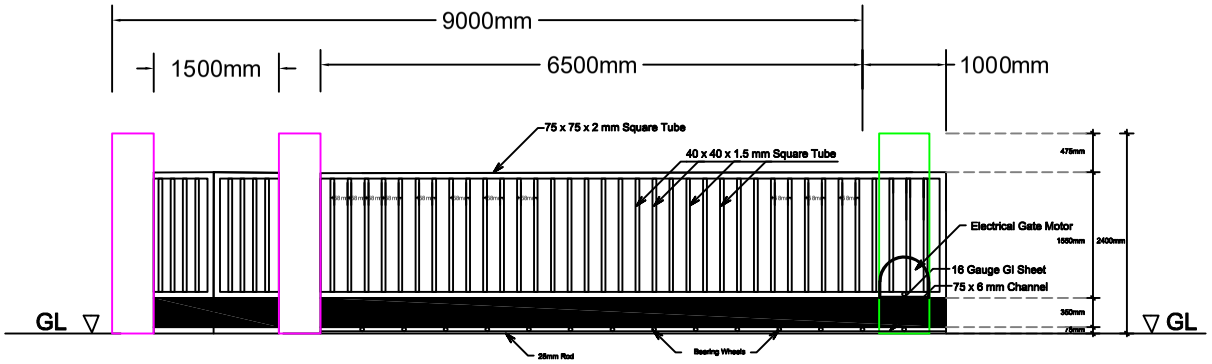


ELEVATION OF AUTOMATIC SLIDING GATE

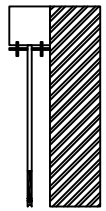

SIDE VIEW

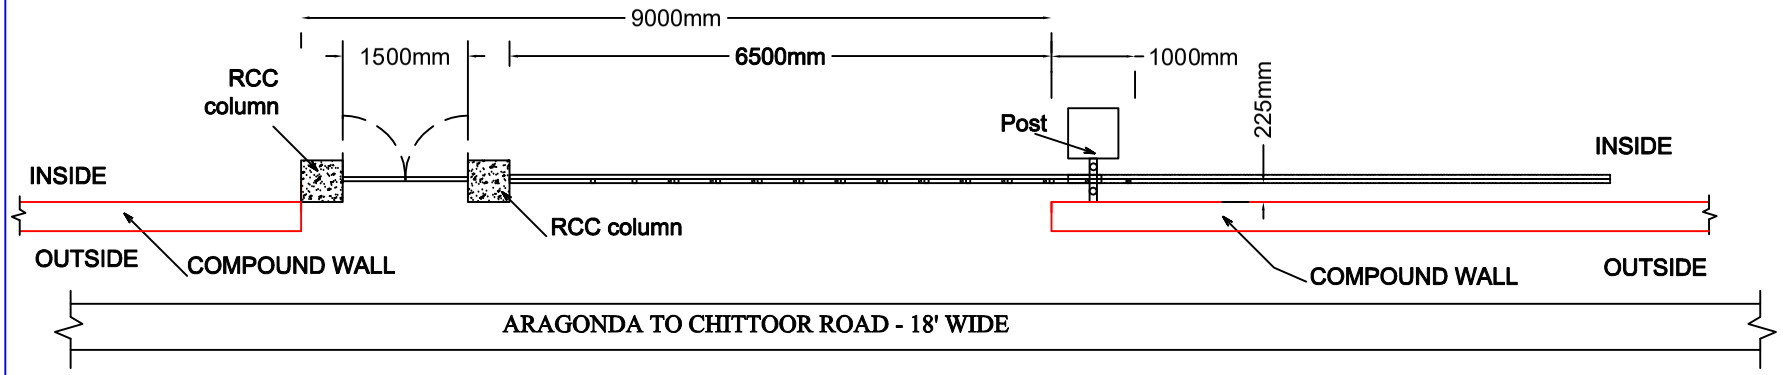

PLAN OF AUTOMATIC SLIDING GATE

FOR APPROVAL ONLY

RCC column 500mm x 500mm

Post 600mm x 600mm

NOTE:1) All the Dimensions are in Millimeters,Meters
2) Do not Scale the Dwg,Only written dimensions are to be followed.

REV	DESCRIPTION	DATE

PROJECT: Modernization of Chittoor Plant

CLIENT: BALMER LAWRIE & CO LTD

DWG TITLE: Sliding Gate Details

DATE:20-09-2021	DRAWN :
OPTION :	CHECKED :
SCALE : N.T.S	APPROVED :
NORTH	OWNERS SIGNATURE

N

INDRAPRASTA CONSULTANTS
STRUCTURAL ENGINEERS, ARCHITECTS, INTERIOR DESIGNERS
810, 2nd floor, Flat # 302, Rd. # 2, Castle Hills, Masab tank,
Hyderabad 500057.
Phone No. 91772-25598, 98480-25598.
E-Mail: chandrashekaran.kn@gmail.com