


FOUNDATION DETAILS

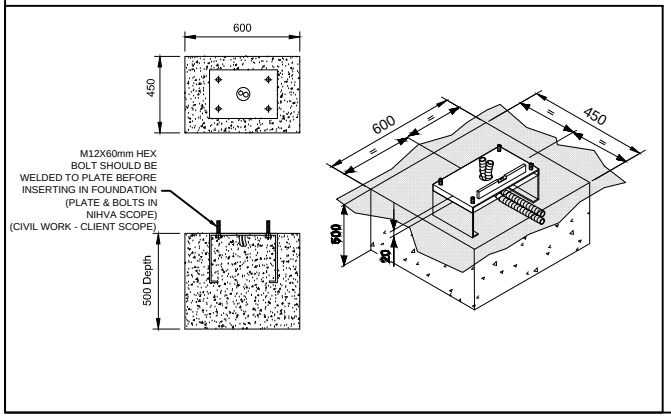

BOOM BARRIER QTY : 1 NO

TOLERANCE - ±10mm

This drawing & design is the property of NIHVA TECHNOLOGIES. Not to be sold or copied to any other concern.

TITLE				
8 MTR BOOM BARRIER				NIHVA TECHNOLOGIES PVT. LTD. PUNE Tel : 020 66304033 Email:- info@nihva.com Website:- www.nihva.com
	NAME	SIGN	DATE	
DRAWN	P.A		27.07.2020	CLIENT -
CHECK	G.J		27.07.2020	PROJECT -
APPROVAL				SITE LOCATION -
				DWG. NO. : NIHVA/20-21/VDR/0013 REV-R00
If any queries contact : projectsupport@nihva.com				SCALE: NTS WT: SHEET: 01 OF 01
ALL DIMENSION ARE IN mm				