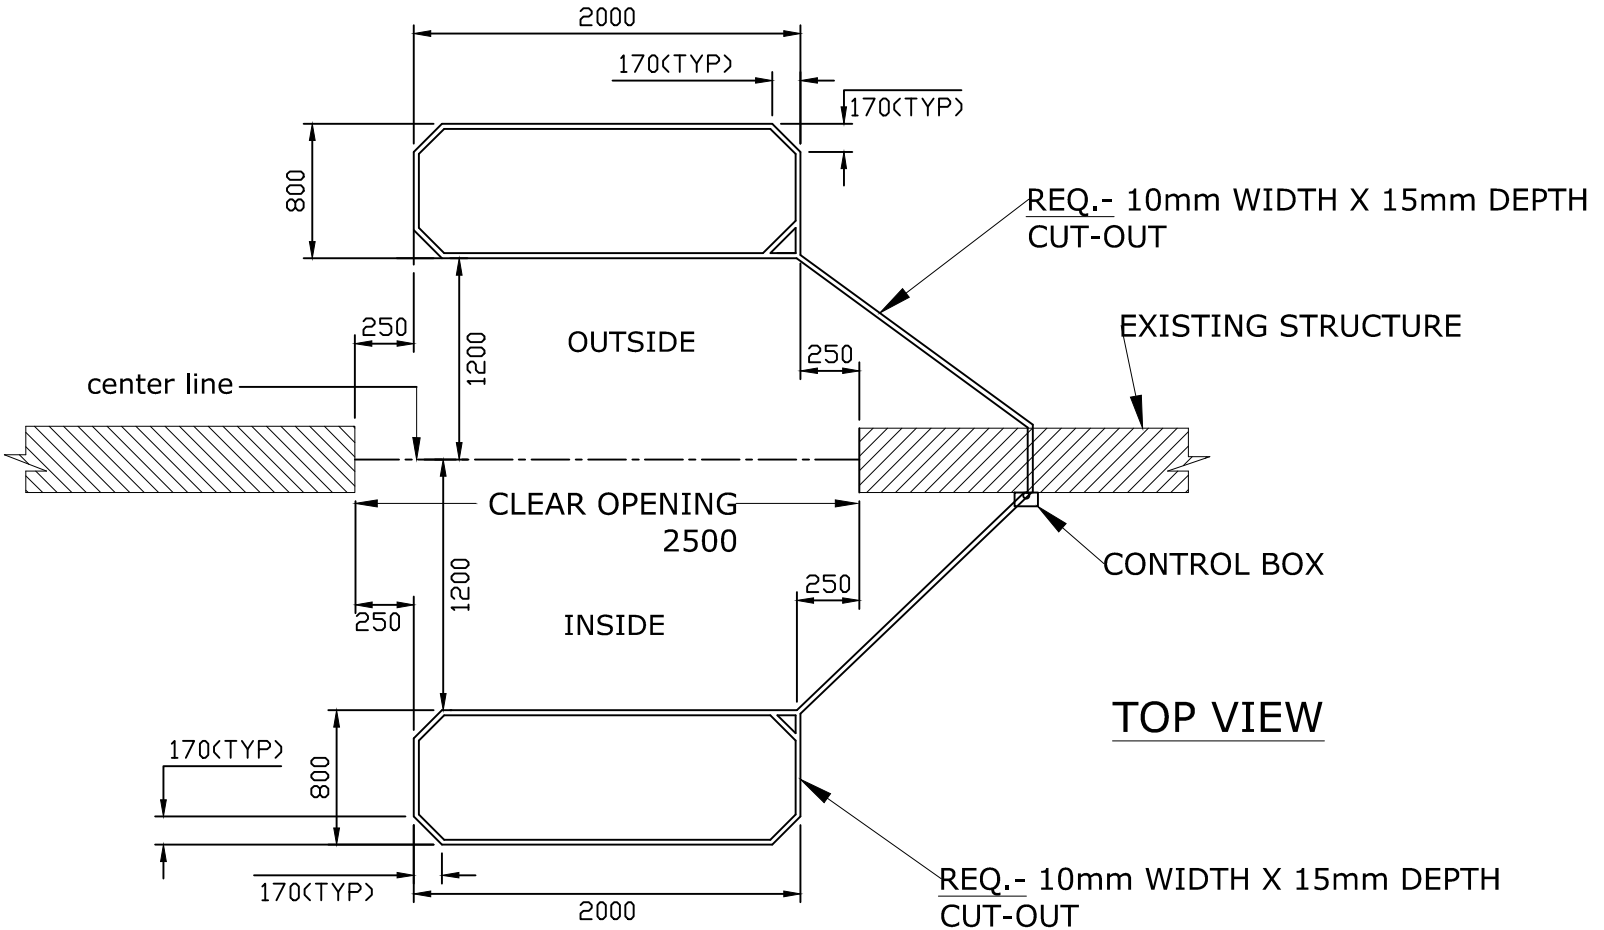


CLEAR WIDTH (CW)	CLEAR HEIGHT (CH)	QUANTITY
2500	6000	4

This drawing & designing is the property of NIHVA TECHNOLOGIES. Not be sold or copy to any other concern.

TITLE

FLOOR CUT-OUT FOR LOOP DETECTOR FOR HIGH SPEED DOOR (RR392)

CLIENT APPROVAL

ALL DIMENSION ARE IN mm

	SIGN	DATE
DRAWN	OMKAR	07/10/17
CHECK	SHEKHAR	07/10/17
ENG		
APPRD.	SHEKHAR	07/10/17
MFG		
Ref. No.		

NIHVA TECHNOLOGIES PVT. LTD.

NIHVA TECHNOLOGY PVT. LTD. PUNE
Tel : 020 66304033
Email:- info@nihva.com
Website:- www.nihva.com

CLIENT - Ferrero India Pvt. Ltd.

PROJECT-

SITE - BARAMATI

DWG. NO. - NIHVA/17-18/0233

SCALE: NTS | WT: | SHEET: 01

If any queries contact : projects@nihva.com