



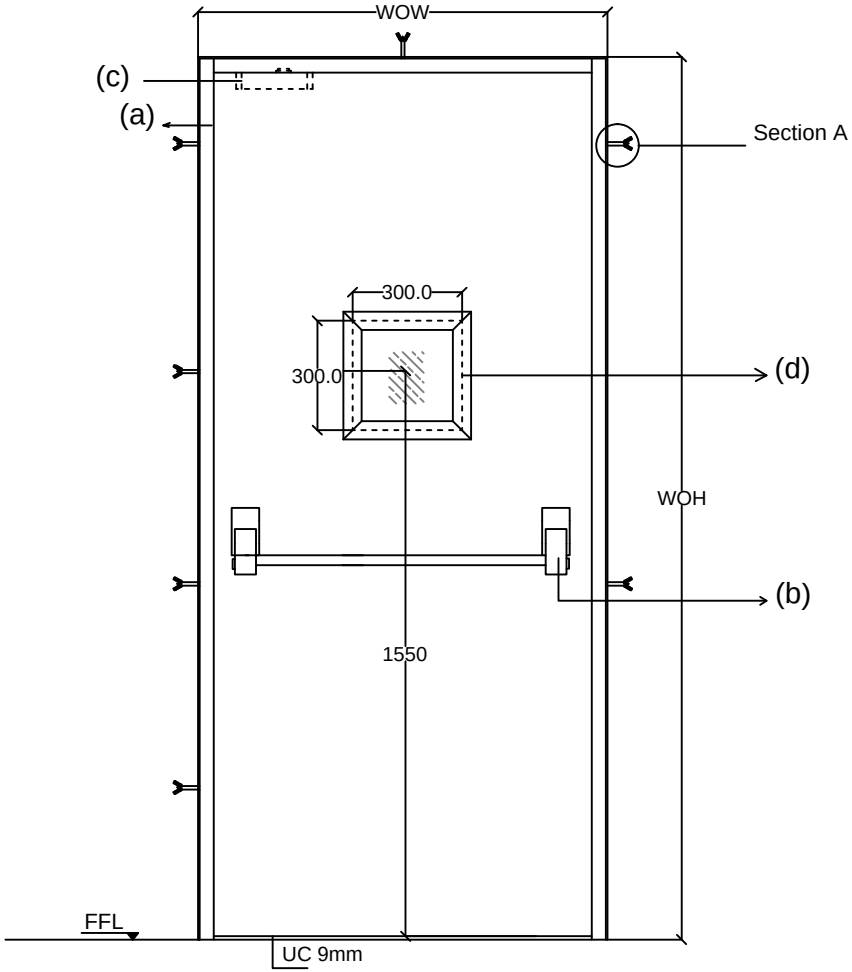


Inside Elevation

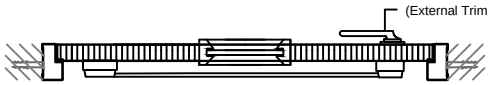

Top View

COLOR- 9003 SIGNAL WHITE

Abbrevation's:
WOW-Wall Opening Width
WOH-Wall Opening Height
UC-Under Cut
FFL-Finished Floor Level

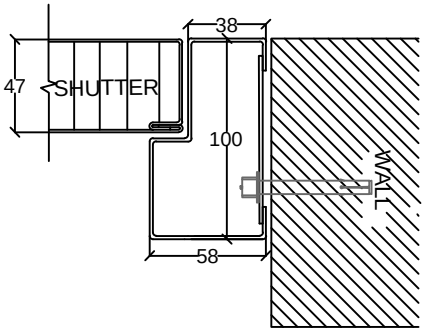

Detail view of Section A

ASSESORIES DETALES

(a) HINGES: SS Ball bearing butt hinges 100x75x3mm

(b) LOCK : PHCR 1000 series puch bar (Make Dorma) External Trim 2905 with Cylinder For Push Bar (Make -Dorma)

(c) DOOR CLOSER: 1 No. Door Colser TS 71 with std arm

(d) GLASS : 1No. Clear fire Vision Glass Clear 6mm of size 300x300mm.

Shutter thickness : 47 mm
Frame Sheet thick : 1.20mm
Shutter sheet thick : 0.80mm
Fixing : On Soliid Brick plasterd wall with Anchors

NOTE:- *All Dimensions are in mm.
*Tolerance:-All Linear Dimensions ±3mm,Others ±0.5mm.
*The Drawing Is For Location of Hardware only. Drawing Does Not Represent The Hardware For More Clarity, Please Go Through Hardware Broucher.

DOOR TYPE	WOW	WOH	TYPE 3	TYPE 4	TOTAL
FIRE DOOR	1165	2158			1
	1180	2160			1
	1170	2184			1
	1120	2166			1

Client should mention door handling type from door handling sheet.

This drawing & designing is the property of NIHVA TECHNOLOGIES. Not be sold or copy to any other concern.

Fire Door

CLIENT APPROVAL

ALL DIMENSION ARE IN mm

	NAME	DATE	SIGN.
DRAWN	OMKAR	03/09/16	
CHECK	ANIL	03/09/16	
REV.	0		
APPRD.			
MFG			

NIHVA TECHNOLOGIES PVT. LTD.
NIHVA TECHNOLOGY PVT. LTD. PUNE
Tel : 020 66304033
Email:- info@nihva.com
Website:-www.nihva.com

CLIENT - LUPIN LIMITED
PROJECT - LUPIN BIORESEARCH CENTRE
SITE - PASHAN,PUNE
DWG. NO. - NIHVA/16-17/0070
SCALE: NTS | WT: | SHEET: 01 OF 01
If any queries contact : projects@nihva.com