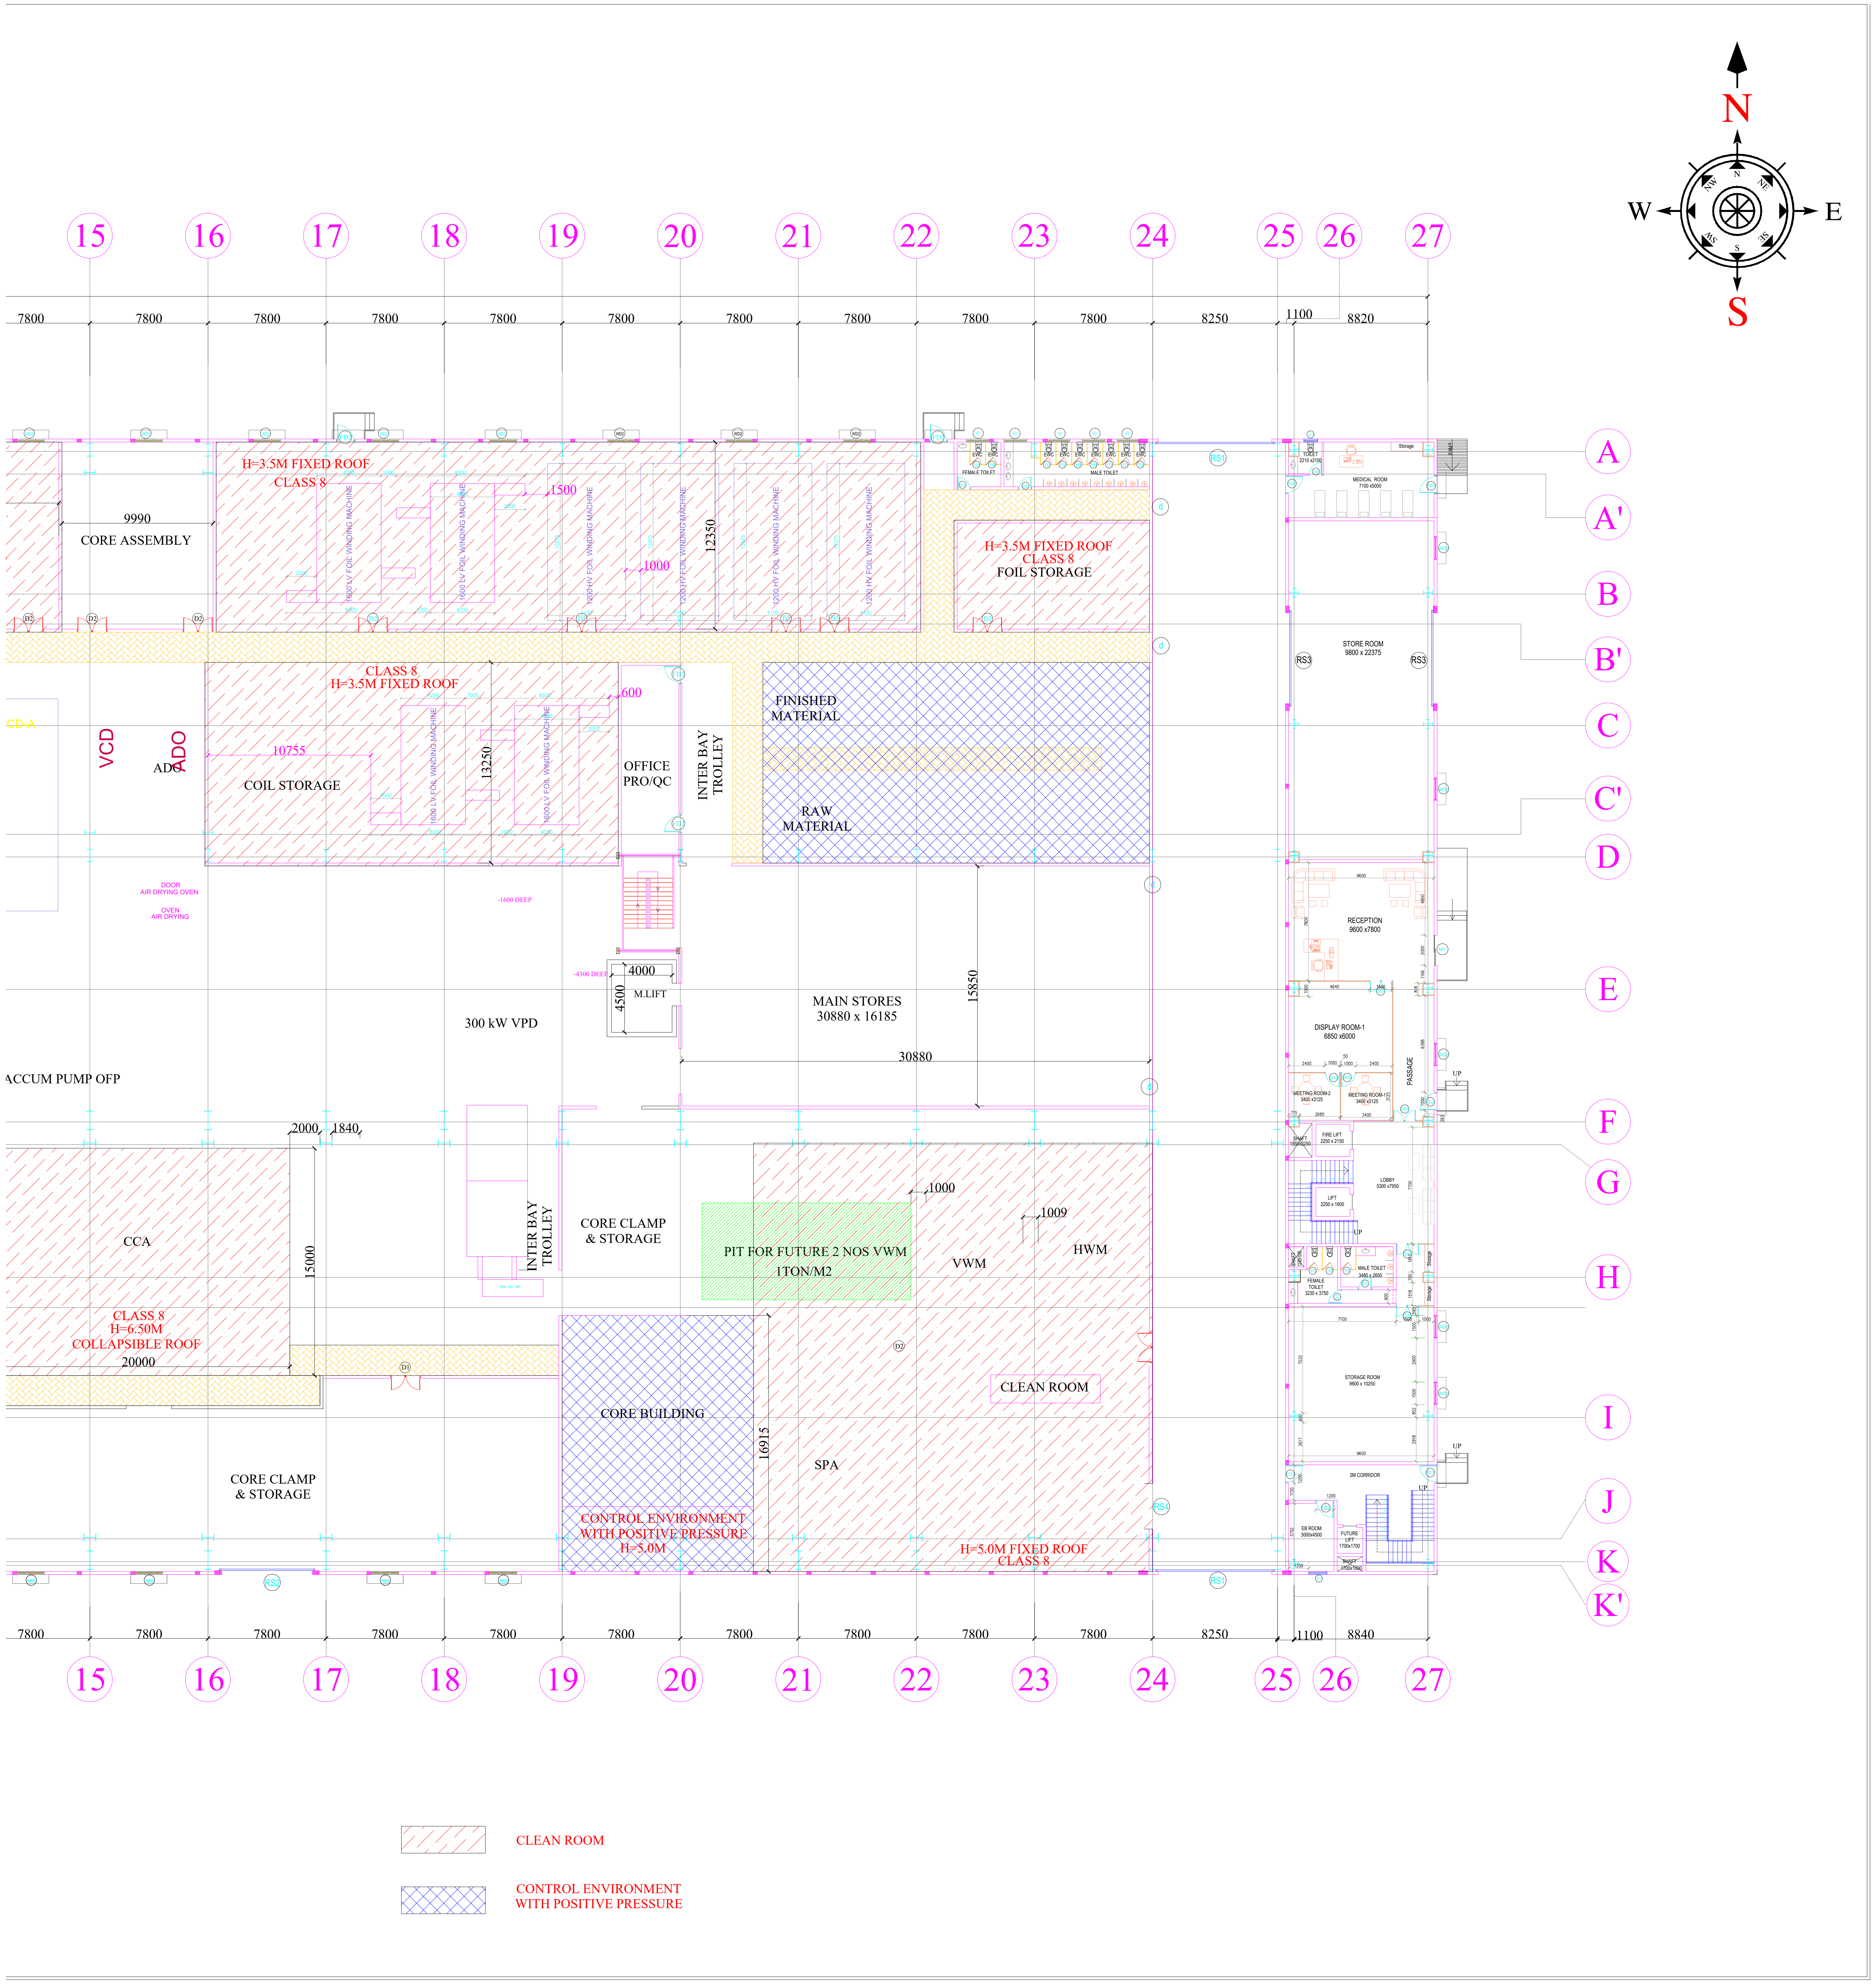
N
S
W
E
15
16
17
18
19
20
21
22
23
24
25
26
27
7800
8250
1100
8820
8840
A
A'
B
B'
C
C'
D
E
F
G
H
I
J
K
K'
H=3.5M FIXED ROOF
CLASS 8
9990
CORE ASSEMBLY
1500
1000
12350
H=3.5M FIXED ROOF
CLASS 8
FOIL STORAGE
CLASS 8
H=3.5M FIXED ROOF
600
10755
COIL STORAGE
13250
OFFICE
PRO/QC
INTER BAY
TROLLEY
FINISHED
MATERIAL
RAW
MATERIAL
VCD
ADO
ADO
CD-A
DOOR
AIR DRYING OVEN
OVEN
AIR DRYING
-1600 DEEP
-4300 DEEP
4000
4500
M.LIFT
300 kW VPD
MAIN STORES
30880 x 16185
15850
30880
ACCUM PUMP OFP
2000
1840
CCA
15000
CLASS 8
H=6.50M
COLLAPSIBLE ROOF
20000
INTER BAY
TROLLEY
CORE CLAMP
& STORAGE
PIT FOR FUTURE 2 NOS VWM
1TON/M2
1000
1009
VWM
HWM
CORE BUILDING
16915
SPA
CLEAN ROOM
CORE CLAMP
& STORAGE
CONTROL ENVIRONMENT
WITH POSITIVE PRESSURE
H=5.0M
H=5.0M FIXED ROOF
CLASS 8
MEDICAL ROOM
STORE ROOM
9800 x 22375
RS3
RS3
RECEPTION
9600 x7800
DISPLAY ROOM-1
6850 x6000
PASSAGE
FIRE LIFT
LIFT
LOBBY
FEMALE TOILET
MALE TOILET
STORAGE ROOM
2M CORRIDOR
UP
▨ CLEAN ROOM
▩ CONTROL ENVIRONMENT
WITH POSITIVE PRESSURE