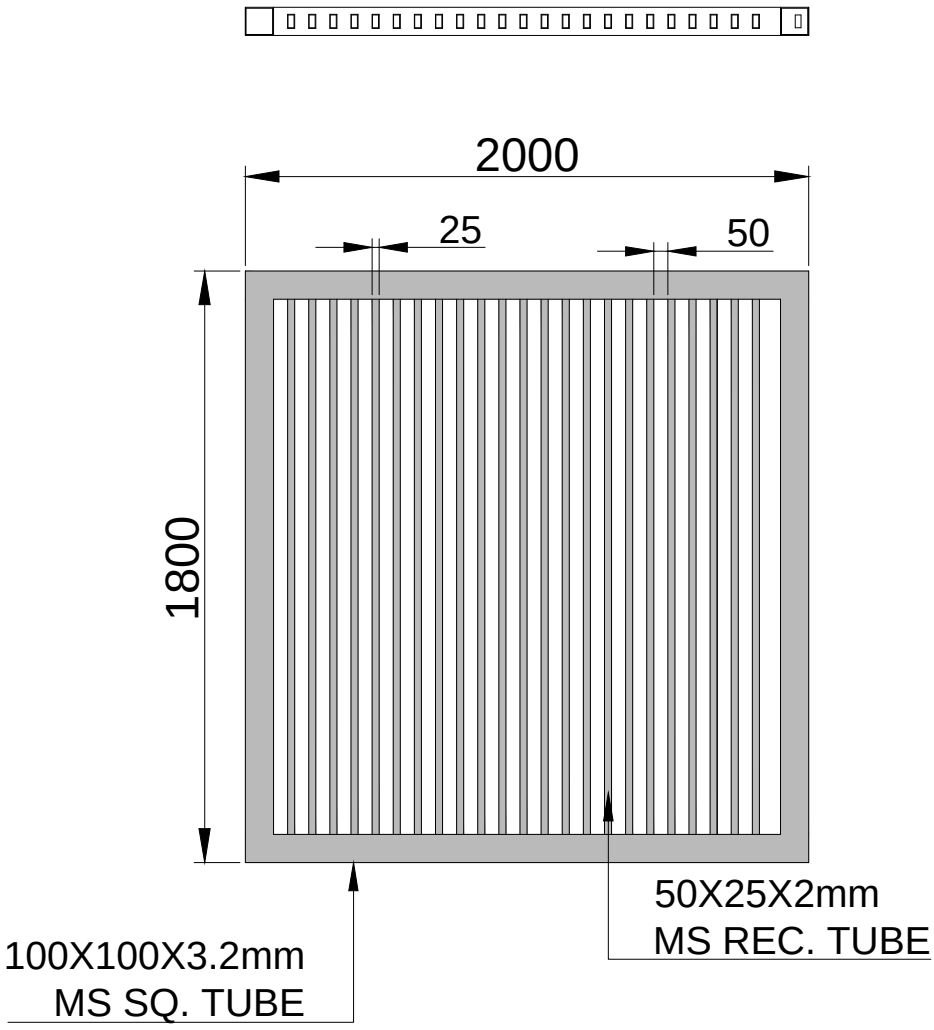


FIXED GATE

QTY- 1 nos

REV NO	DATE	DESCRIPTION
REV -0	31/10/17	INITIAL DRAWING
REV -1	08/11/17	HEIGHT REVISED FROM 2100mm TO 1800mm.

TOLERANCE - ±5mm

This drawing & design is the property of NIHVA TECHNOLOGIES. Not to be sold or copied to any other concern.

TITLE

FIXED GATE
2X1.8m

CLIENT APPROVAL

ALL DIMENSION ARE IN mm

NIHVA
NIHVA TECHNOLOGIES PVT. LTD.

NIHVA TECHNOLOGIES
PVT. LTD. PUNE
Tel : 020 66304033
Email:- info@nihva.com
Website:- www.nihva.com

	SIGN	DATE
DRAWN	OMKAR	31/10/17
CHECK	SHEKHAR	31/10/17
REV.		
APPRD.	SHEKHAR	31/10/17
MFG		
Ref. No.		

CLIENT -

PROJECT -

SITE -

DWG. NO. - NIHVA/17-18/VDR/0149/R01 | REV-1

SCALE: NTS | WT: | SHEET: 01 OF 01

If any queries contact : design@nihva.com