



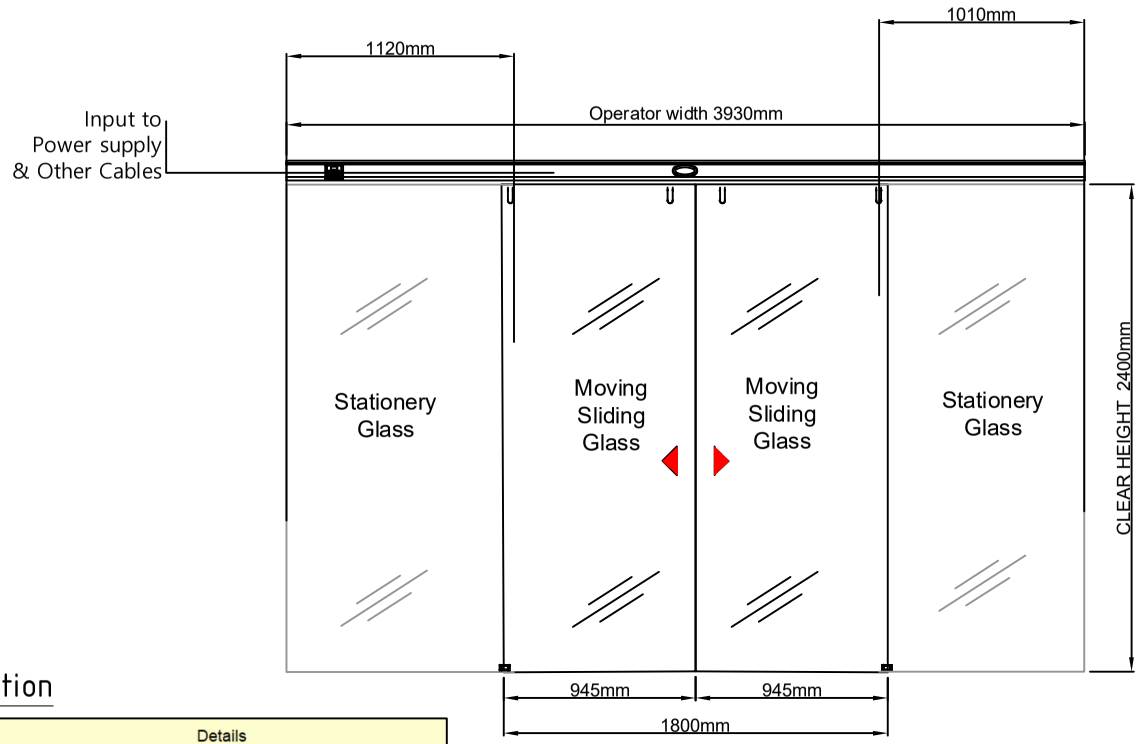

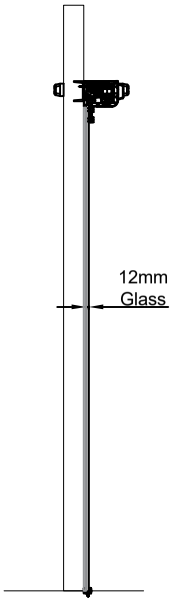

Elevational View A

Technical Specification

Sr.	Description	Details
1	Door type	Fully glazed toughned glass door.
2	Details of glass	Saint Gobain make toughned glass.Glass thickness 12 mm
3	Patch Fittings	All S.S.patch fittings/accessories shall be Dorma fittings.
4	Opening speed	100-300 mm/second.Speed shall be adjustable.
5	Closing speed	100-200 mm/second.Speed shall be adjustable.
6	Operating Temperature	Range -20 to +55 degree Centigrade.
7	Emergency push button	Integrated
8	Built in photo cell for safety	Integrated
9	Controll Unit	Microprocessor radar based control unit is required.
10	Door locking/Deactivitation facillity	Door deactivation facillity(either in Open or closed position) shall be made available. Also a door locking system shall be made available

This drawing & design is the property of NIHVA TECHNOLOGIES. Not to be sold or copied to any other concern.

TITLE:- AUTOMATIC
BI- PARTING GLASS DOOR

NIHVA
NIHVA TECHNOLOGIES PVT. LTD.

NIHVA TECHNOLOGIES
PVT. LTD. PUNE
Tel : 020 66304033
Email:- info@nihva.com
Website:- www.nihva.com

	NAME	DATE	SIGN
DRAWN	SUMIT.J	04-11-2023	
CHECK	A.K.		
APPRD.	V.T.		

CLIENT - TATA MOTORS
LOCATION - Pune
PRODUCT - GLASS DOOR
If any queries contact : design@nihva.com
DWG NO:- NIHVA/23-24/CLT/005 REV- 02
ALL DIMENSION ARE IN mm
SCALE: NTS SHEET: 01 OF 01