
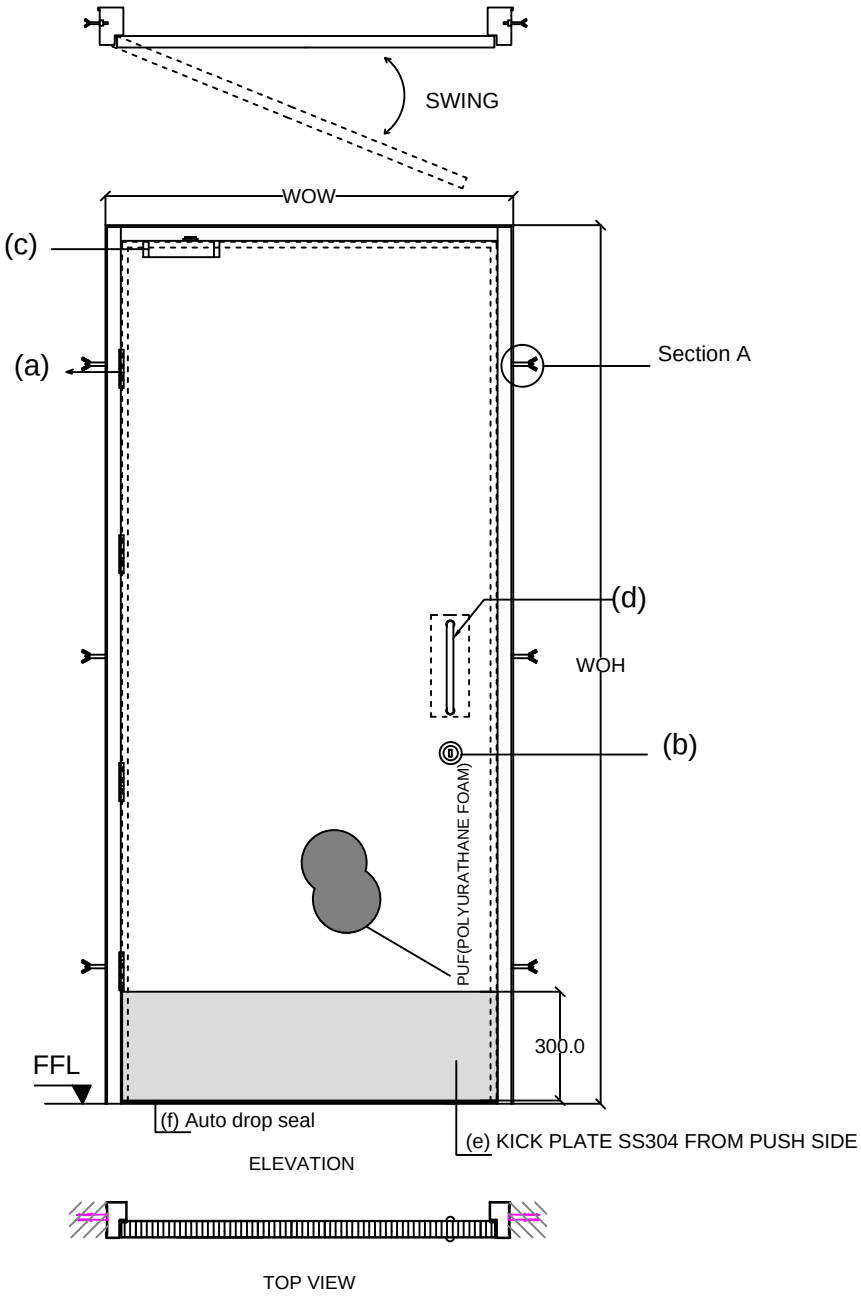


ELEVATION

TOP VIEW

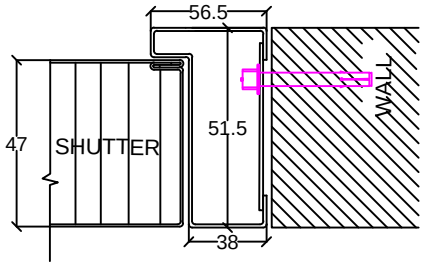

Section A

Abbrevation's:
WOW-Wall Opening Width
WOH-Wall Opening Height
UC-Under Cut
FFL-Finished Floor Level

ASSESORIES DETALES

(a) HINGES: SS Ball bearing butt hinges size 100x75x3mm

(b) LOCK : Mortise Dead lock,Cylinder(Both side key) with Escutcheon ALT-102 (ALTOS make) with 3 keys.

(c) DOOR CLOSER : TS 68 Dorma make

(d) HANDLE : D Handle from one side & push plate(125X325X1.2mm) on other side.

(e) SS Kick plate from push side.

(f) Auto drop seal.

Shutter thickness : 47 mm
Frame Sheet thick : 1.20mm
Shutter sheet thick : 0.80mm
Fixing : On Soliid Brick plasterd wall with Anchors

NOTE:- *All Dimensions are in mm.
*Tolerance:-All Linear Dimensions ±3mm,Others ±0.5mm.
*The Drawing Is For Location of Hardware only. Drawing Does Not Represent The Hardware For More Clarity, Please Go Through Hardware Broucher.

Steel door size

WOW	WOH	TYPE 1	TYPE 2	QUANTITY
900	2200	2	3	5

COLOR- RAL 5015(SKY BLUE)

This drawing & designing is the property of NIHVA TECHNOLOGIES. Not be sold or copy to any other concern.

STEEL DOOR (SINGLE LEAF)

CLIENT APPROVAL

ALL DIMENSION ARE IN mm

	NAME	DATE	SIGN.
DRAWN	OMKAR	28/02/17	
CHECK	SAGAR P.	28/02/17	
REV.			
APPRD.	R.K.	28/02/17	
MFG			

NIHVA TECHNOLOGIES PVT. LTD.
NIHVA TECHNOLOGY PVT. LTD. PUNE
Tel : 020 66304033
Email:- info@nihva.com
Website:-www.nihva.com

CLIENT -
PROJECT -
SITE -
DWG. NO. - NIHVA/16-17/VDR/053
SCALE: NTS | WT: | SHEET: 01 OF 01
If any queries contact : projects@nihva.com