

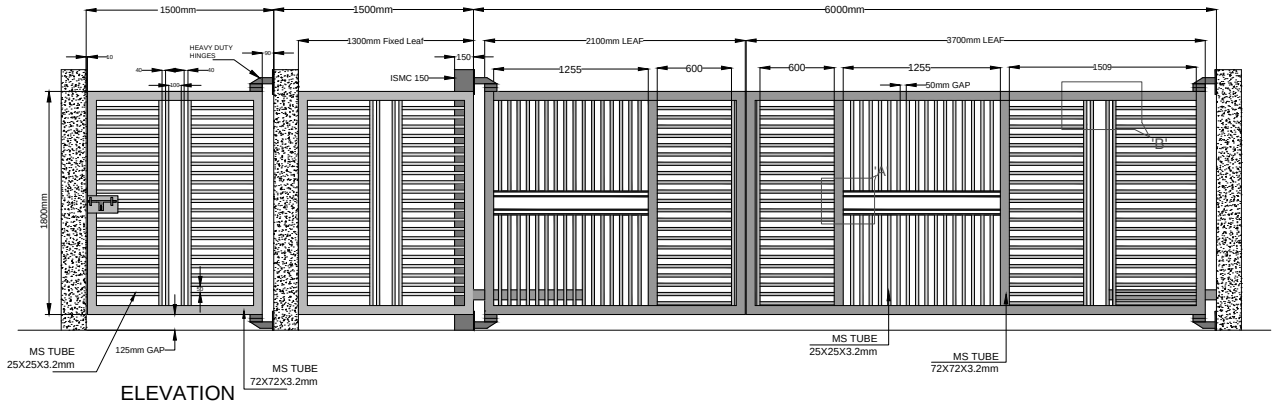



ELEVATION

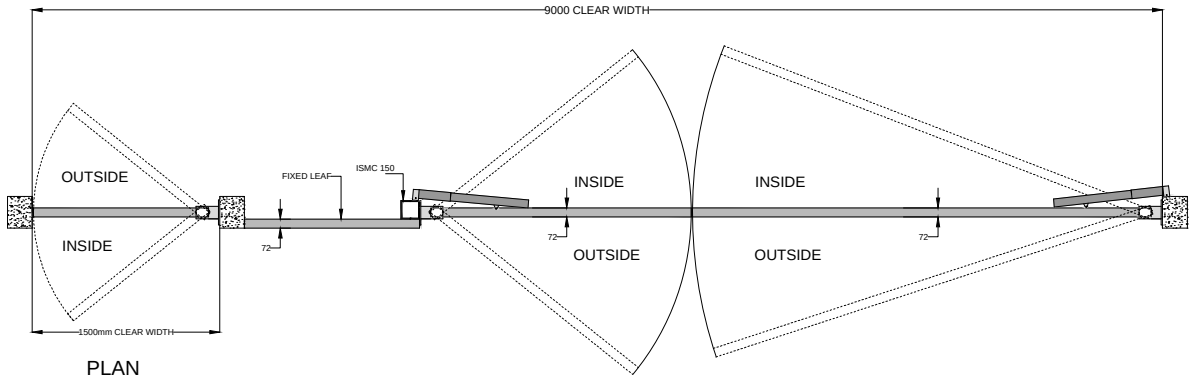

PLAN

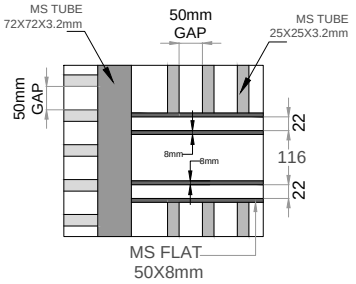

DETAIL VIEW OF 'A'.

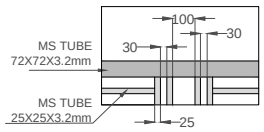

DETAIL VIEW 'B'

SR NO	CLEAR WIDTH	CLEAR HEIGHT	QTY.
1	9000mm	1800mm	01 NOS

This drawing & design is the property of NIHVA TECHNOLOGIES. Not to be sold or copied to any other concern.

TITLE: AUTOMATIC SWING GATE

NIHVA TECHNOLOGIES PVT. LTD.

NIHVA TECHNOLOGIES PVT. LTD. PUNE
Tel : 020 66304033
Email:- info@nihva.com
Website:- www.nihva.com

	NAME	SIGN	DATE
DRAWN	SURAJ		11-05-2018
CHECK	OMKAR		11-05-2018
APPRD.	PRADEEP		11-05-2018

If any queries contact : design@nihva.com

ALL DIMENSION ARE IN mm

CLIENT - JLL

PROJECT -STANDLEE

SITE LOCATION - CHAKAN.

DWG. NO. : NIHVA/18-19/0035 | REV- 0

SCALE: NTS | WT: | SHEET: 01 OF 01