




SIDE VIEW

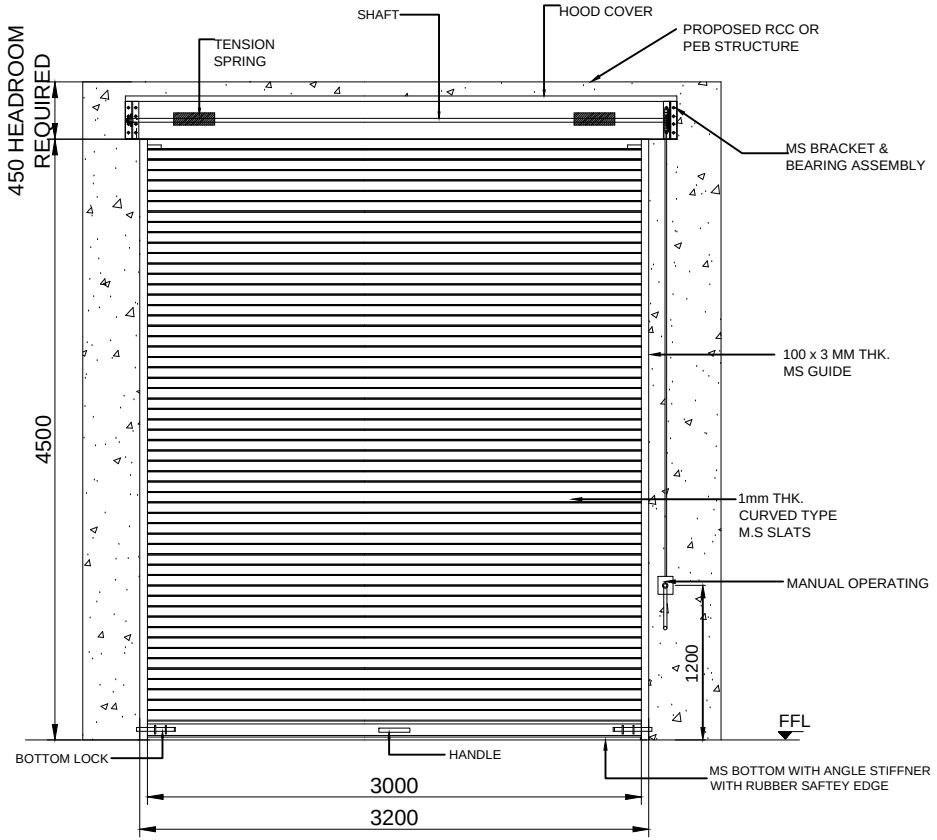


INSIDE ELEVATION

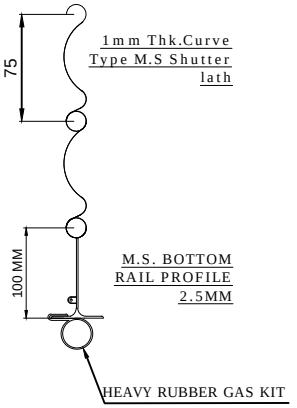

M.S. BOTTOM RAIL PROFILE 2.5MM

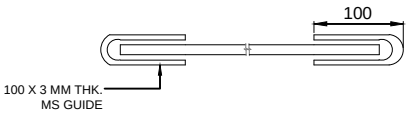

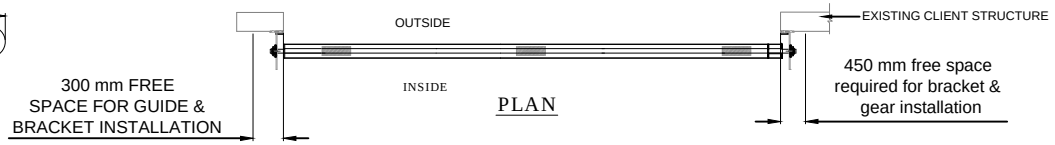

PLAN

TOLERANCE - ±10mm

NOTE-
1. ALL CIVIL WORK WILL BE CLIENT'S SCOPE.
2.STRUCTURE REQUIRED FOR SHUTTER IS IN CLIENT'S SCOPE.
3.FINAL FINISH OF SHUTTER WILL BE IN POWDER COATING OF APPROVED COLOR .

This drawing & design is the property of NIHVA TECHNOLOGIES. Not to be sold or copied to any other concern.

TITLE	GEAR OPERATED ROLLING SHUTTER 3m X 4.5 m Right side gear box.		
	NAME	SIGN	DATE
DRAWN	P.A		16.10.2019
CHECK	G.J		16.10.2019
APPRD.			

NIHVA TECHNOLOGIES PVT. LTD.
NIHVA TECHNOLOGIES PVT. LTD. PUNE
Tel : 020 66304033
Email:- info@nihva.com
Website:- www.nihva.com

CLIENT - PROGRESSIVE INFRA PROJECT PVT. LTD.		
PROJECT -		
SITE LOCATION - PUNE		
If any queries contact : design@nihva.com	DWG. NO. : NIHVA/19-20/0136	REV- R00
ALL DIMENSION ARE IN mm	SCALE: NTS WT:	SHEET: 01 OF 01