

1

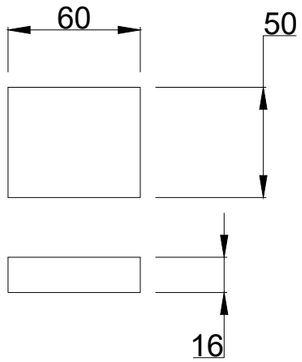

MNTG PLATE - 50 X 60 X 16 MM
MTRL - M.S.

QTY=65 NOS


2

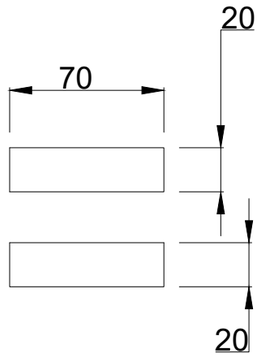

HORIZONTAL SQ. BAR
- 20 X 20 X 70 MM
MTRL - M.S.

QTY=65 NOS

3

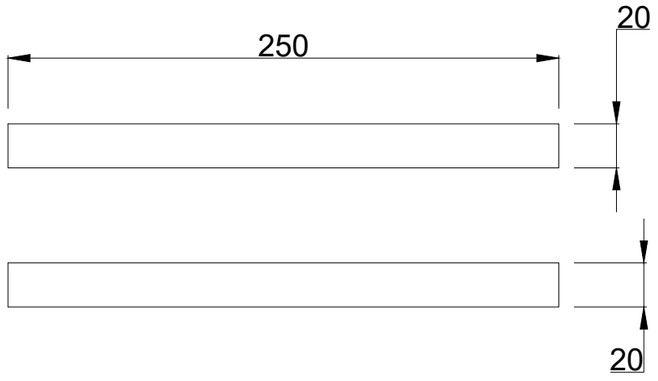


VERTICAL SQ. BAR
- 20 X 20 X 250 MM
MTRL - M.S.

QTY=65 NOS

SUBASSEMBLY AT SHOP
PER HEIGHT MNTG PLATE

QTY=65 NOS

A

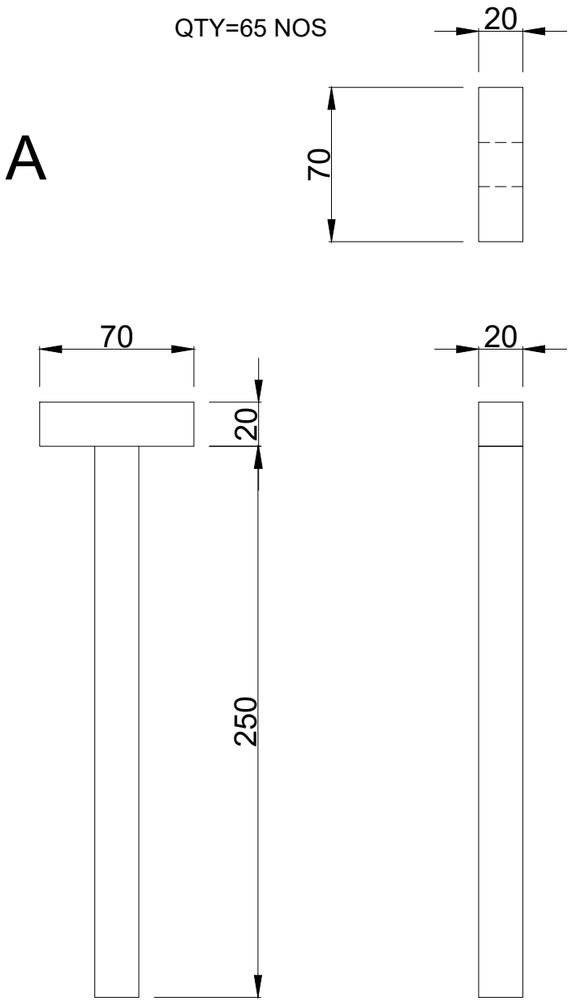


MNTG PLATE - 50 X 60 X 16 MM
MTRL - M.S.

QTY=65 NOS

FINAL FITTING AT SITE
PER HEIGHT MNTG PLATE

QTY=65 NOS

B

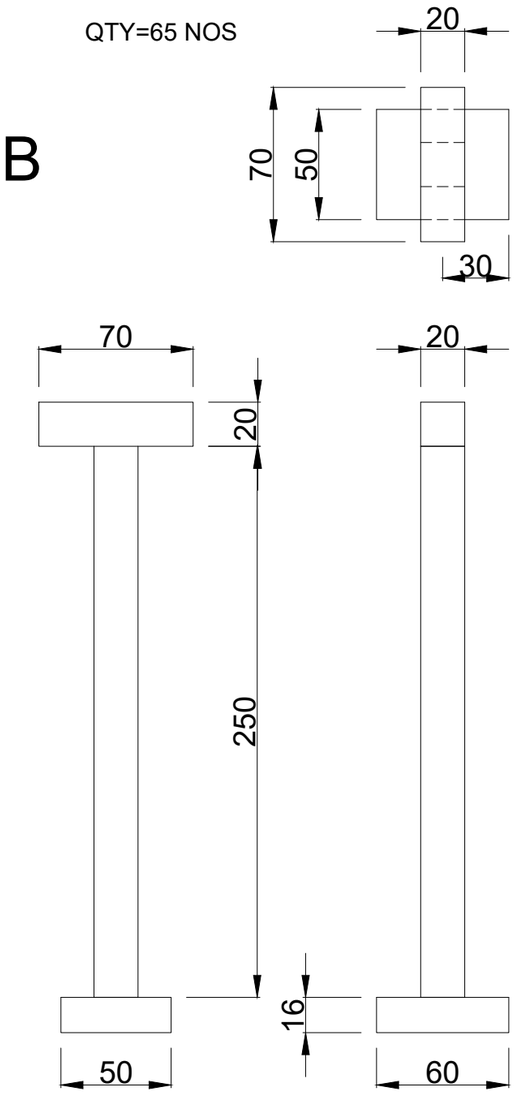

This drawing & design is the property of NIHVA TECHNOLOGIES. Not to be sold or copied to any other concern.

TITLE:- 4 LEAF CRM DOOR 10			NIHVA TECHNOLOGIES PVT. LTD. PUNE Tel : 020 66304033 Email:- info@nihva.com Website:- www.nihva.com
	NAME	DATE	SIGN
DRAWN	M.SUTAR	15/06/2022	
CHECK	M.SUTAR	15/06/2022	
APPRD.			
CLIENT - NIHVA TECHNOLOGIES PVT.LTD			
LOCATION -			
PRODUCT - SLIDING DOOR			
If any queries contact : design@nihva.com	DWG NO:-NIHVA/22-23/MNFG/0036		REV- 0
ALL DIMENSION ARE IN mm	SCALE: NTS	SCALE:-- 1:1	SHEET: 01 OF 01

	Date	Revised By